

143.7 m². Room to live.

Sixteen spruce glulam homes, developed from the manufacturer’s roof and glazing concept. A coordinated architectural study for your appointed architect, matching the selected interactive model.

16

HOMES

143.7

USABLE m² / HOME

2,299.2

DEVELOPMENT m²

A measured design, with choices

- 01

Outside enclosure 10.400 x 11.4148 m. Ground usable 96.7121 m² plus loft 46.9879 m². Both master arrangements total 143.7 m².
- 02

The wider option uses the established right wall as its datum; private divisions are adjusted to keep garden access. The minimum measured separation between enclosed house faces is 3.29 m. House setting-out points and rotations stay fixed.
- 03

Two downstairs rooms each measure 3.4675 x 5.0675 m. Bedroom, dining and library options share the same shell.
- 04

The dressing loft front and stair/landing move forward 141.43 mm to compensate for the extra partitions. Both layouts retain glass toward the living room.
- 05

Usable area excludes wall/door-reveal bands, ground stair reservation, upper void and loft floor below 2.10 m clear headroom. Fixed cabinetry is included.

Drawing register

SHEET	DRAWING	SCALE
A000	Design brief and drawing register	NTS
A001	Overall site arrangement	1:500
A101	Upper terrace plots 5 and 6	1:250
A102	Middle terrace plots 3 and 4	1:250
A103	Lower terrace plots 1 and 2	1:250
A201	Dimensioned ground floor	1:50
A202	Both master-suite arrangements	1:50
A203	Three lower-left room options	1:25
A204	Bathroom and laundry options	1:25
A301	Four external elevations	1:100
A302	Roof plan and building sections	1:100 / 1:50
A401	Area and placement schedules	NTS
A402	Shared amenities and design coordination	1:150

CONCEPT CO4 / ARCHITECT REVIEW

Shared dimensions match the CO4 website model. This set does not establish permit rights, legal setbacks or construction details. Plot trace and terrace levels are provisional. Structural, services, drainage, fire and energy designs require appointed consultants.

Do not set out from rounded dimensions. The metre-based CAD and area audit retain full precision.

CONCEPT DESIGN – NOT FOR CONSTRUCTION OR PERMIT SUBMISSION

Dimensions in metres unless stated. Print at 100% on A2 (594 x 420 mm).

PROJECT KH-16-143.7

Brief: 143.7 m² usable per home

SCALE

NTS

DRAWING

A000

SHEET

01 / 13

Overall arrangement / 16 homes of 143.7 m²

Existing setting-out points and orientations retained. Perimeter divisions, private gardens and shared green area.



PLOT	HOMES	USABLE m²
6	3	431.1
5	3	431.1
4	3	431.1
3	2	287.4
1	3	431.1
2	2	287.4

- 01 Upper plots 5/6: +6.00 m. Middle plots 3/4: +3.00 m. Lower plots 1/2: +0.00 m. House finished floors +0.30 m above terrace; relative levels only.
- 02 Only the two source road corridors are shown. Parking access meets the road edge; no extra internal street is introduced.
- 03 Rear gardens on plots 1, 3 and 4; left garden at Thyme and right garden at Arbutus. Larger homes require more compact terraces.
- 04 Private divisions are landscape proposals, not cadastral boundaries. Gate locations and retaining walls need measured survey coordination.

Upper terrace / homes, gardens and arrivals

143.7 m² usable per home. Enclosed footprint 10.400 x 11.4148 m; porch additional.



HOME	NAME	FFL	GARDEN	PLOT GAP*	PARCEL GAP*
P6-01	Olive	+6.30	front	2.44	2.44
P6-02	Cypress	+6.30	front	5.05	1.40
P6-03	Juniper	+6.30	front	4.23	1.40
P5-01	Cedar	+6.30	front	2.36	2.36
P5-02	Laurel	+6.30	front	5.19	0.90
P5-03	Myrtle	+6.30	front	5.30	0.90

* Shortest enclosed-face distance to the plot or private division. These are measured model clearances, not approved setbacks. Roof overhangs and wall construction require separate review.

Every home retains a 2.70 x 5.20 m parking bay and direct road connection. Gate fabrication is not defined.

Middle terrace / homes, gardens and arrivals


143.7 m² usable per home. Enclosed footprint 10.400 x 11.4148 m; porch additional.



HOME	NAME	FFL	GARDEN	PLOT GAP*	PARCEL GAP*
P3-O1	Sage	+3.30	rear	3.40	3.35
P3-O2	Rosemary	+3.30	rear	4.64	3.45
P4-O1	Almond	+3.30	rear	1.97	1.75
P4-O2	Fig	+3.30	rear	4.70	1.75
P4-O3	Pomegranate	+3.30	rear	2.86	1.85

* Shortest enclosed-face distance to the plot or private division. These are measured model clearances, not approved setbacks. Roof overhangs and wall construction require separate review.

Every home retains a 2.70 x 5.20 m parking bay and direct road connection. Gate fabrication is not defined.

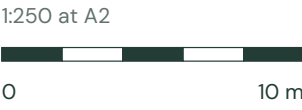

Lower terrace / homes, gardens and arrivals


143.7 m² usable per home. Enclosed footprint 10.400 x 11.4148 m; porch additional.



HOME	NAME	FFL	GARDEN	PLOT GAP*	PARCEL GAP*
P1-01	Jasmine	+0.30	rear	1.29	1.29
P1-02	Lavender	+0.30	rear	5.46	1.60
P1-03	Iris	+0.30	rear	0.39	0.39
P2-01	Thyme	+0.30	left	1.42	1.42
P2-02	Arbutus	+0.30	right	0.52	0.52


* Shortest enclosed-face distance to the plot or private division. These are measured model clearances, not approved setbacks. Roof overhangs and wall construction require separate review.

Every home retains a 2.70 x 5.20 m parking bay and direct road connection. Gate fabrication is not defined.

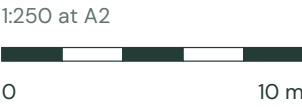

Ground floor / furnished arrangement

96.7121 m² counted usable. All three left-room options use this enclosure.

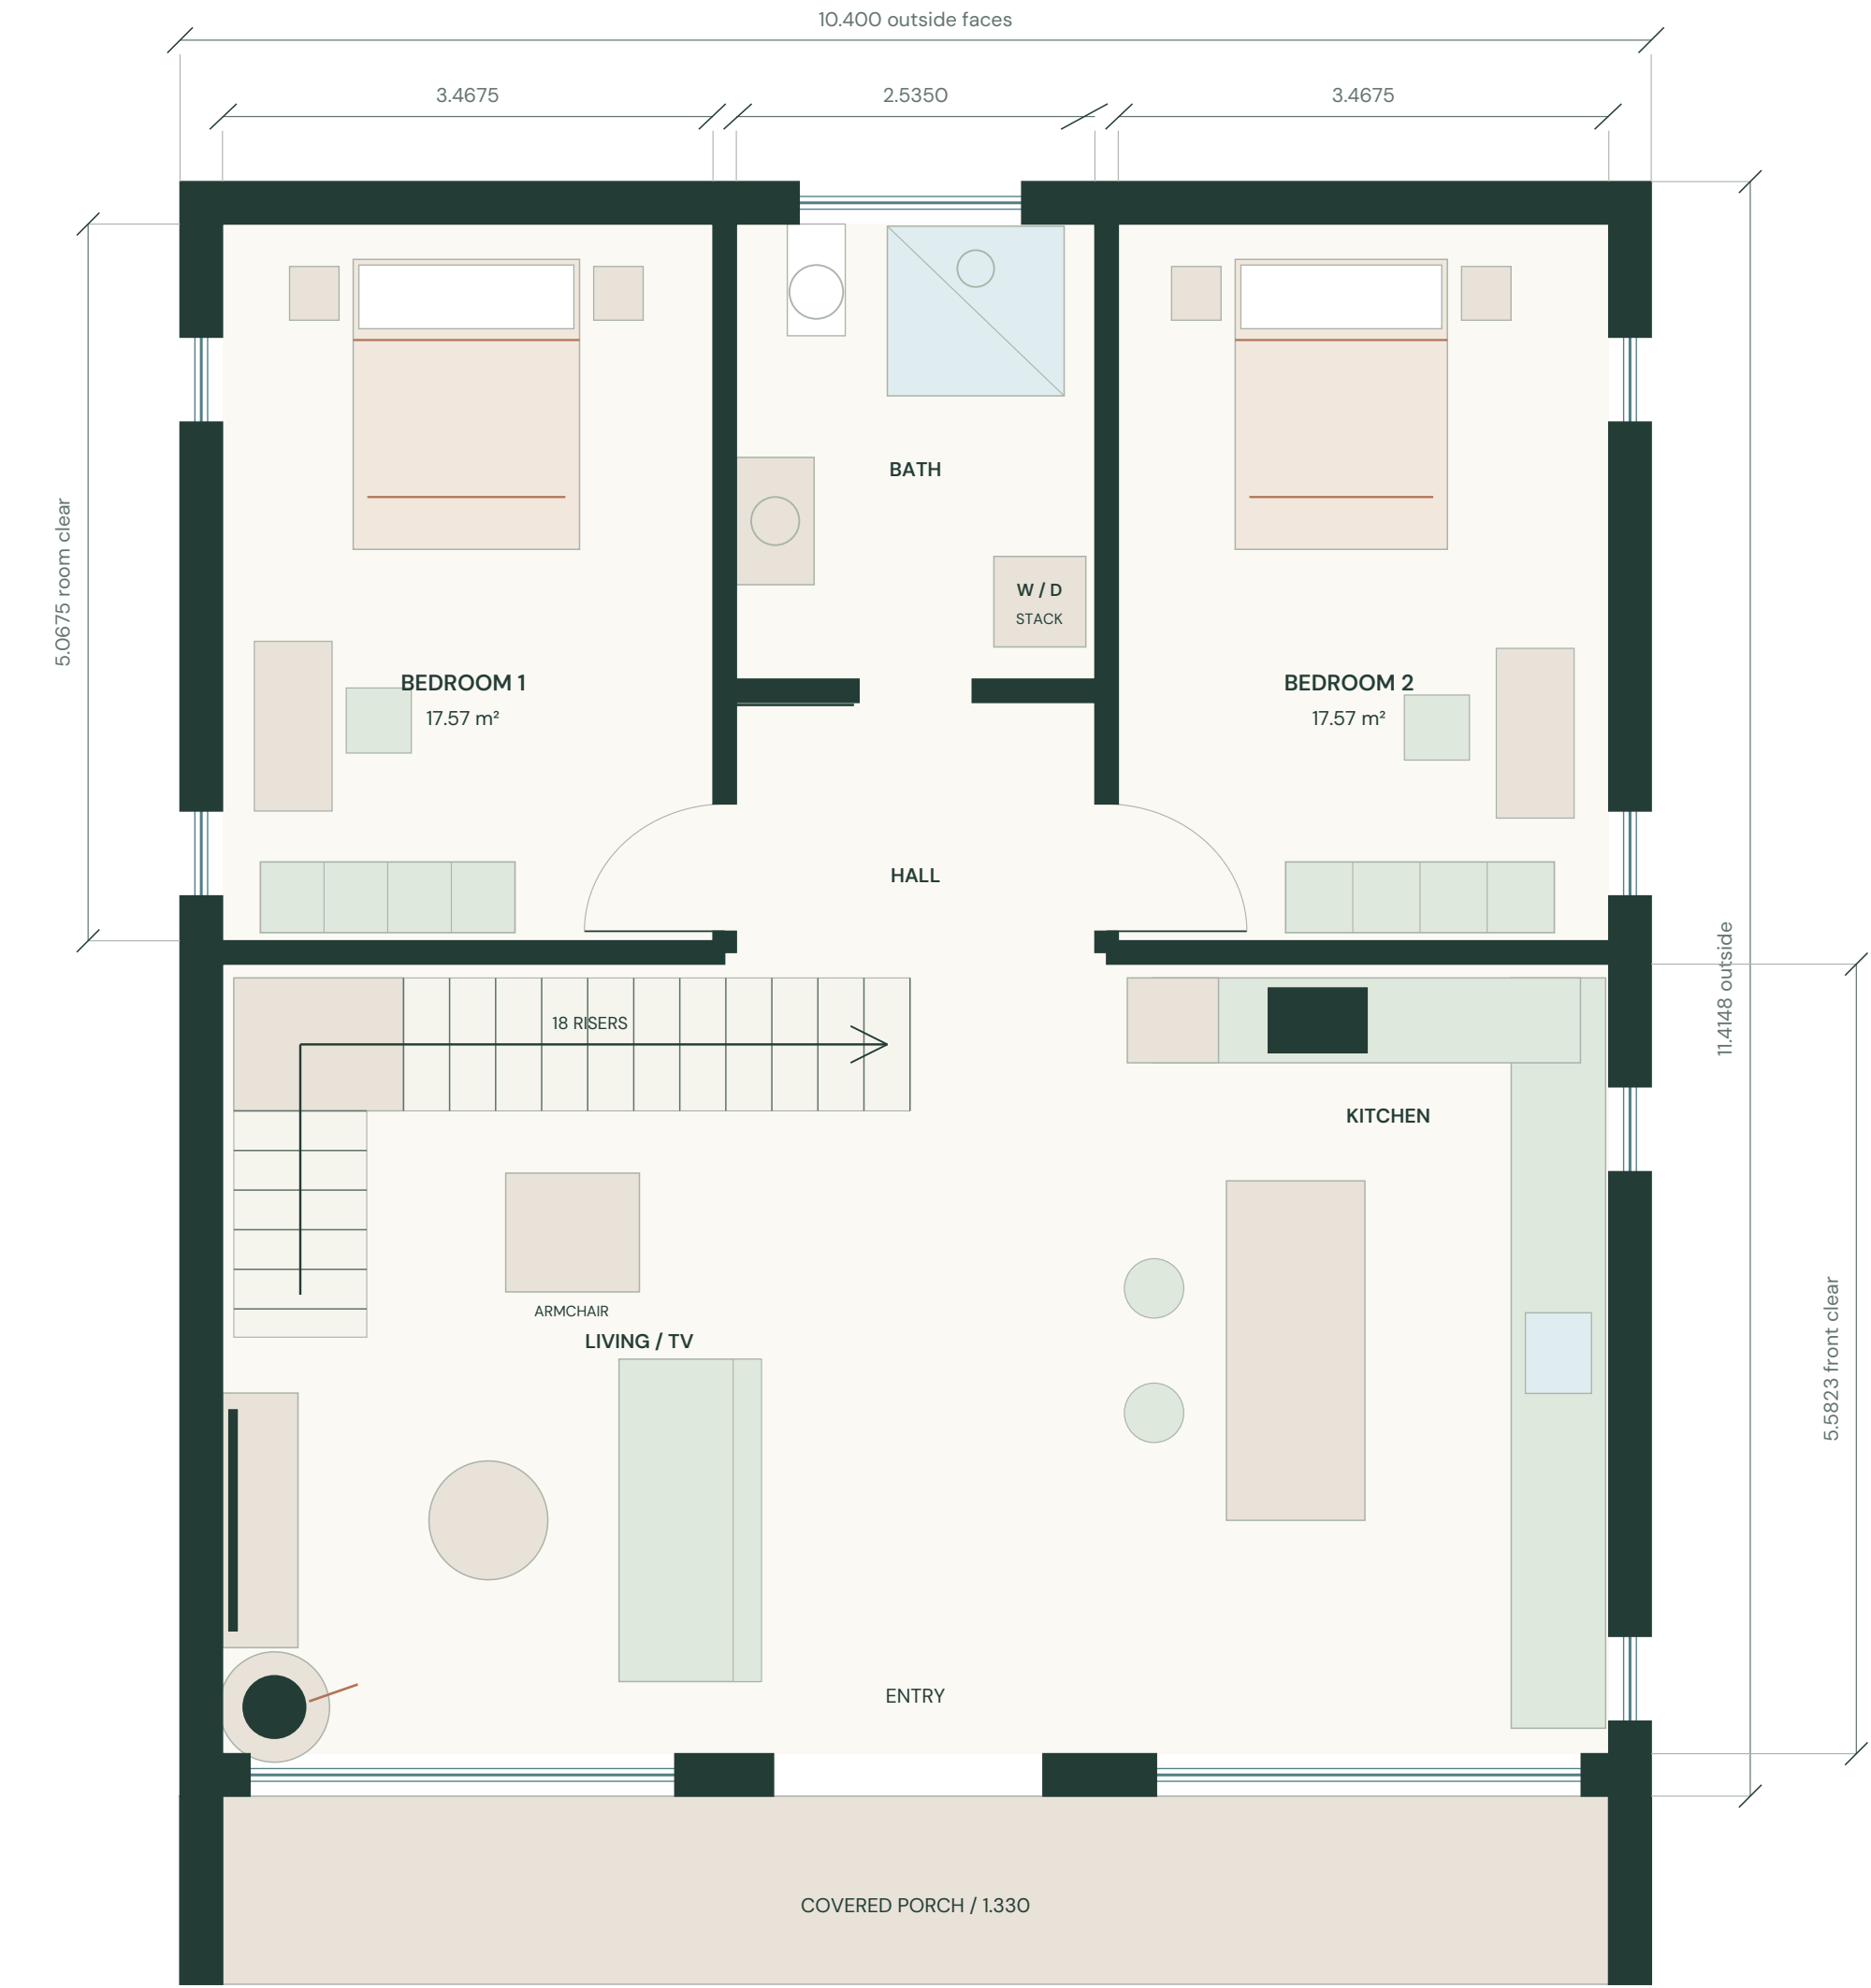

Space for everyday life

GROUND FLOOR	AREA m²
Inside external walls	105.9850
Less full partition bands	3.2757
Less stair / guard reservation	5.9972
USABLE GROUND FLOOR	96.7121


- 01 Each rear room: 17.5716 m² clear before furnishings. Central bath: 2.535 x 3.2175 m clear between finished walls. External walls 300 mm; internal wall bands 165 mm.
- 02 Side-wall TV faces the sofa. The stair returns against the bedroom wall and a separate armchair faces the seating area; the 2.40 m island has clear working aisles and drawers below the kitchen windows.
- 03 Stair concept: 18 equal rises over 3.235 m (179.72 mm). Lower goings 280 mm; upper goings 325.45 mm. Clear flight 940 mm; upper landing 1.160 x 1.040 m. Verify structure, handrails and headroom.
- 04 This ground plan shows the open-suite stair position. With the dressing loft, the stair reservation moves 141.43 mm toward the front; usable area is unchanged.
- 05 1.330 m clear sheltered porch between the extended side walls. The open porch is excluded from usable and enclosed floor area.

CO4: wider rooms and bathroom; shorter enclosure; stairs beside the bedroom partition. Ground bath retains stacked laundry. Both master arrangements retain the glazed front.




A / Open master suite

Bathroom partition with open clothes storage; retained glazed frontage.

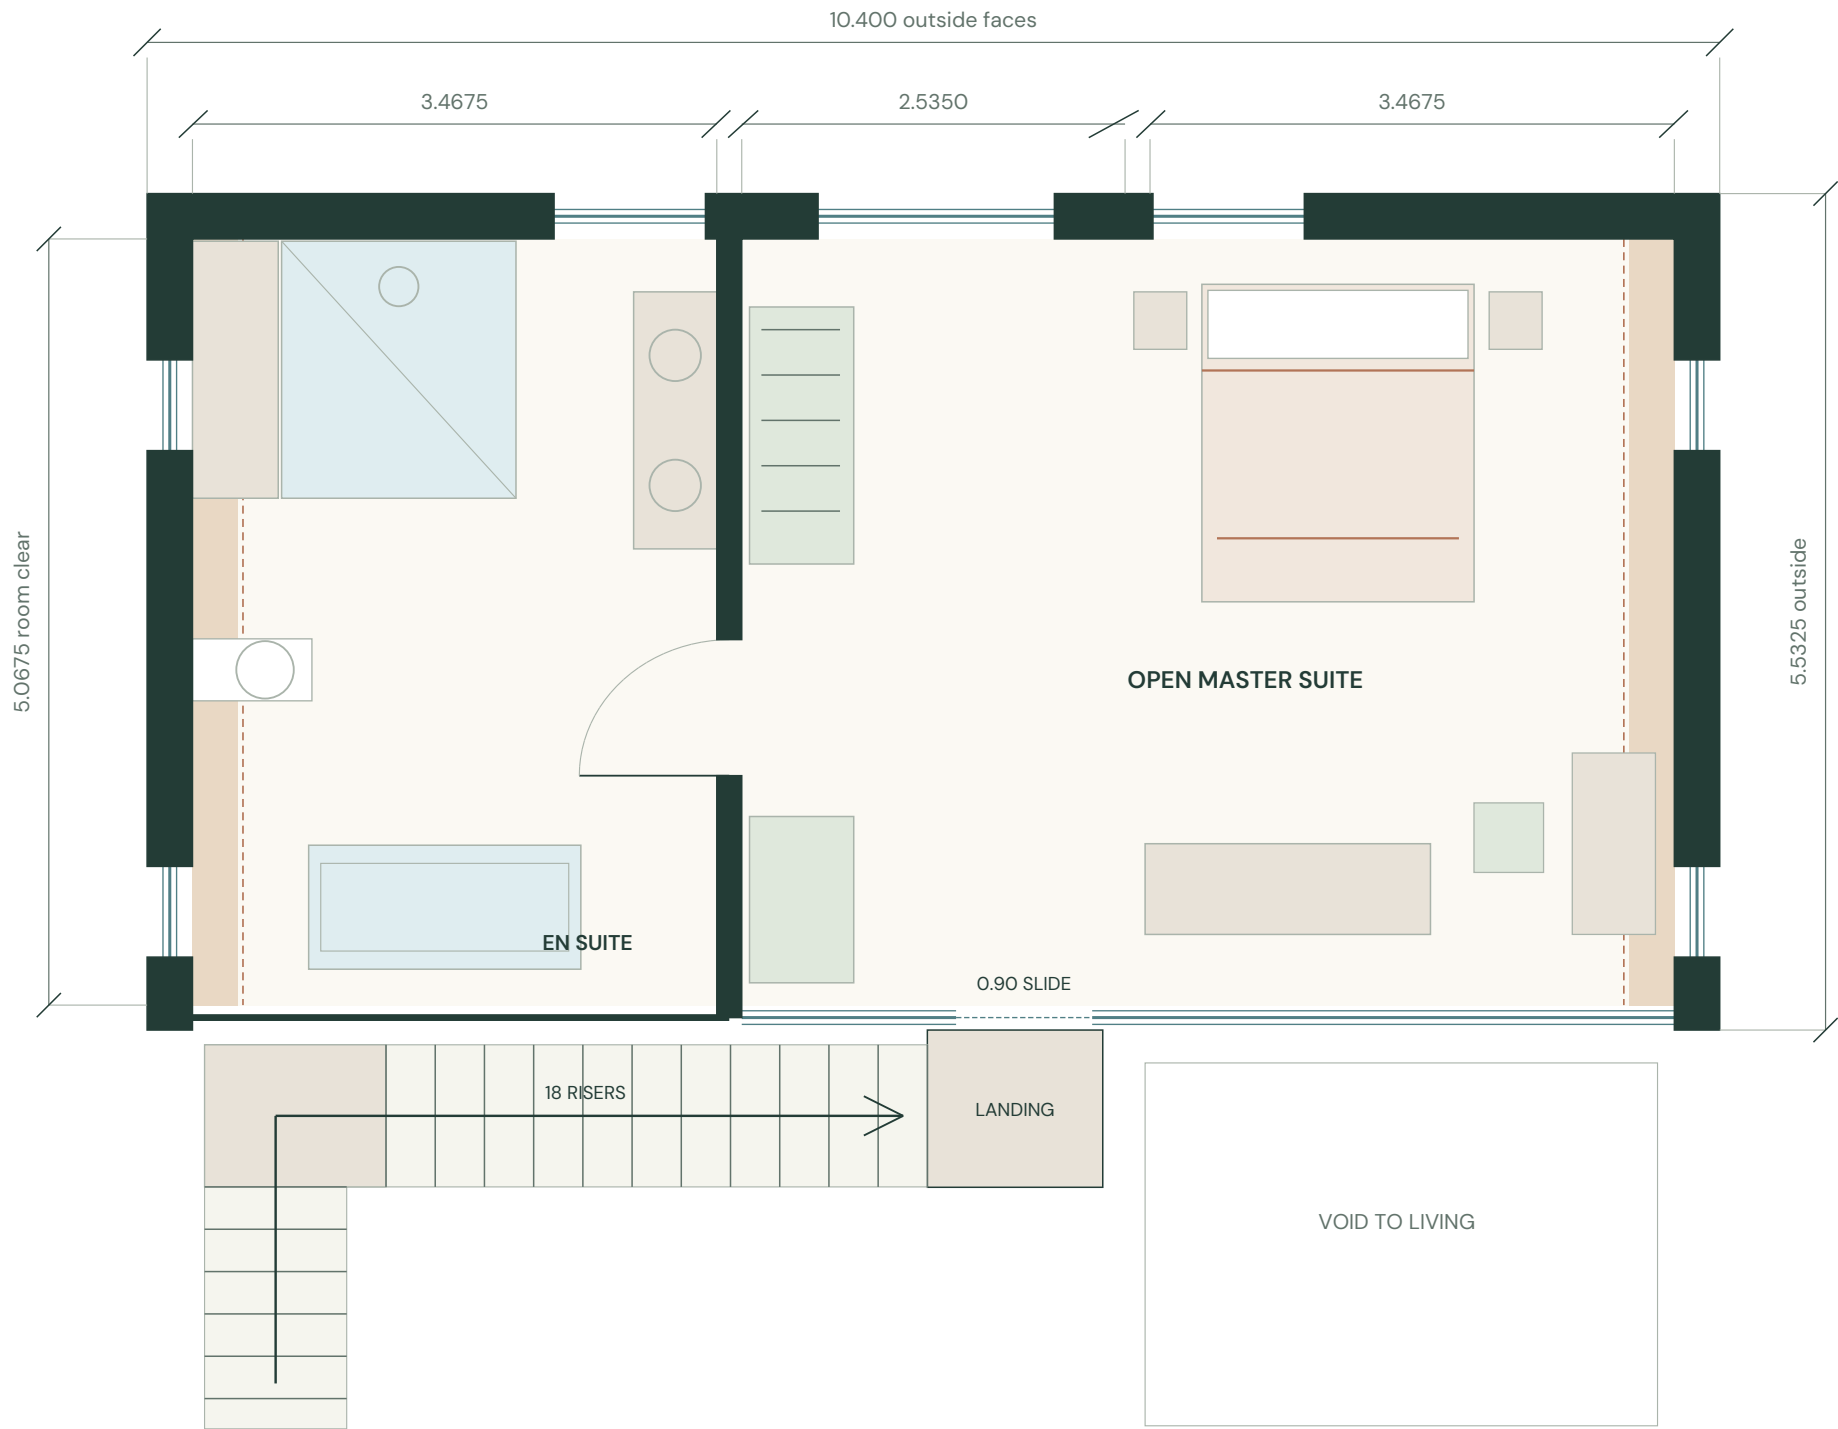

B / Walk-in wardrobe suite

Glazed frontage and landing advance 141.43 mm.

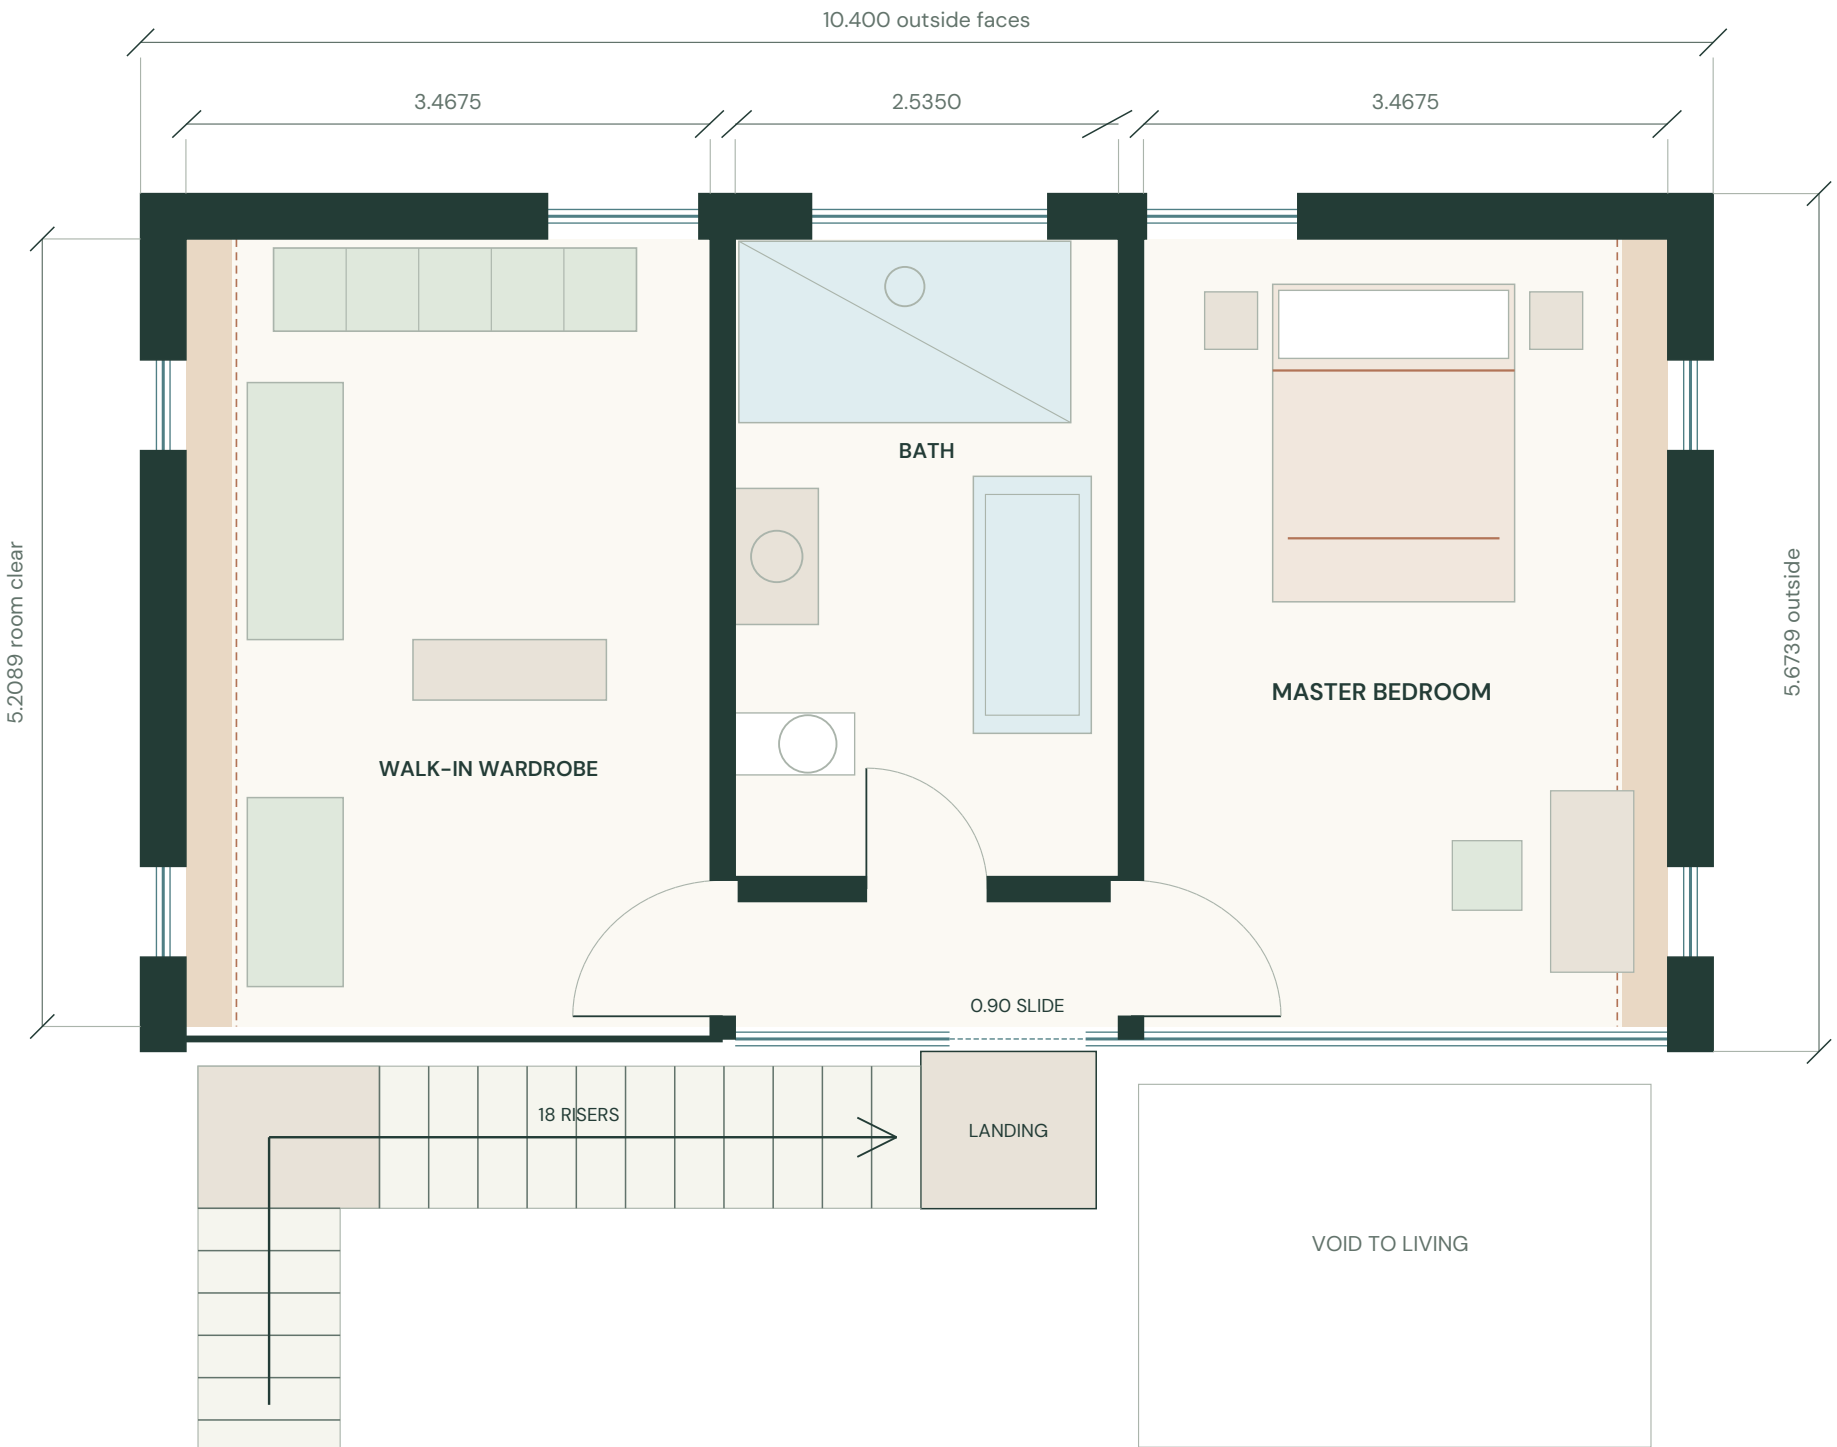

COUNTING METHOD	OPEN	DRESSING
Clear room floor	48.8254	48.9103
Below 2.10 m (excluded)	3.0439	3.1288
Landing included	1.2064	1.2064
USABLE LOFT	46.9879	46.9879


Ochre bands identify the low-headroom floor excluded from usable area. The threshold is a project counting assumption, not a statement of statutory habitable-room compliance. Cabinetry in these strips stays under the roof.

Both loft choices plus the ground floor total 143.7 m². The 0.90 m sliding entrance aligns with the landing.


The lower-left room / three ways to live

Identical finished dimensions: 3.4675 x 5.0675 m. Each option: 17.5716 m².


01 / BEDROOM

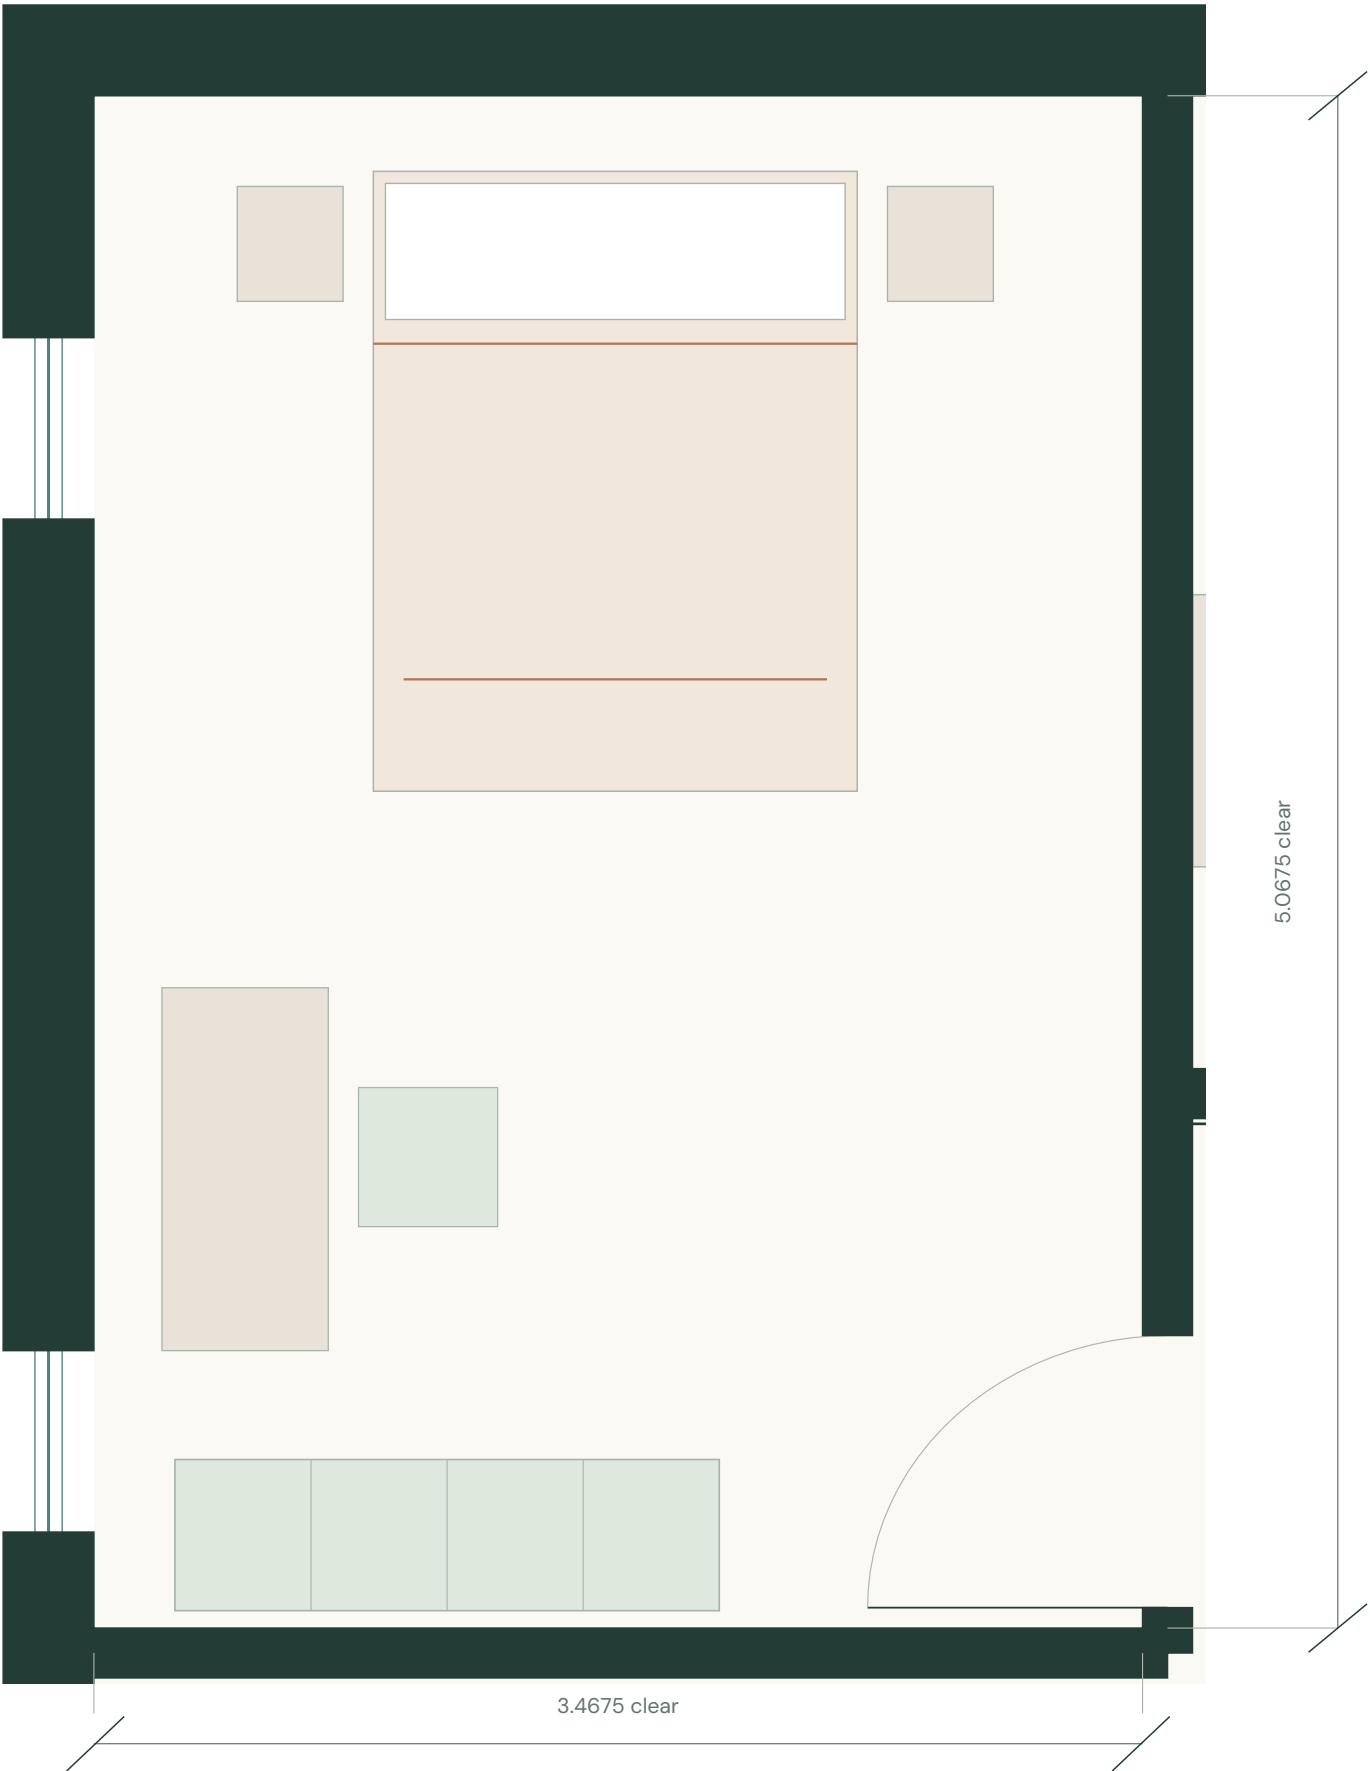

02 / ROUND DINING

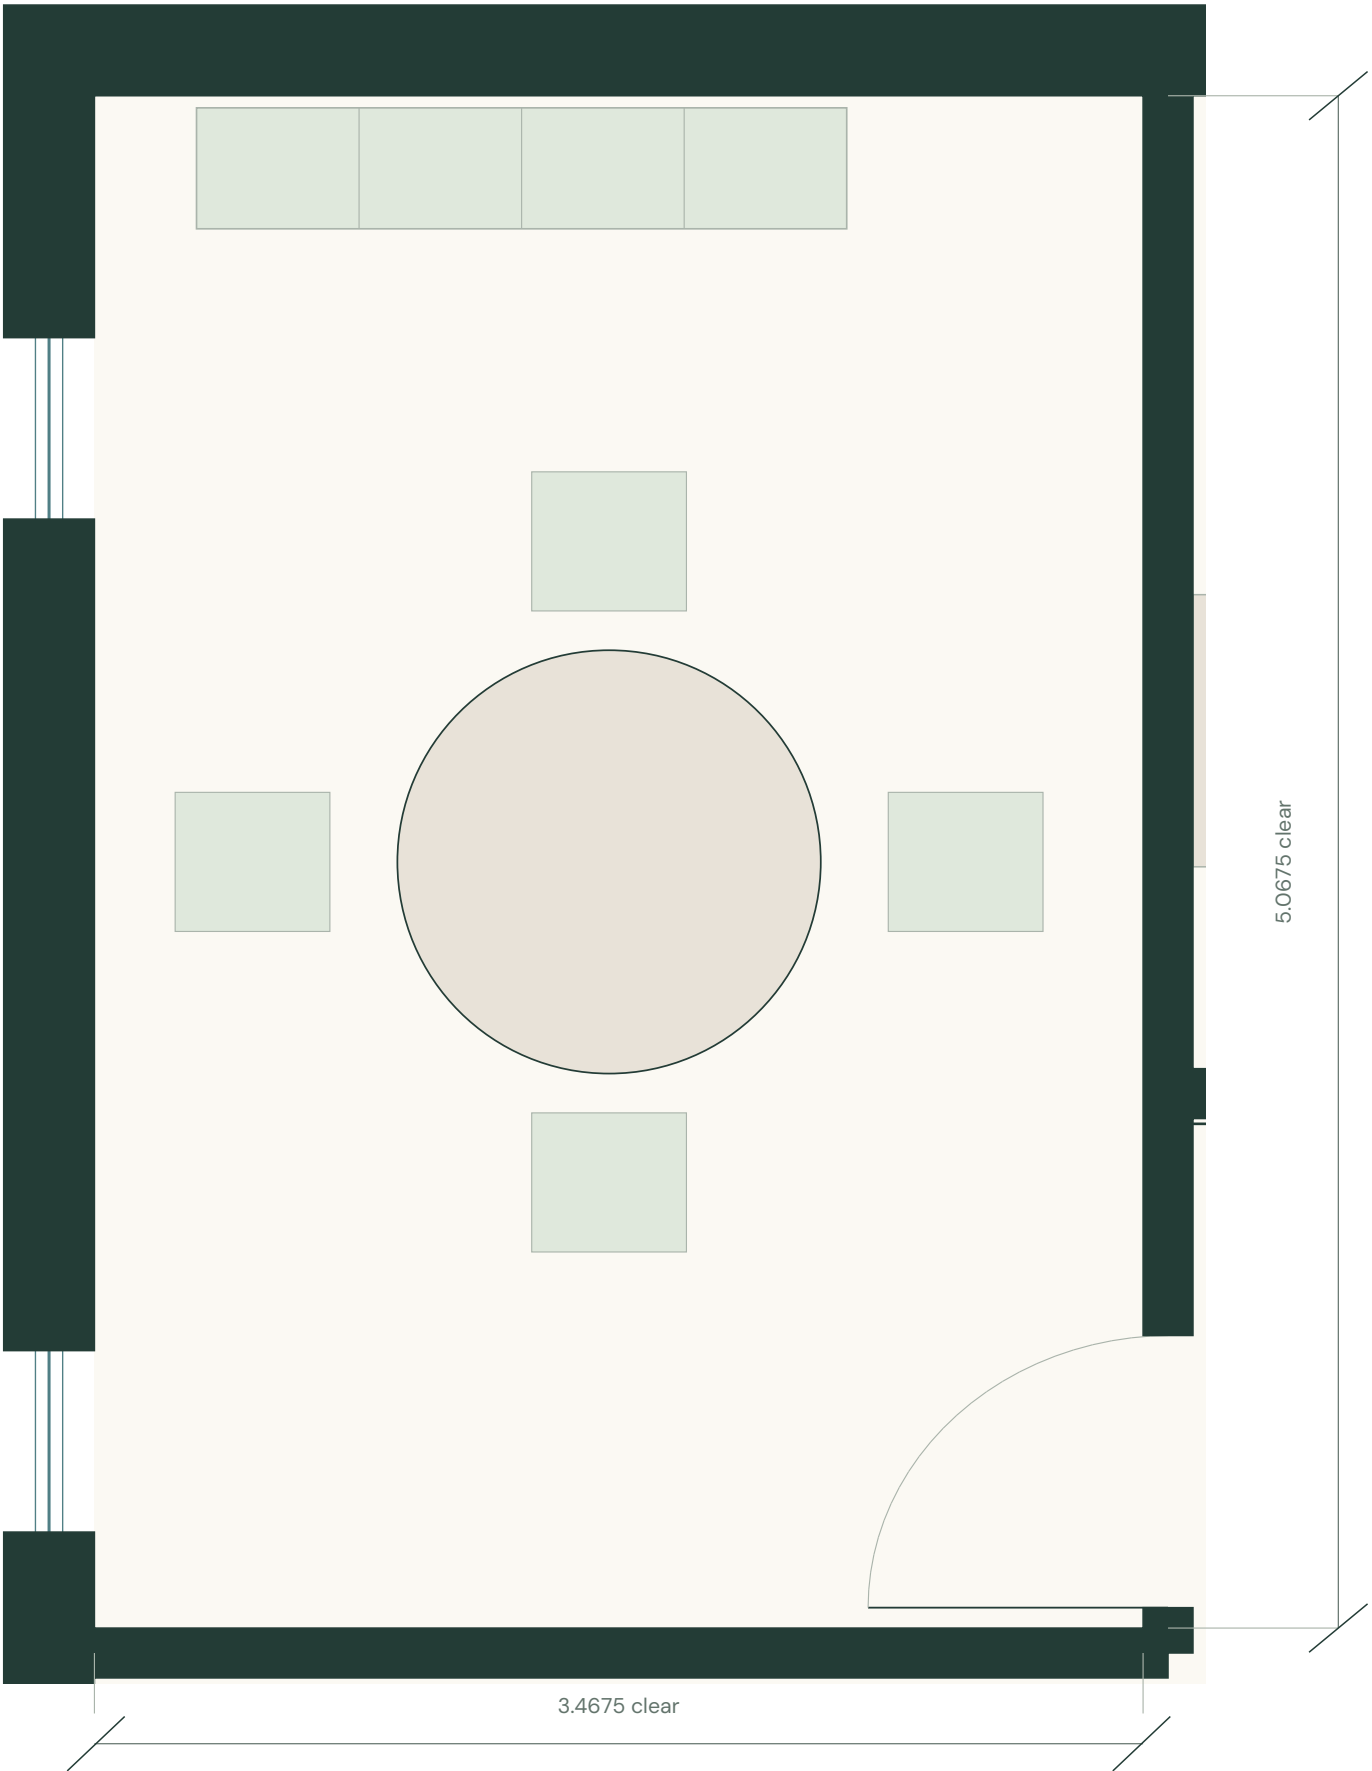


03 / LIBRARY + DESK

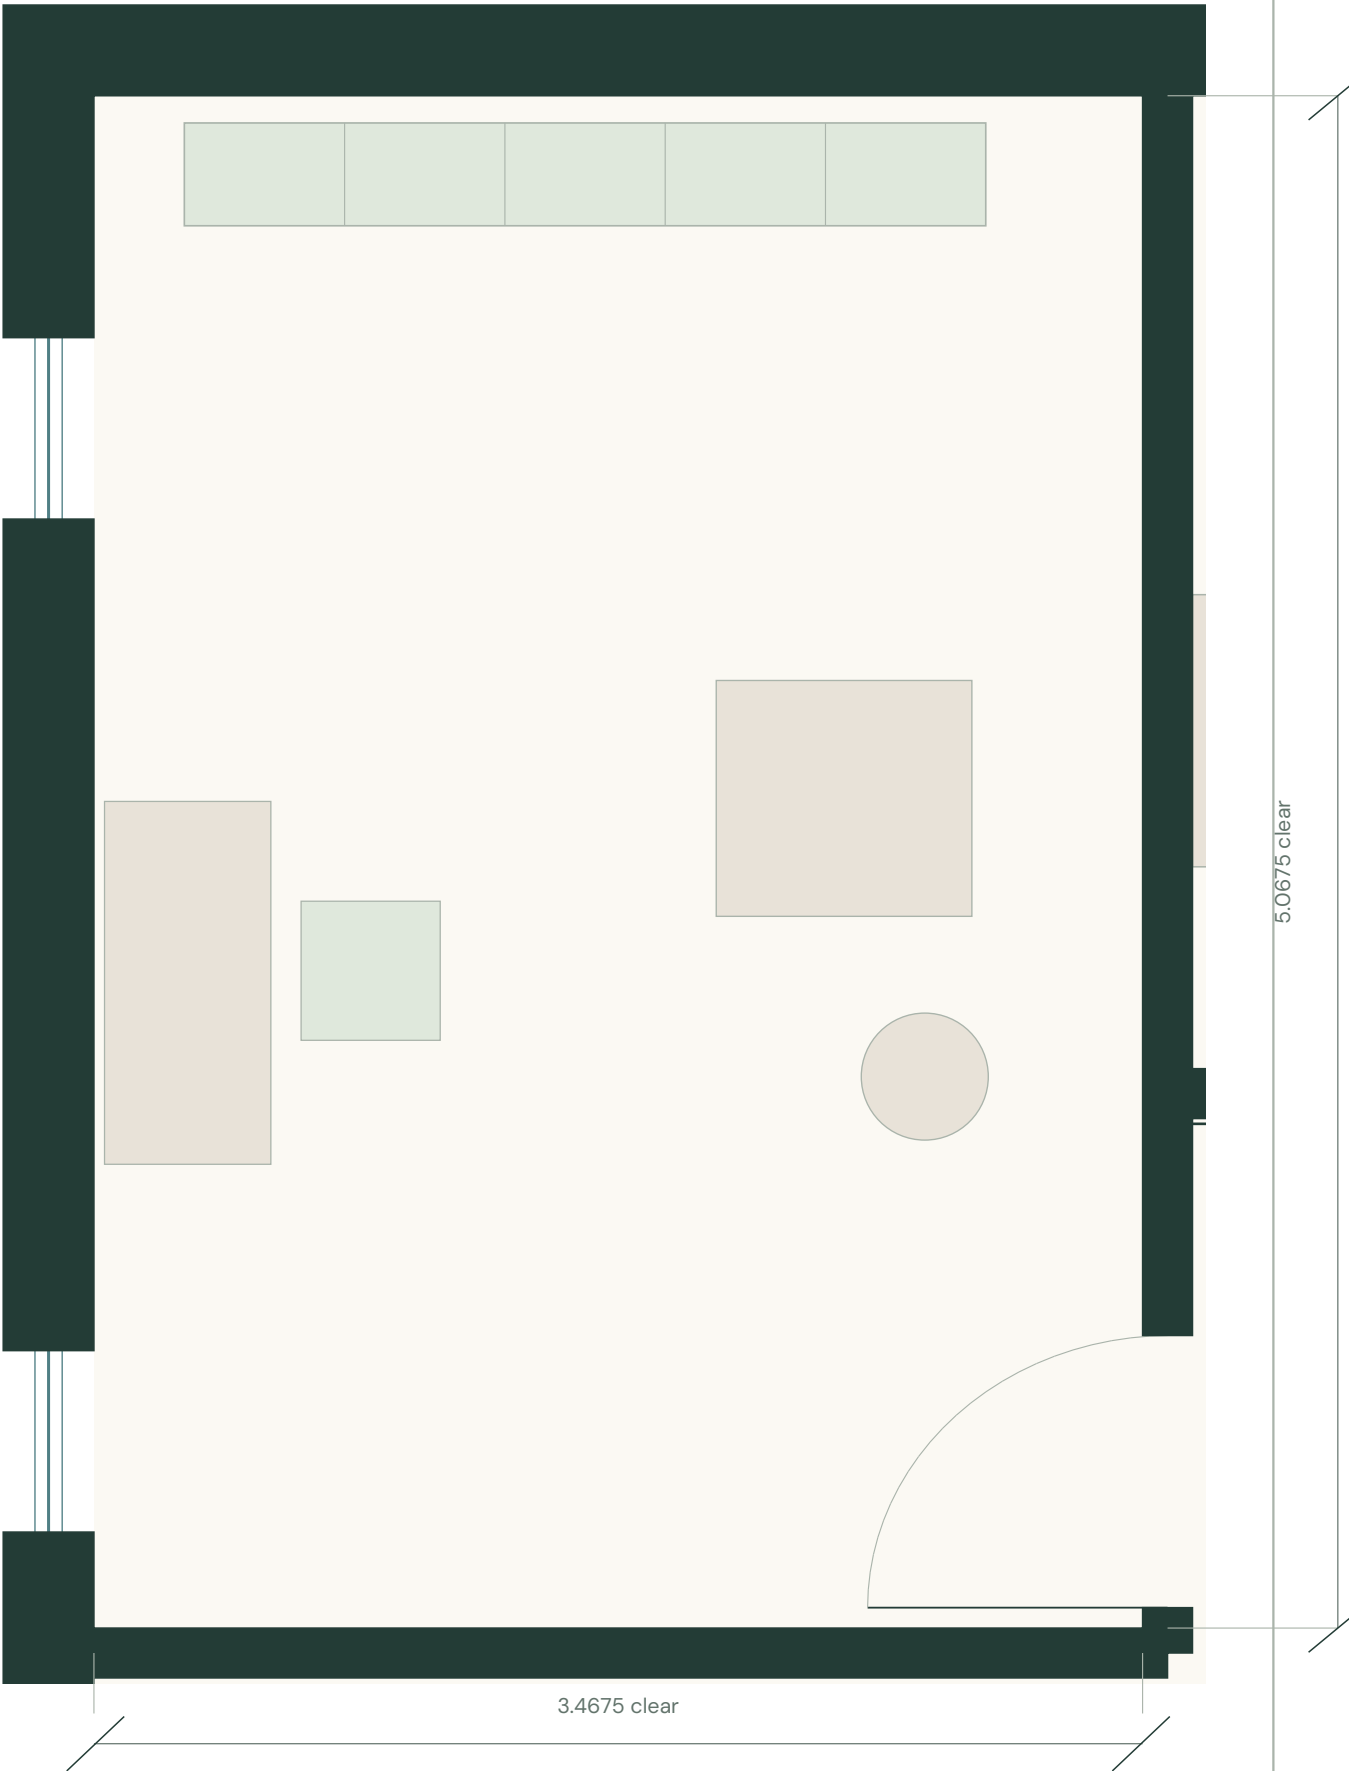

Bathrooms / comfort, laundry and choices

1:25. Fixture positions match the CO4 model. Blue bath outlines are optional; shower-only replaces the bath with a towel bench.


GROUND / SHOWER + LAUNDRY

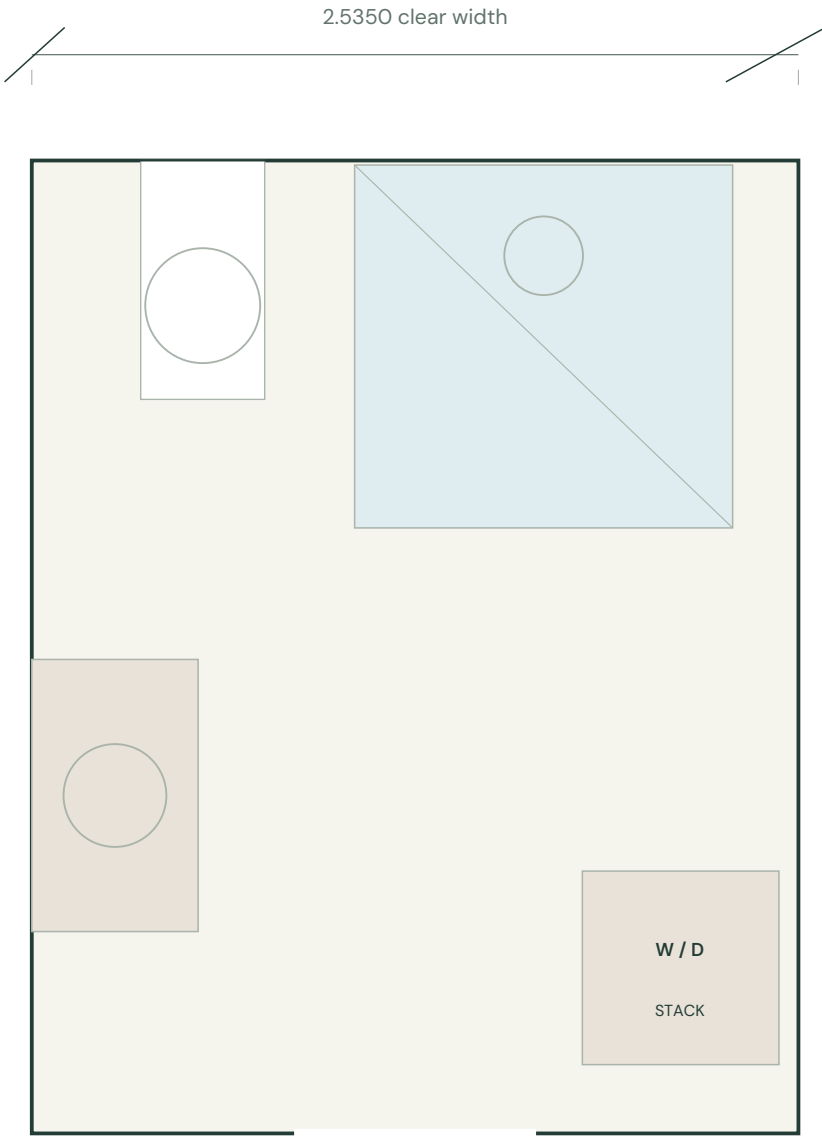

A 1.25 x 1.20 m shower, wall-backed WC, 0.90 m vanity and a 0.64 x 0.65 m stacked washer/dryer. Sliding entry avoids a door swing into appliances.


Bathroom variants do not alter the floor-area total. Clothes storage flanks both sides of the open-suite bathroom doorway. Plumbing, waterproofing, ventilation and electrical zones require detailed coordination.

OPEN SUITE / SHOWER + BATH

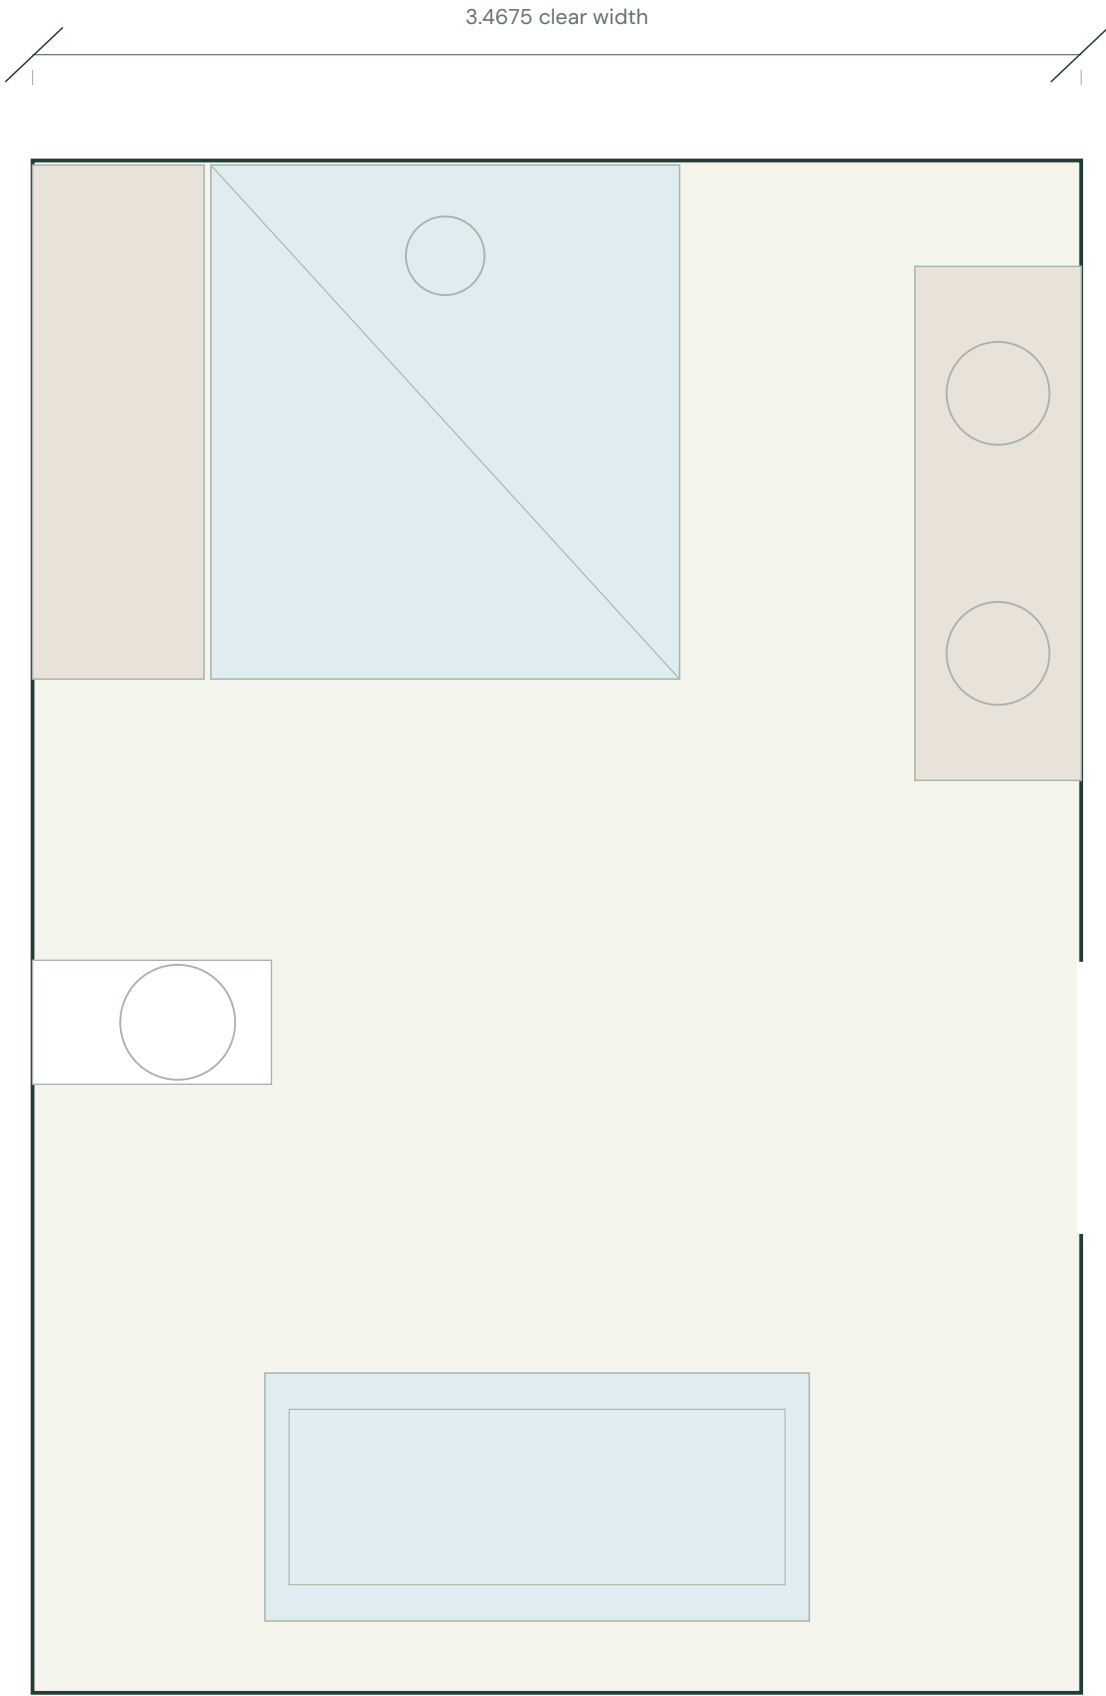

A 1.55 x 1.70 m walk-in shower and 1.70 m wall-backed double vanity. Optional 0.82 x 1.80 m bath; remove it for a towel bench and open floor.

WALK-IN SUITE / SHOWER + BATH

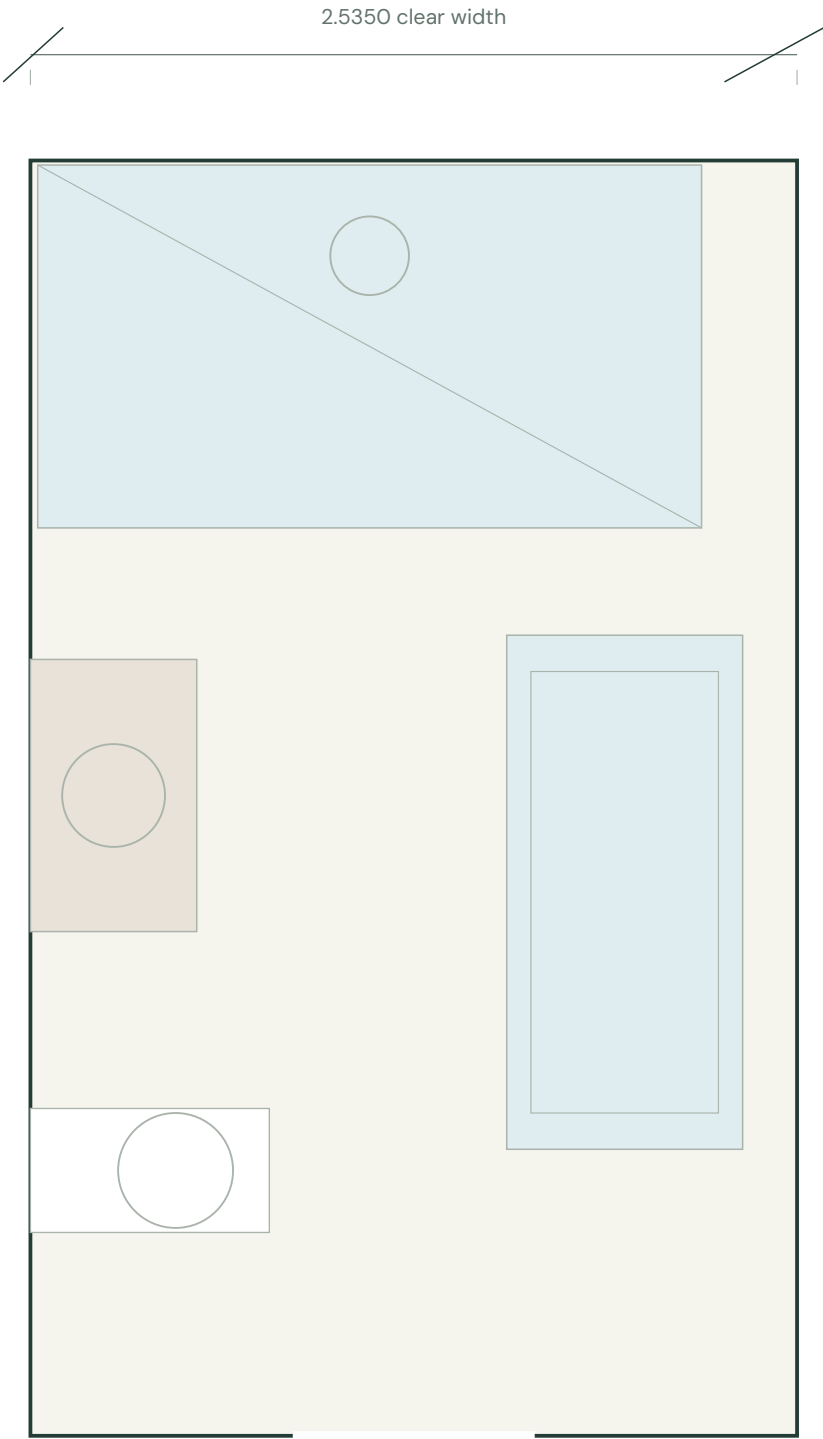

A 2.195 x 1.20 m shower, wall-backed vanity and side-wall WC. Optional 0.78 x 1.70 m bath keeps an approximately 1.03 m aisle beside the vanity.

Elevations / warm spruce and sage roofs

Horizontal timber courses, sage green standing-seam metal and sheltered porches.




FRONT ELEVATION

Roof pitch 30°. Loft FFL +3.235 m. Knee structure +5.235 m. Ridge structure +8.151 m. Approximate roof cap +8.481 m above FFL.




REAR ELEVATION

Roof pitch 30°. Loft FFL +3.235 m. Knee structure +5.235 m. Ridge structure +8.151 m. Approximate roof cap +8.481 m above FFL.

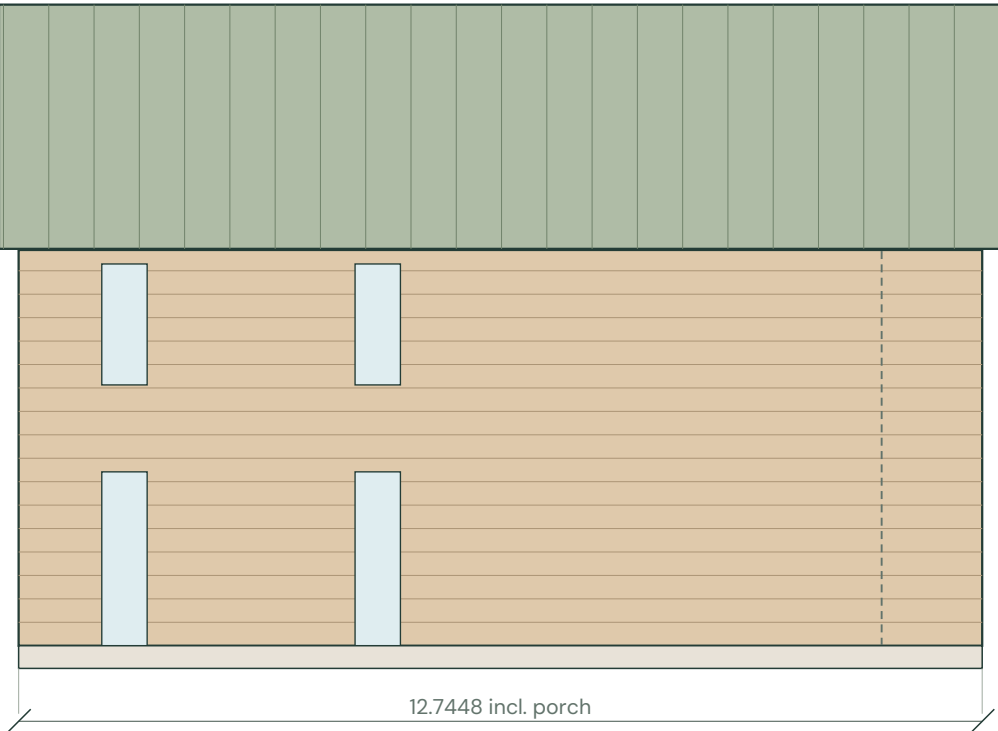

LEFT ELEVATION

The wider design raises the ridge to retain the 30° pitch. Porch wings extend 1.330 m. All levels are relative to each house finished floor.

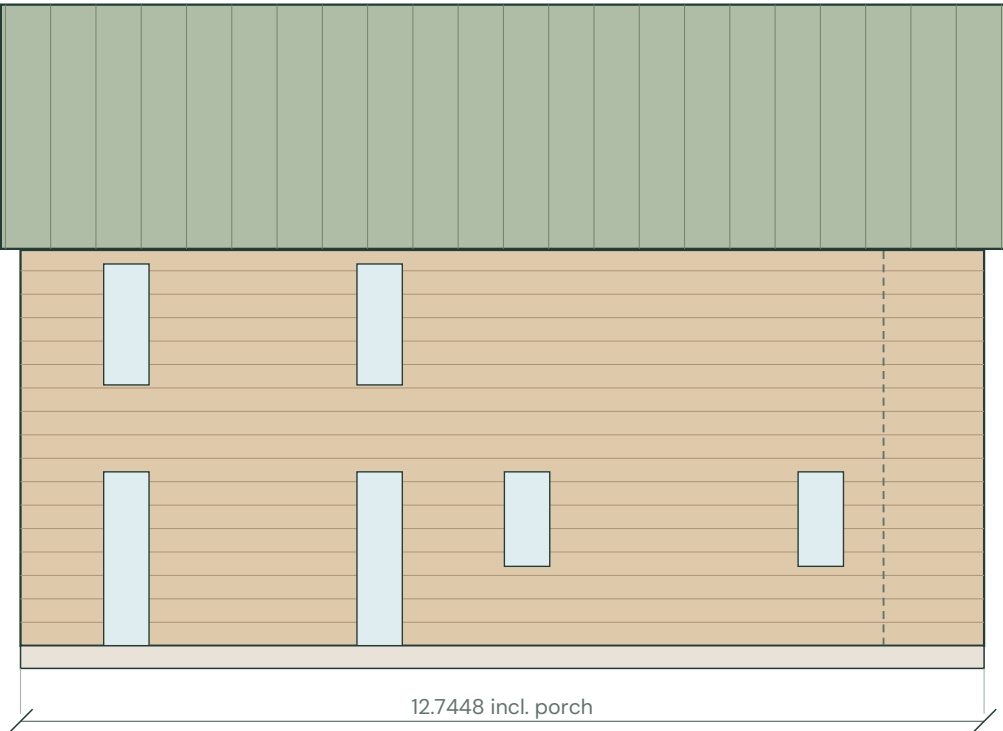


RIGHT ELEVATION

The wider design raises the ridge to retain the 30° pitch. Porch wings extend 1.330 m. All levels are relative to each house finished floor.


Roof plan / sage green metal

1:100. The roof and covered porch are additional to the enclosed floor area.

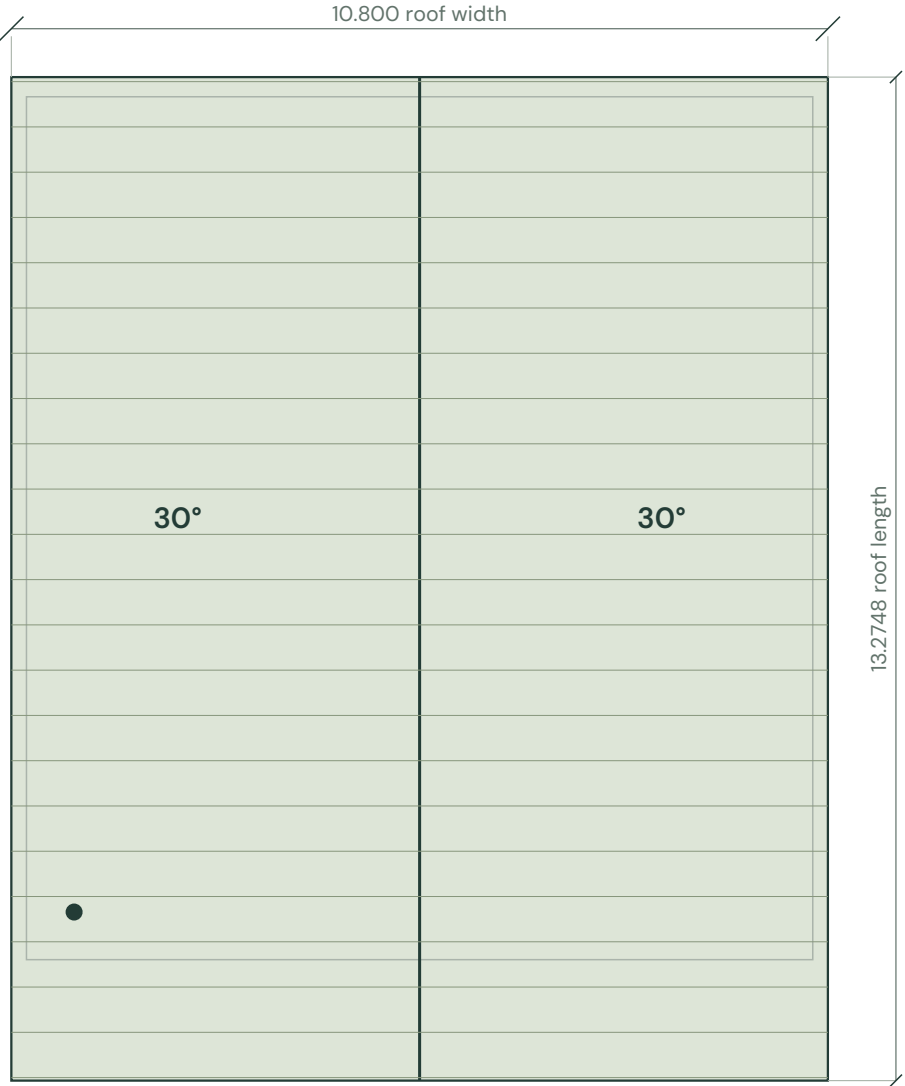


Longitudinal section / at the loft arrival

1:100. Glass retained toward the double-height living room.

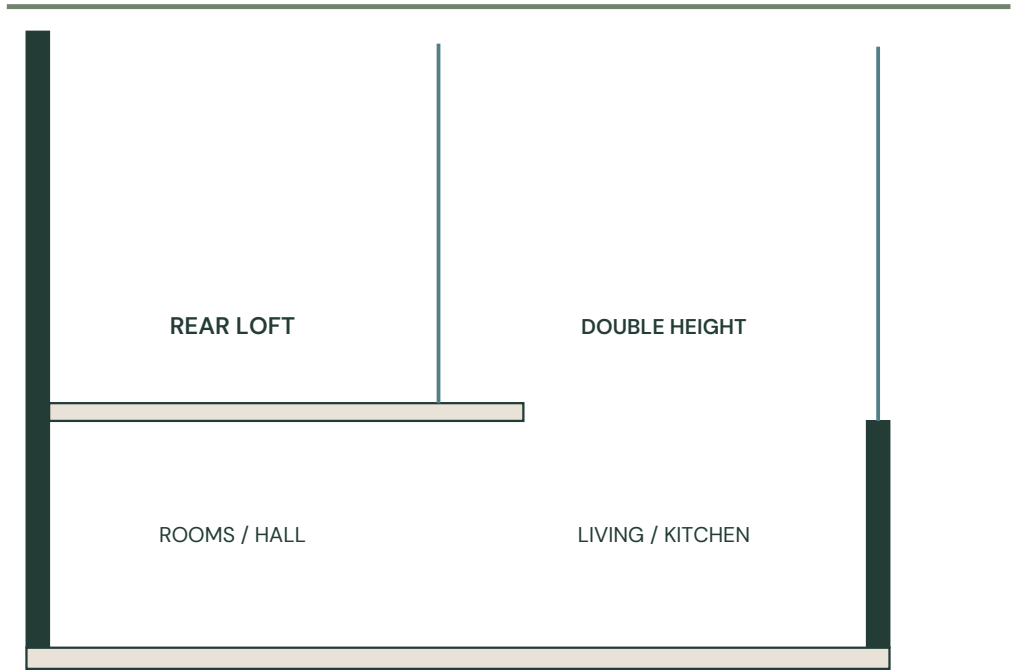

Transverse section / rear loft

1:50. Measured enclosure, full wall thicknesses and headroom bands.

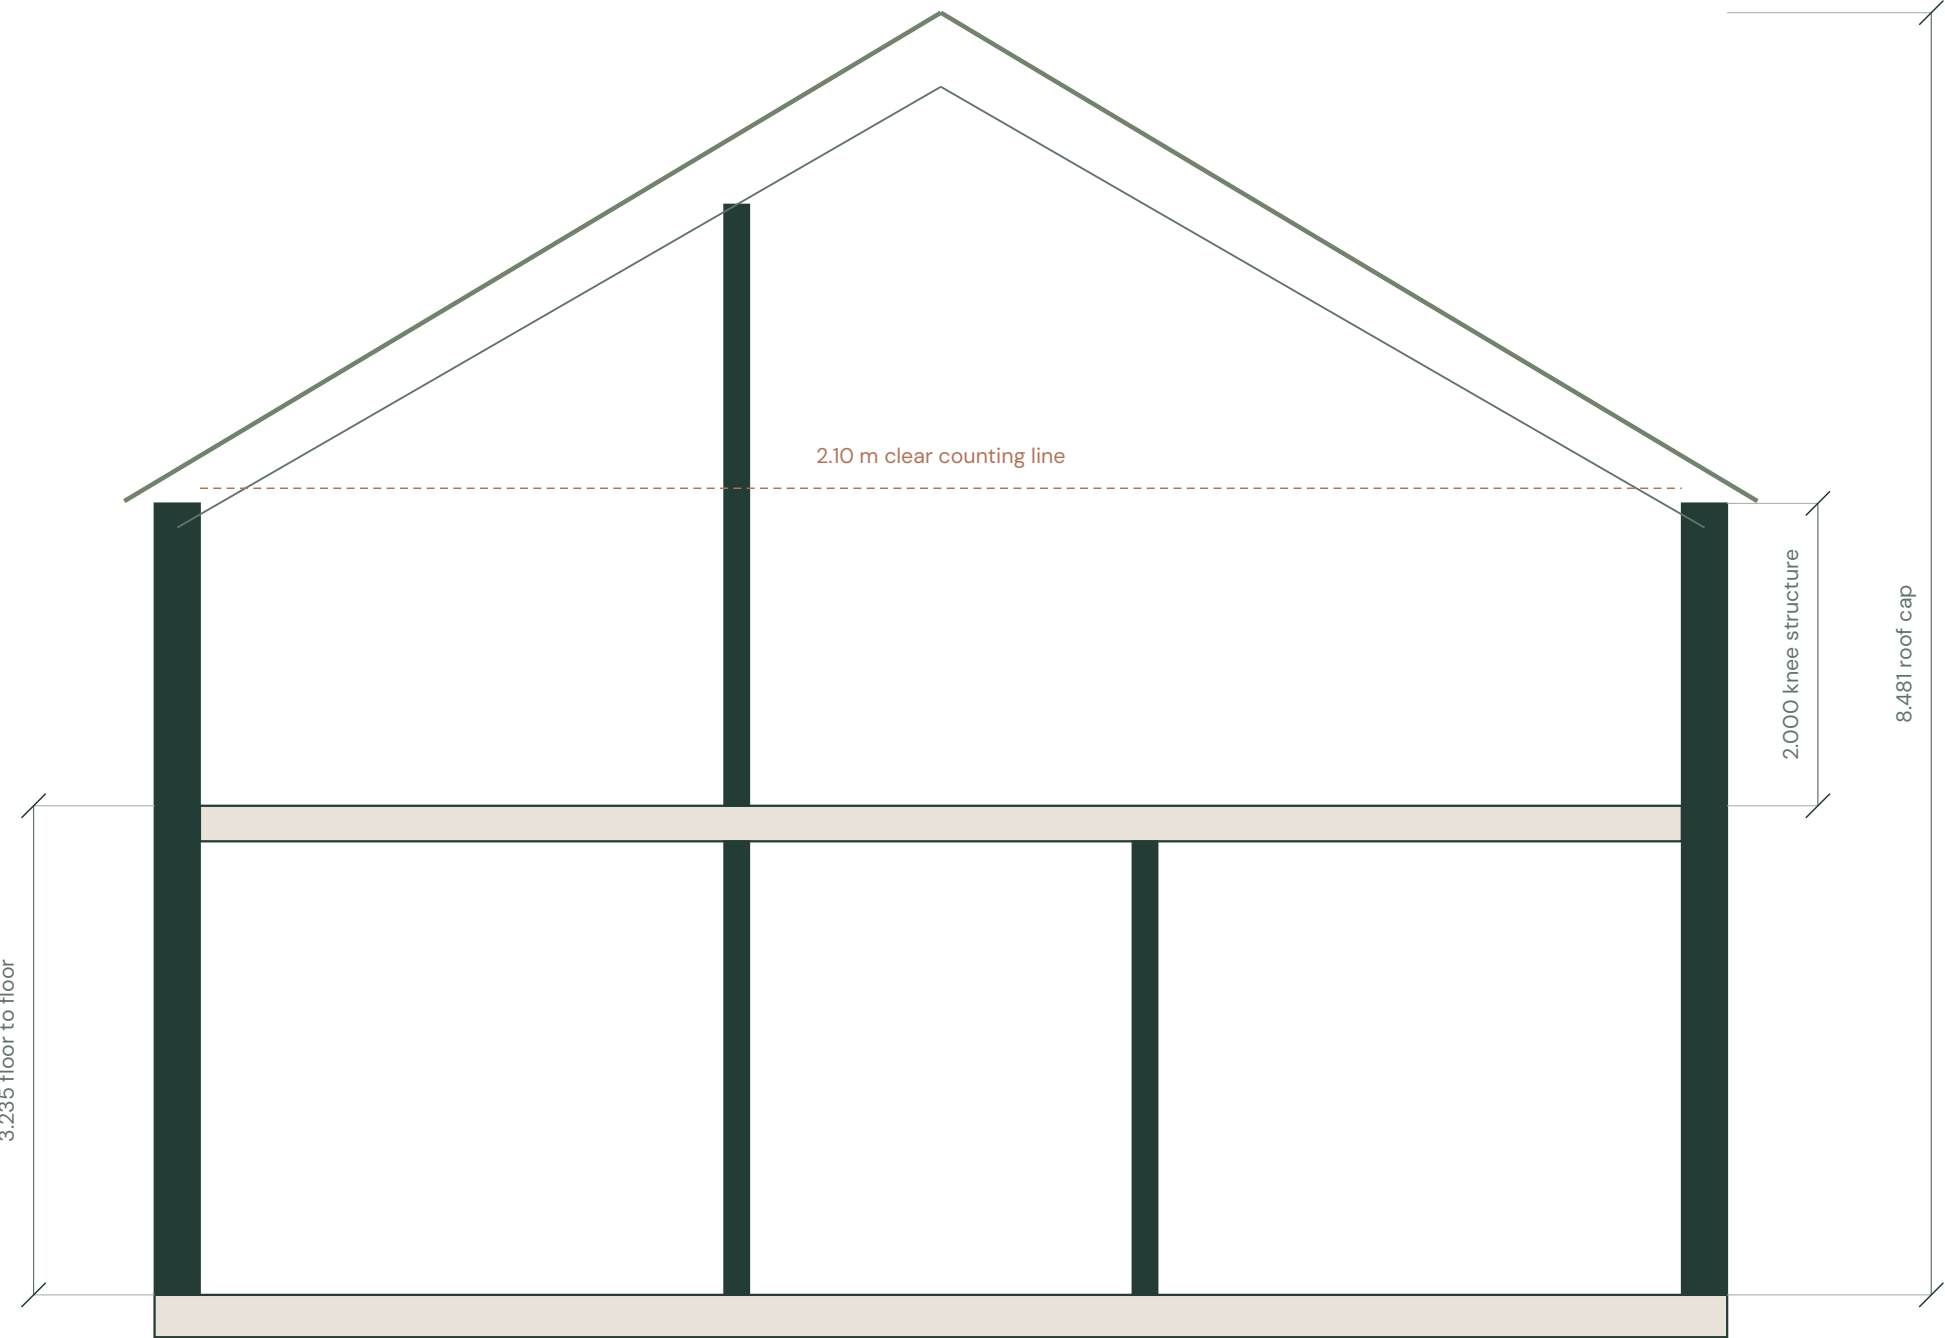

The roof underside controls the excluded low-headroom strips. External walls remain 300 mm; partitions remain 165 mm. Floor, roof and timber joints shown here are indicative assemblies for engineering coordination.

Roof cap is approximately 8.481 m above house FFL, or 8.781 m above its garden. Confirm the applicable height datum and limits with the appointed architect.

Usable area and placement register

All local coordinates are metres. Do not treat this model trace as a cadastral survey.

HOME	NAME	PLOT	CENTRE X	CENTRE Z	ROTATION	FFL	USABLE m²
P6-01	Olive	6	-34.5000	-39.1180	0.00°	+6.30	143.7
P6-02	Cypress	6	-18.5000	-39.1180	0.00°	+6.30	143.7
P6-03	Juniper	6	-2.5000	-39.1180	0.00°	+6.30	143.7
P5-01	Cedar	5	14.5000	-39.1180	0.00°	+6.30	143.7
P5-02	Laurel	5	29.5000	-39.1180	0.00°	+6.30	143.7
P5-03	Myrtle	5	44.5000	-39.1180	0.00°	+6.30	143.7
P3-01	Sage	3	-41.5000	-9.6180	0.00°	+3.30	143.7
P3-02	Rosemary	3	-24.3000	-9.6180	0.00°	+3.30	143.7
P4-01	Almond	4	-2.5000	-9.6180	0.00°	+3.30	143.7
P4-02	Fig	4	11.5000	-9.6180	0.00°	+3.30	143.7
P4-03	Pomegranate	4	25.5000	-9.6180	0.00°	+3.30	143.7
P1-01	Jasmine	1	-44.5233	30.7960	-9.60°	+0.30	143.7
P1-02	Lavender	1	-30.5233	33.0960	-9.60°	+0.30	143.7
P1-03	Iris	1	-17.0233	35.3960	-9.60°	+0.30	143.7
P2-01	Thyme	2	36.0000	19.1820	0.00°	+0.30	143.7
P2-02	Arbutus	2	21.5000	37.1820	0.00°	+0.30	143.7


PER HOME	OPEN	DRESSING
Ground usable	96.7121	96.7121
Loft usable	46.9879	46.9879
TOTAL USABLE	143.7	143.7
Gross enclosed floor*	177.458	178.929

Development usable total: 2,299.20 m². Smallest enclosed-house separation: 3.29 m. Smallest original plot-boundary clearance: 0.39 m. These gaps are geometric measurements, not evidence of permitted setbacks.

* Gross is an illustrative outside-face envelope including the landing. Usable area is not planning floor area. The historical binder records plot-6 density/coverage constraints; current rights and loft treatment need the appointed architect’s review.

The shared garden / space to come together

Pool, padel, café, gym and planted paths. Exterior landscaping is a concept proposal.

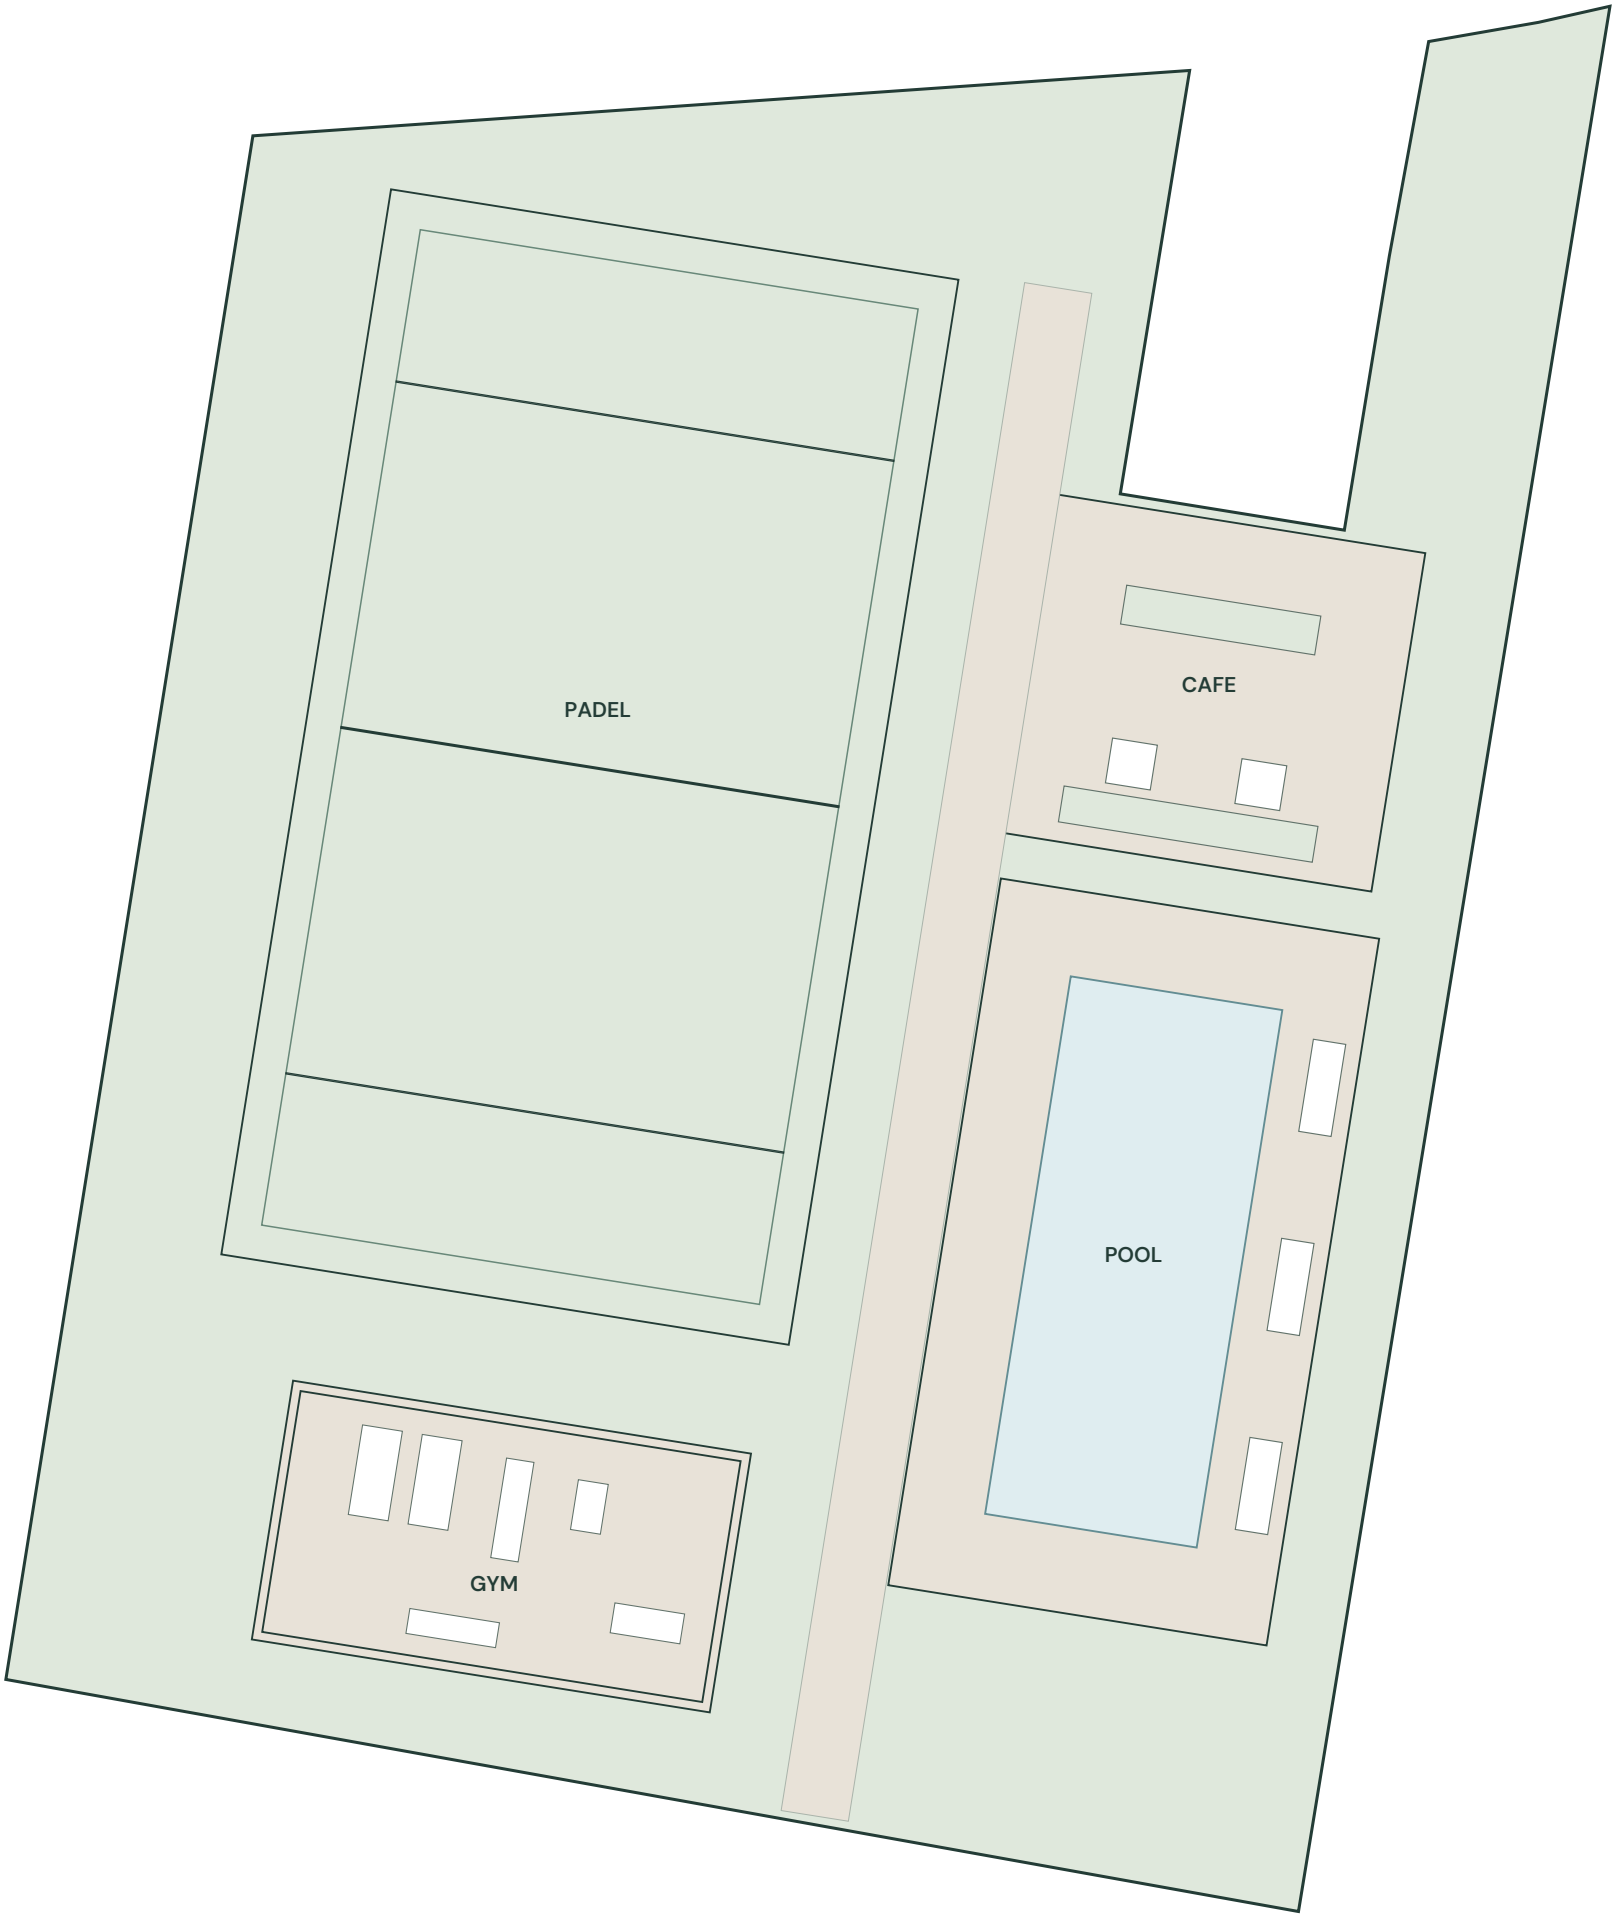

Development and coordination

- 01** Padel playing area: 10 x 20 m. Enclosure, access and compact surrounds are concept layouts. Pool water surface: 4.25 x 10.80 m. Gym pavilion: 9.20 x 5.20 m.
- 02** Thirty-centimetre external timber walls are kept full size in both models. Structural spruce grade, connections, fire performance, insulation, moisture control and foundations require engineering.
- 03** The nominal 2.10 m loft counting threshold follows the shared roof underside. Floor finishes, roof build-up, stair headroom and opening details need a coordinated construction design.
- 04** Private gardens have perimeter walls, a parking bay and a garden kitchen. Boundary walls and retaining sections require drainage and structural design. The larger option has compact rear patios in the tightest parcels.
- 05** Street, garden and common-area fixtures illuminate at dusk/night in the model. Positions are indicative; electrical, glare and access requirements remain to be designed.
- 06** Source basis: manufacturer hand drawing, architect binder, subdivision overview and the owner’s revised placement and landscape instructions. Refer to the Info folder for source material.
- 07** North, plot edges, levels and roads follow the digitized model trace. A fresh measured survey and appointed architect review are required before setting out.

