

# 95 m². Room to live.

Sixteen spruce glulam homes, developed from the manufacturer’s roof and glazing concept. A coordinated architectural study for your appointed architect, matching the selected interactive model.

16

HOMES

95

USABLE m² / HOME

1,520.0

DEVELOPMENT m²

### A measured design, with choices

- 01

Outside enclosure 9.400 x 8.6639 m. Ground usable 62.7208 m² plus loft 32.2792 m². Both master arrangements total 95 m².
- 02

The wider option uses the established right wall as its datum; private divisions are adjusted to keep garden access. The minimum measured separation between enclosed house faces is 4.29 m. House setting-out points and rotations stay fixed.
- 03

Two downstairs rooms each measure 3.1175 x 3.8675 m. Bedroom, dining and library options share the same shell.
- 04

The dressing loft front and stair/landing move forward 127.95 mm to compensate for the extra partitions. Both layouts retain glass toward the living room.
- 05

Usable area excludes wall/door-reveal bands, ground stair reservation, upper void and loft floor below 2.10 m clear headroom. Fixed cabinetry is included.

### Drawing register

| SHEET | DRAWING                                  | SCALE        |
|-------|------------------------------------------|--------------|
| A000  | Design brief and drawing register        | NTS          |
| A001  | Overall site arrangement                 | 1:500        |
| A101  | Upper terrace   plots 5 and 6            | 1:250        |
| A102  | Middle terrace   plots 3 and 4           | 1:250        |
| A103  | Lower terrace   plots 1 and 2            | 1:250        |
| A201  | Dimensioned ground floor                 | 1:50         |
| A202  | Both master-suite arrangements           | 1:50         |
| A203  | Three lower-left room options            | 1:25         |
| A301  | Four external elevations                 | 1:100        |
| A302  | Roof plan and building sections          | 1:100 / 1:50 |
| A401  | Area and placement schedules             | NTS          |
| A402  | Shared amenities and design coordination | 1:150        |

#### CONCEPT CO4 / ARCHITECT REVIEW

Shared dimensions match the CO4 website model. This set does not establish permit rights, legal setbacks or construction details. Plot trace and terrace levels are provisional. Structural, services, drainage, fire and energy designs require appointed consultants.

Do not set out from rounded dimensions. The metre-based CAD and area audit retain full precision.

Overall arrangement / 16 homes of 95 m²

Existing setting-out points and orientations retained. Perimeter divisions, private gardens and shared green area.



| PLOT | HOMES | USABLE m² |
|------|-------|-----------|
| 6    | 3     | 285.0     |
| 5    | 3     | 285.0     |
| 4    | 3     | 285.0     |
| 3    | 2     | 190.0     |
| 1    | 3     | 285.0     |
| 2    | 2     | 190.0     |

- 01 Upper plots 5/6: +6.00 m. Middle plots 3/4: +3.00 m. Lower plots 1/2: +0.00 m. House finished floors +0.30 m above terrace; relative levels only.
- 02 Only the two source road corridors are shown. Parking access meets the road edge; no extra internal street is introduced.
- 03 Rear gardens on plots 1, 3 and 4; left garden at Thyme and right garden at Arbutus. Larger homes require more compact terraces.
- 04 Private divisions are landscape proposals, not cadastral boundaries. Gate locations and retaining walls need measured survey coordination.

Upper terrace / homes, gardens and arrivals


95 m² usable per home. Enclosed footprint 9.400 x 8.6639 m; porch additional.



| HOME  | NAME    | FFL   | GARDEN | PLOT GAP* | PARCEL GAP* |
|-------|---------|-------|--------|-----------|-------------|
| P6-01 | Olive   | +6.30 | front  | 3.58      | 3.58        |
| P6-02 | Cypress | +6.30 | front  | 6.43      | 2.40        |
| P6-03 | Juniper | +6.30 | front  | 4.23      | 2.40        |
| P5-01 | Cedar   | +6.30 | front  | 3.36      | 3.36        |
| P5-02 | Laurel  | +6.30 | front  | 6.57      | 1.90        |
| P5-03 | Myrtle  | +6.30 | front  | 6.67      | 1.90        |

\* Shortest enclosed-face distance to the plot or private division. These are measured model clearances, not approved setbacks. Roof overhangs and wall construction require separate review.

Every home retains a 2.70 x 5.20 m parking bay and direct road connection. Gate fabrication is not defined.

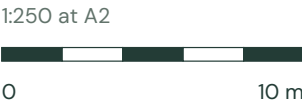



Middle terrace / homes, gardens and arrivals


95 m² usable per home. Enclosed footprint 9.400 x 8.6639 m; porch additional.



| HOME  | NAME        | FFL   | GARDEN | PLOT GAP* | PARCEL GAP* |
|-------|-------------|-------|--------|-----------|-------------|
| P3-01 | Sage        | +3.30 | rear   | 4.47      | 3.90        |
| P3-02 | Rosemary    | +3.30 | rear   | 6.02      | 3.90        |
| P4-01 | Almond      | +3.30 | rear   | 2.97      | 2.30        |
| P4-02 | Fig         | +3.30 | rear   | 6.07      | 2.30        |
| P4-03 | Pomegranate | +3.30 | rear   | 3.99      | 2.30        |

\* Shortest enclosed-face distance to the plot or private division. These are measured model clearances, not approved setbacks. Roof overhangs and wall construction require separate review.

Every home retains a 2.70 x 5.20 m parking bay and direct road connection. Gate fabrication is not defined.

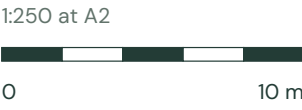

Lower terrace / homes, gardens and arrivals


95 m² usable per home. Enclosed footprint 9.400 x 8.6639 m; porch additional.



| HOME  | NAME     | FFL   | GARDEN | PLOT GAP* | PARCEL GAP* |
|-------|----------|-------|--------|-----------|-------------|
| P1-01 | Jasmine  | +0.30 | rear   | 2.99      | 2.39        |
| P1-02 | Lavender | +0.30 | rear   | 7.04      | 2.15        |
| P1-03 | Iris     | +0.30 | rear   | 0.40      | 0.40        |
| P2-01 | Thyme    | +0.30 | left   | 3.09      | 3.09        |
| P2-02 | Arbutus  | +0.30 | right  | 1.73      | 1.73        |


\* Shortest enclosed-face distance to the plot or private division. These are measured model clearances, not approved setbacks. Roof overhangs and wall construction require separate review.

Every home retains a 2.70 x 5.20 m parking bay and direct road connection. Gate fabrication is not defined.

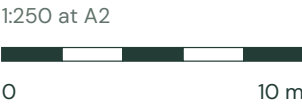

Ground floor / furnished arrangement

62.7208 m² counted usable. All three left-room options use this enclosure.

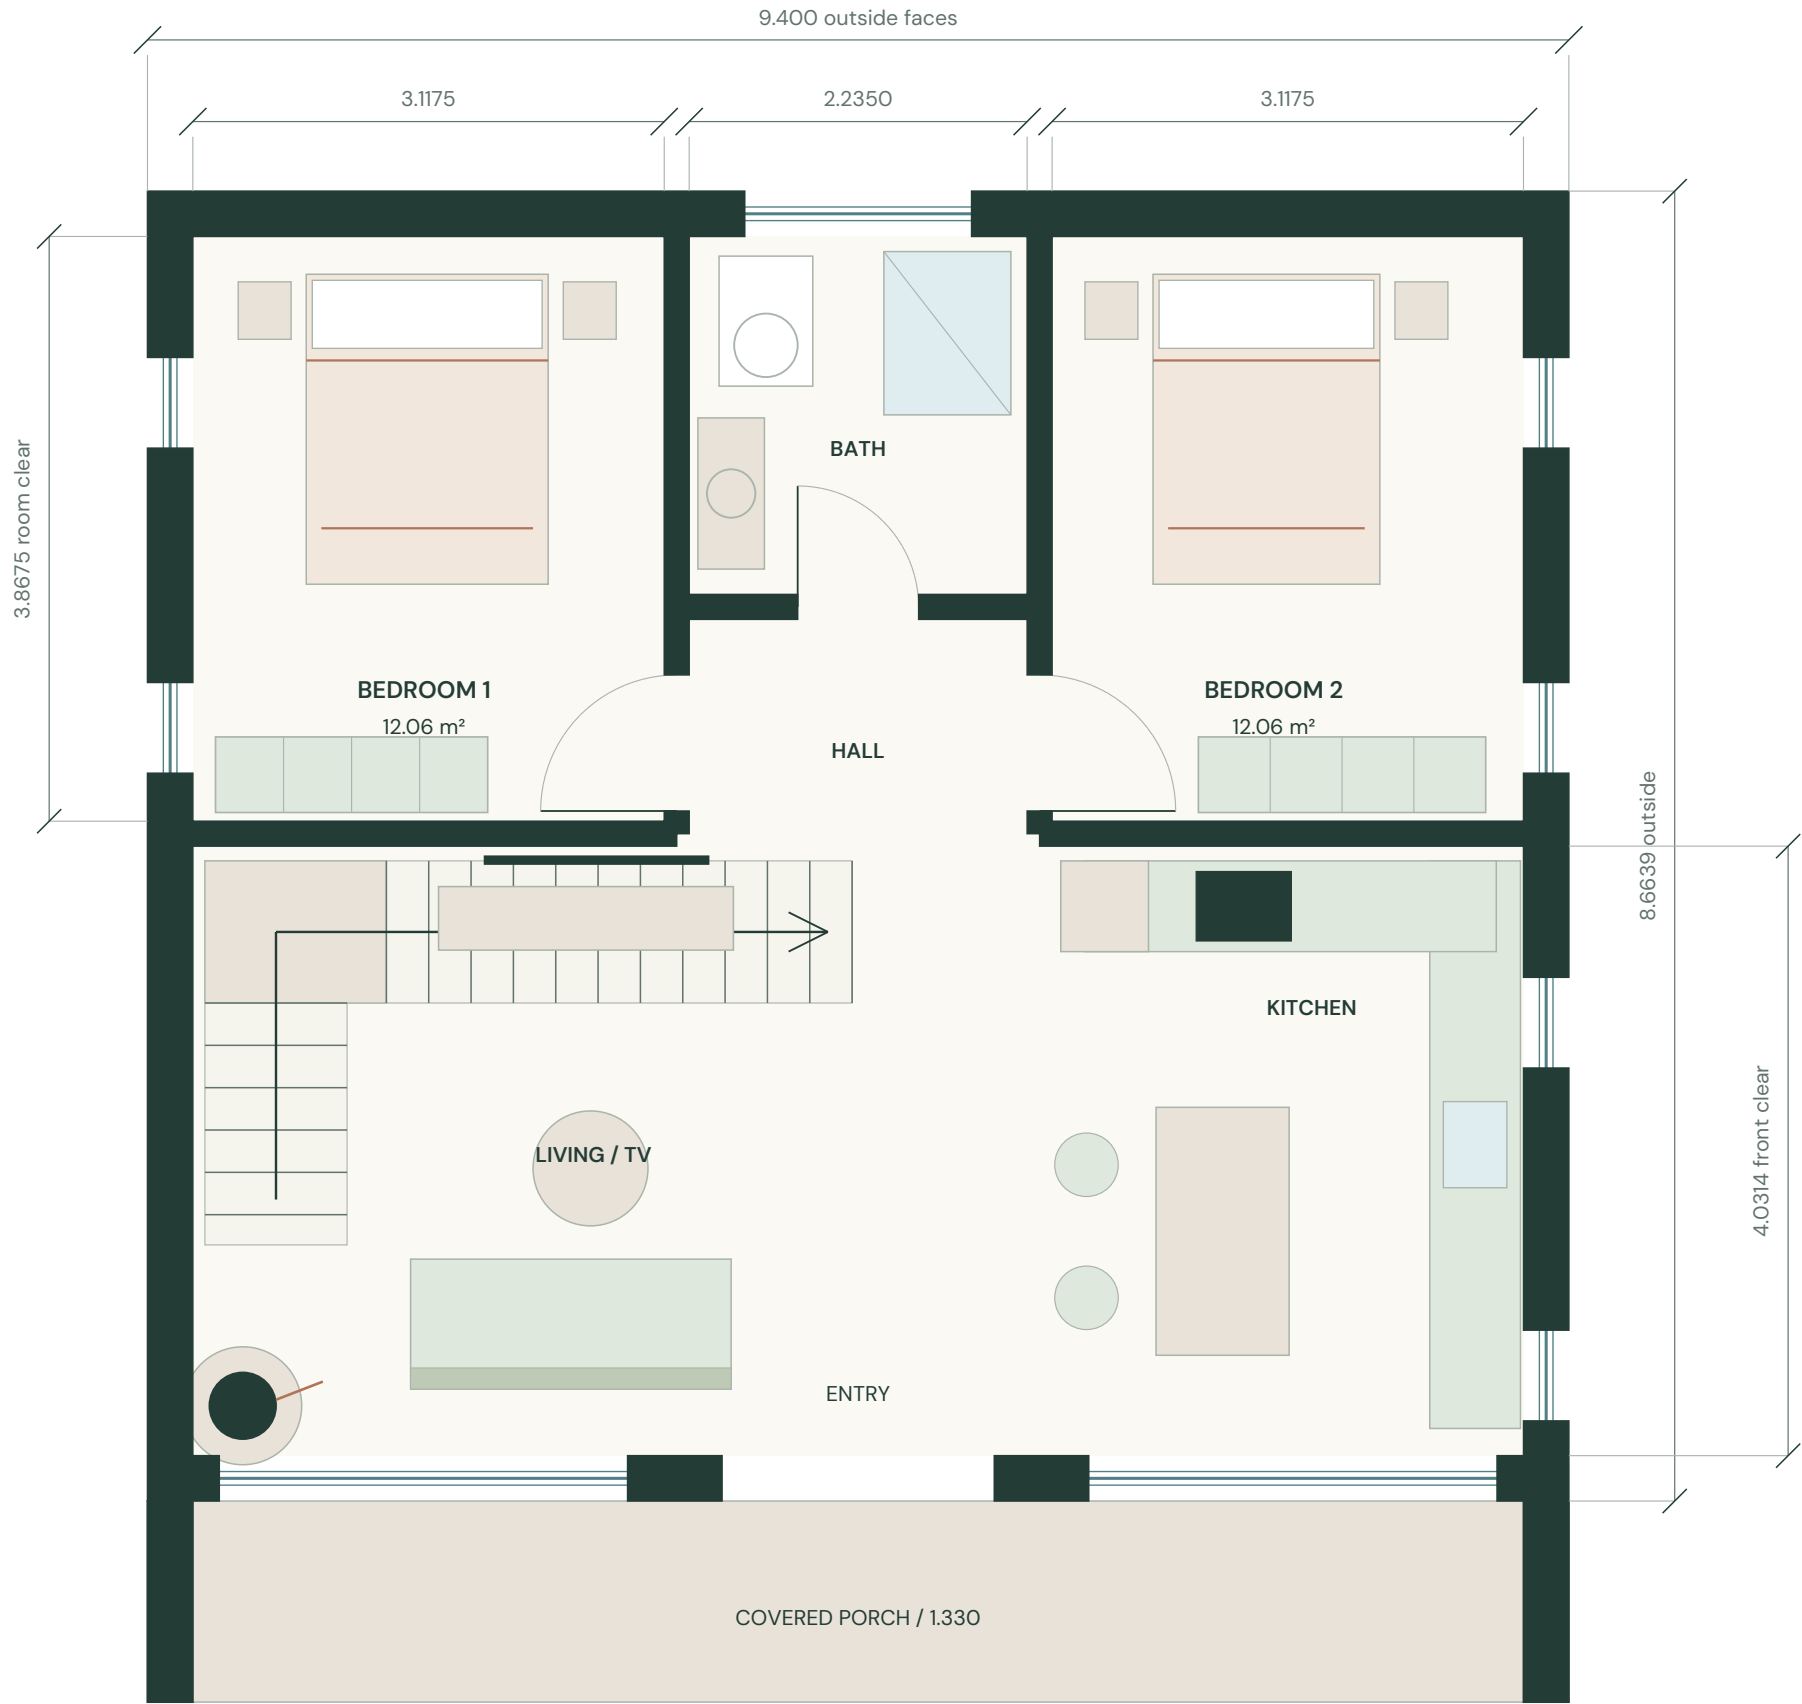

Space for everyday life

| GROUND FLOOR                   | AREA m² |
|--------------------------------|---------|
| Inside external walls          | 70.9627 |
| Less full partition bands      | 2.7147  |
| Less stair / guard reservation | 5.5272  |
| USABLE GROUND FLOOR            | 62.7208 |

- 01** Each rear room: 12.0569 m² clear before furnishings. Central bath: 2.235 x 2.3675 m clear between finished walls. External walls 300 mm; internal wall bands 165 mm.
- 02** Living seating faces the wall-backed screen below the stair. The sealed corner stove faces the sofa. Kitchen island and counters are independently sized.
- 03** Stair concept: 18 equal rises over 3.235 m (179.72 mm). Lower goings 280 mm; upper goings 280.00 mm. Clear flight 940 mm; upper landing 1.160 x 1.040 m. Verify structure, handrails and headroom.
- 04** This ground plan shows the open-suite stair position. With the dressing loft, the stair reservation moves 127.95 mm toward the front; usable area is unchanged.
- 05** 1.330 m clear sheltered porch between the extended side walls. The open porch is excluded from usable and enclosed floor area.


Furniture is a coordinated interior concept, not a joinery specification. The central entry, hall and sliding loft arrival are kept clear.






A / Open master suite

Bathroom partition with open clothes storage; retained glazed frontage.

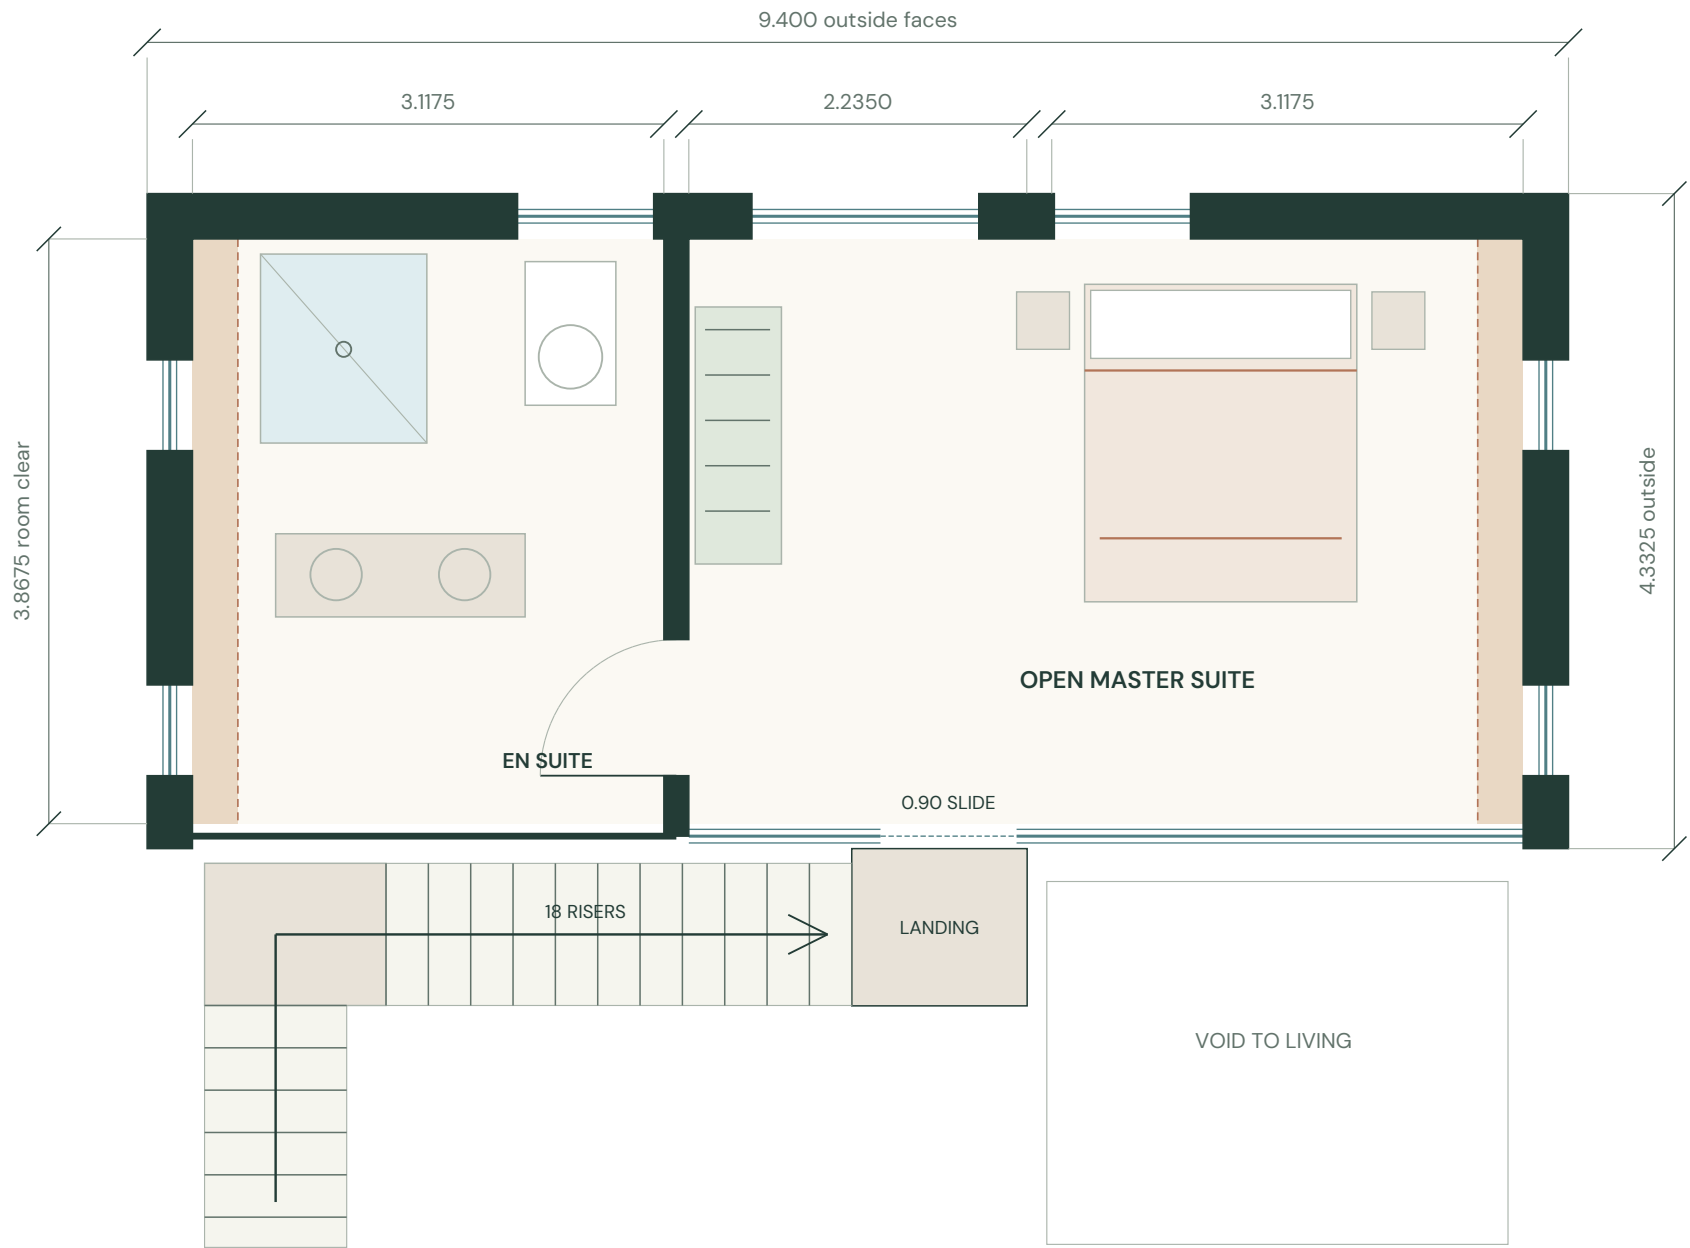

B / Walk-in wardrobe suite

Glazed frontage and landing advance 127.95 mm.

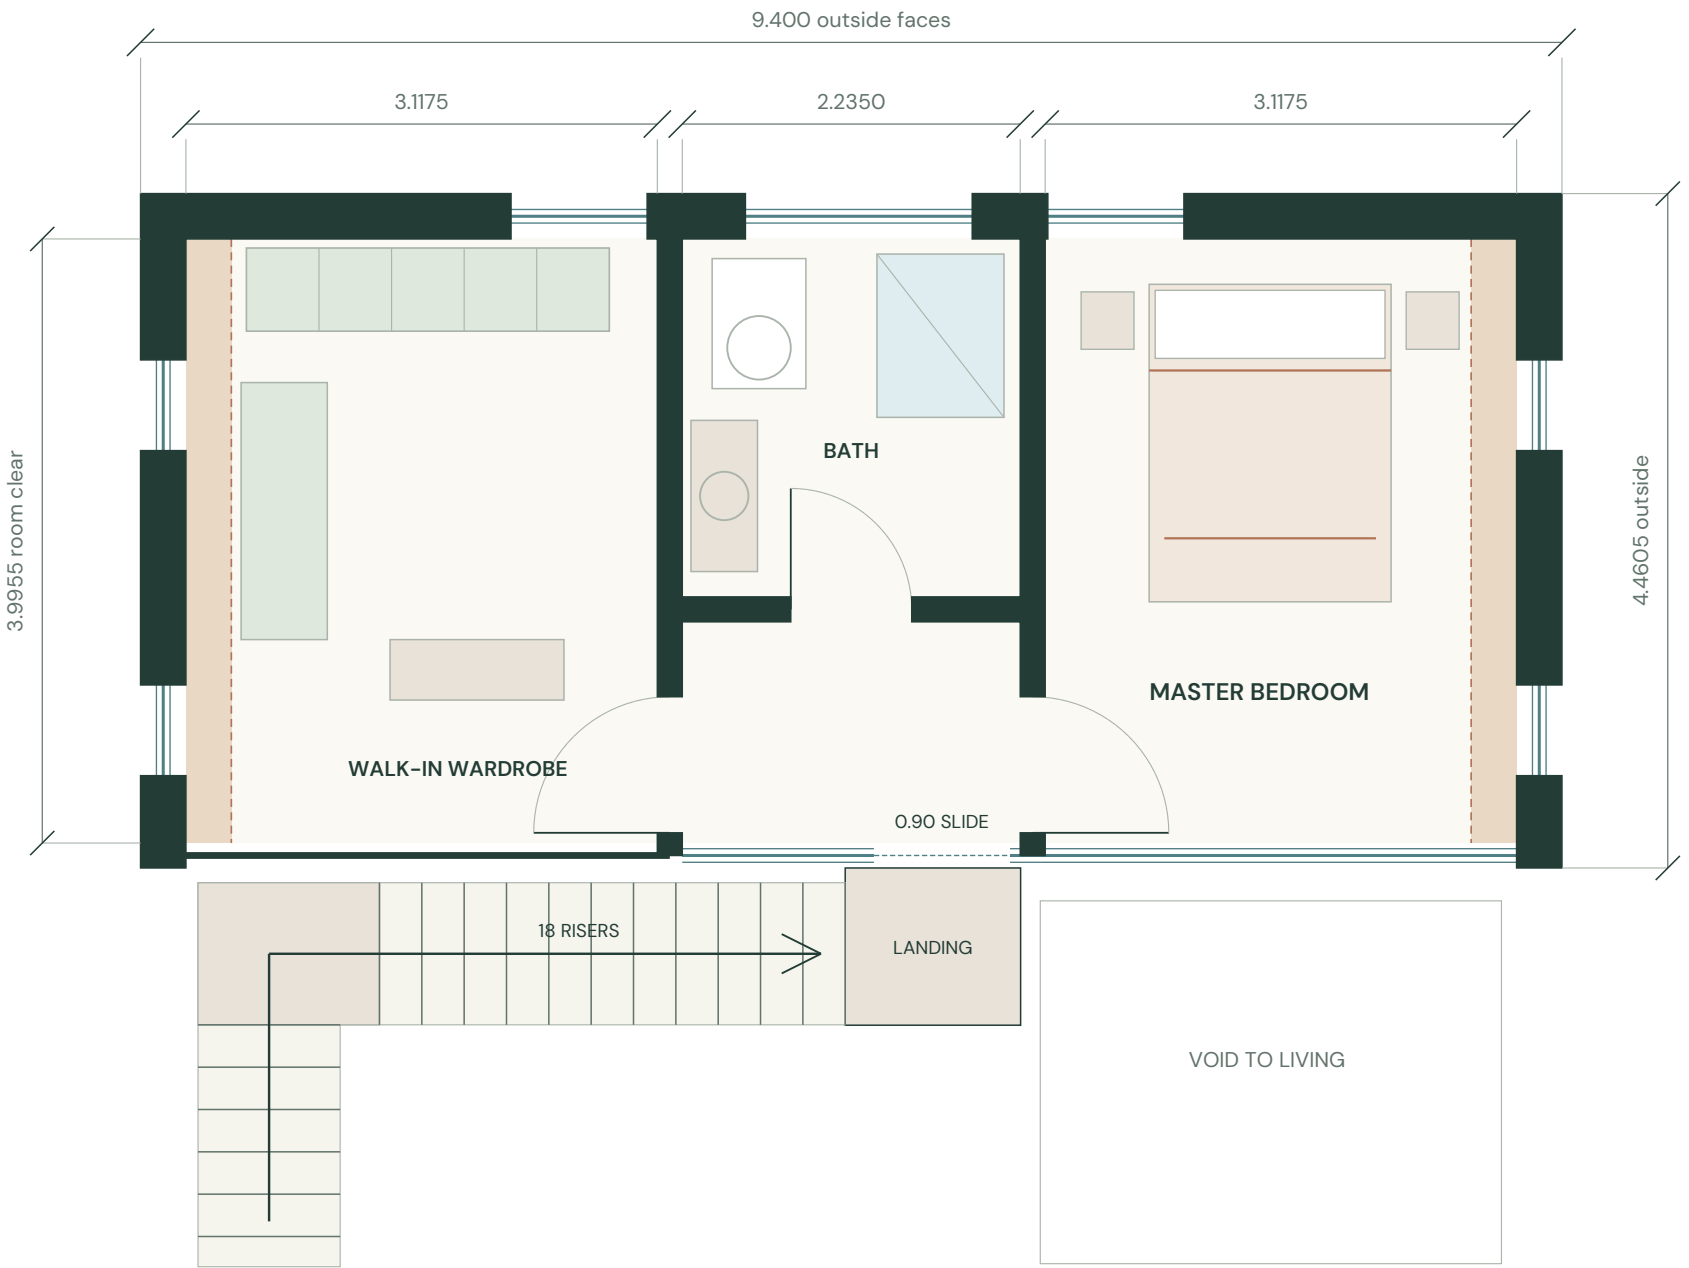

| COUNTING METHOD         | OPEN    | DRESSING |
|-------------------------|---------|----------|
| Clear room floor        | 33.3959 | 33.4727  |
| Below 2.10 m (excluded) | 2.3231  | 2.3999   |
| Landing included        | 1.2064  | 1.2064   |
| USABLE LOFT             | 32.2792 | 32.2792  |


Ochre bands identify the low-headroom floor excluded from usable area. The threshold is a project counting assumption, not a statement of statutory habitable-room compliance. Cabinetry in these strips stays under the roof.

Both loft choices plus the ground floor total 95 m². The 0.90 m sliding entrance aligns with the landing.

The lower-left room / three ways to live


Identical finished dimensions: 3.1175 x 3.8675 m. Each option: 12.0569 m².

O1 / BEDROOM

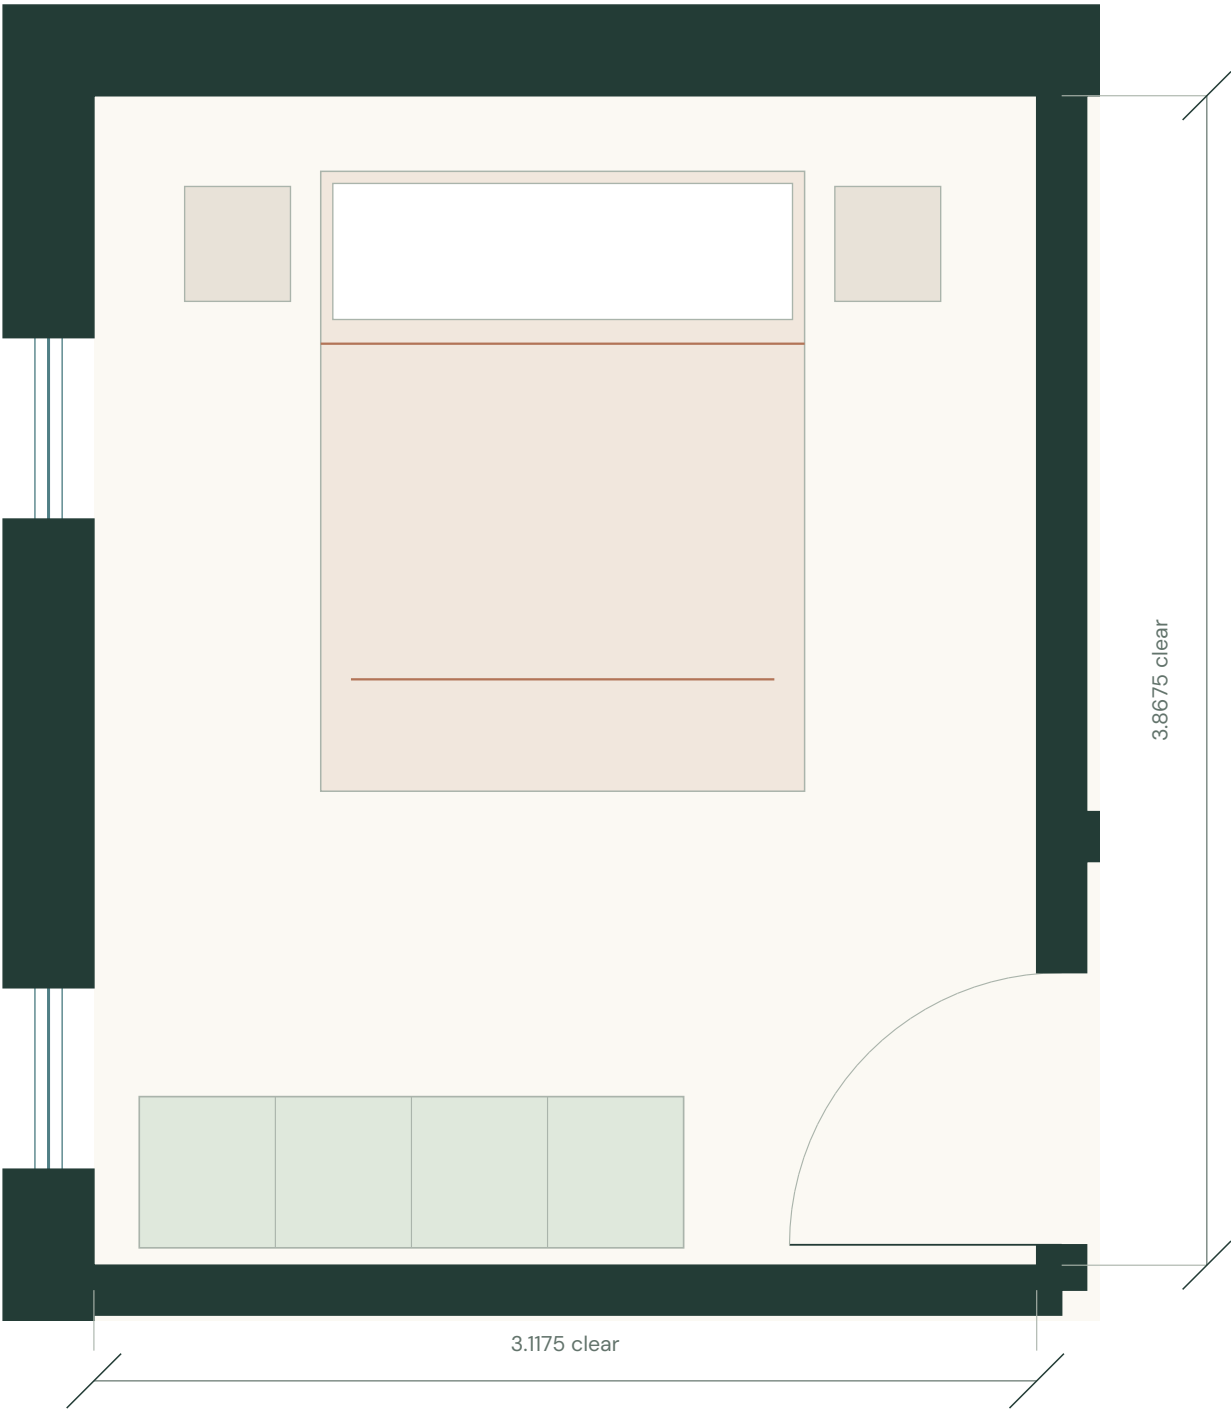


1.60 x 2.05 m bed; two bedside tables and 1.80 m wardrobe.

O2 / ROUND DINING

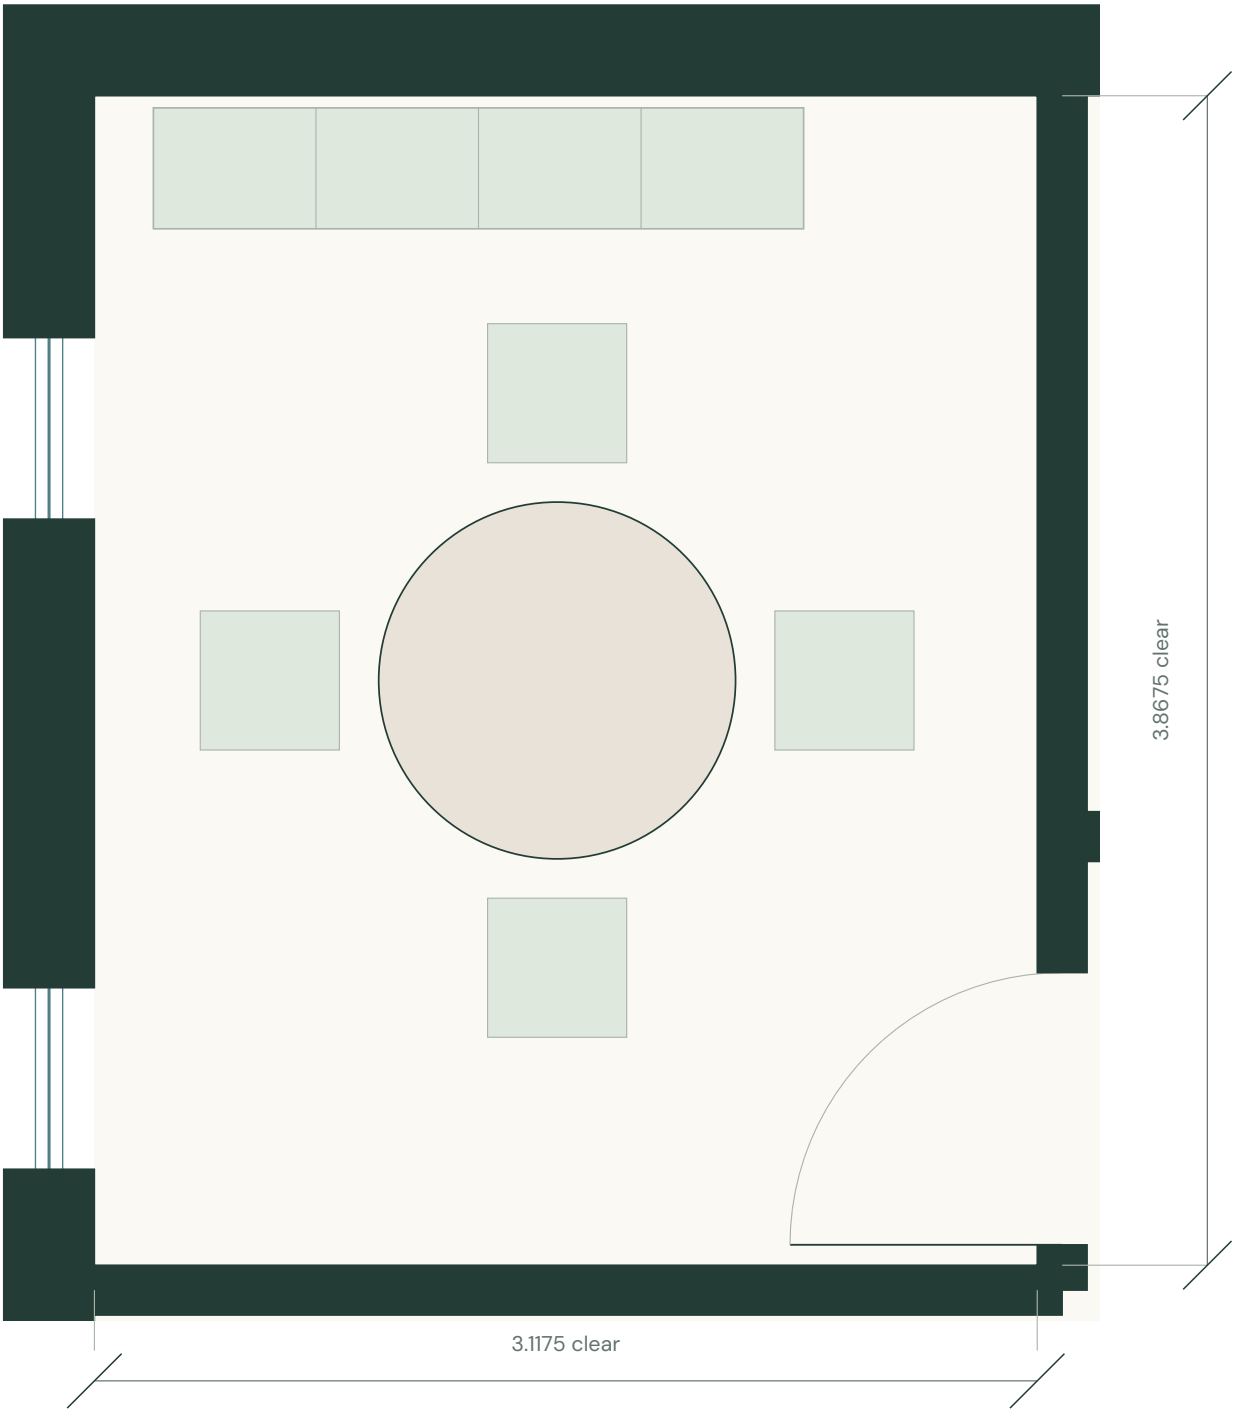

Four chairs around a 1.18 m diameter table; shallow rear sideboard.

O3 / LIBRARY + DESK

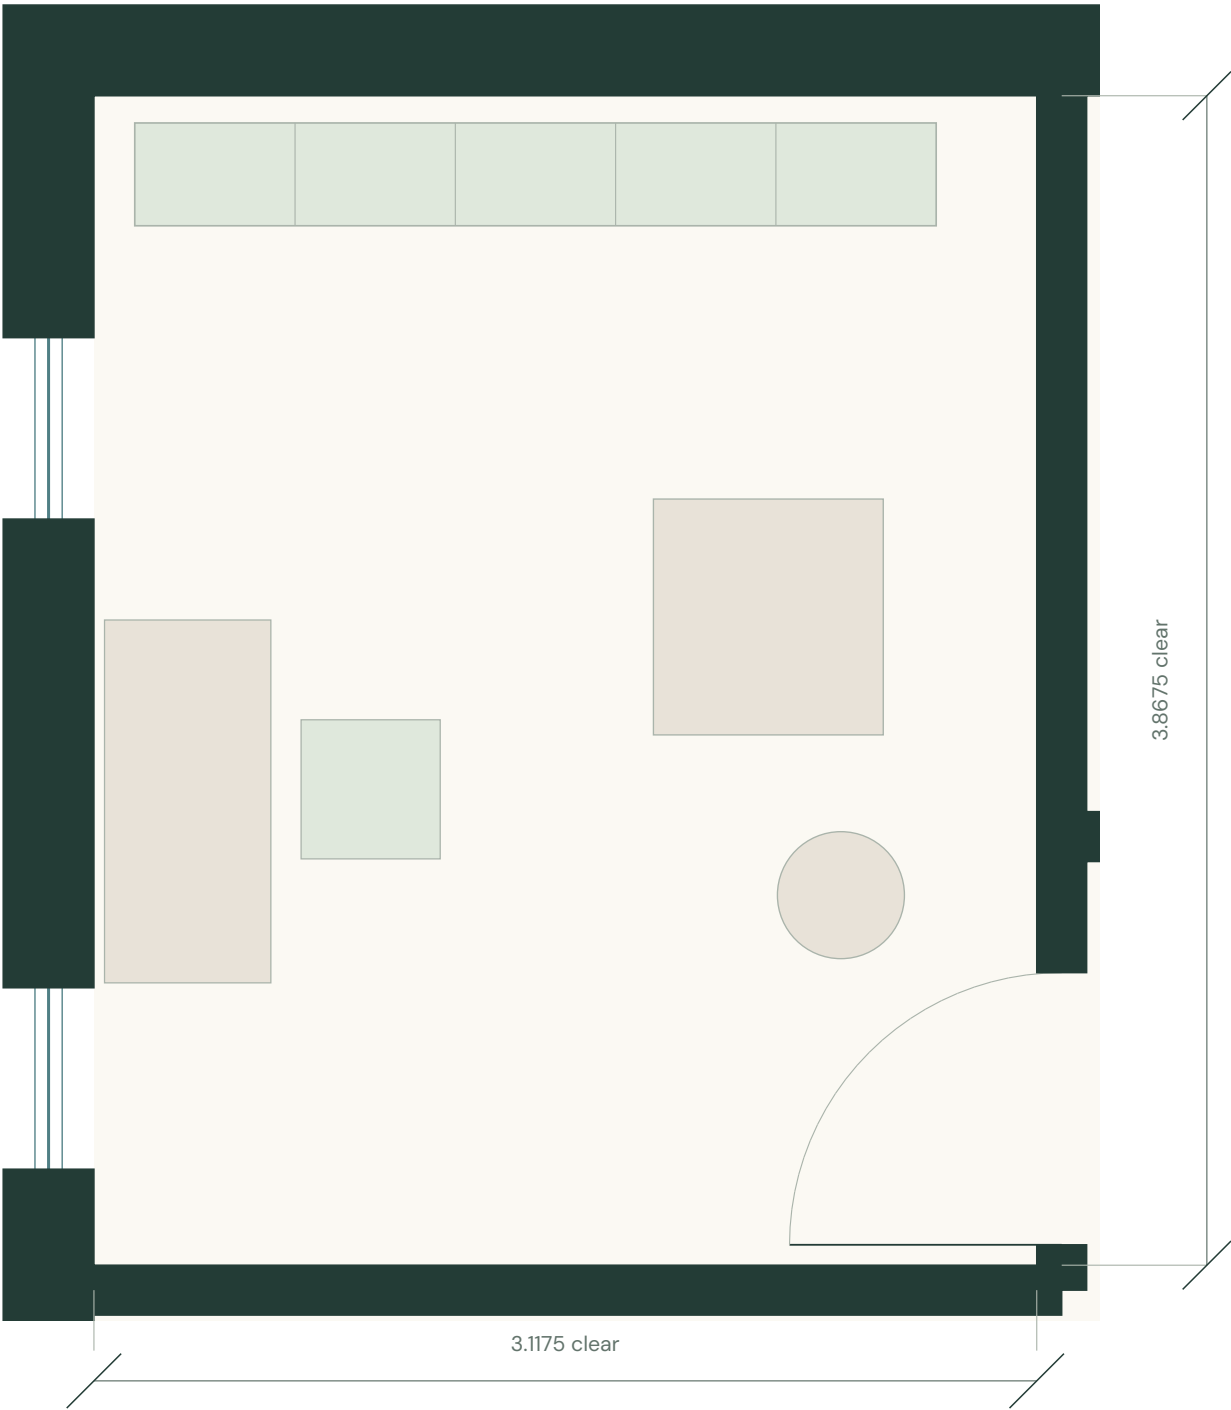

Oak bookshelves, writing desk, upholstered reading chair and side lamp.



Elevations / warm spruce and sage roofs

Horizontal timber courses, sage green standing-seam metal and sheltered porches.




FRONT ELEVATION

Roof pitch 30°. Loft FFL +3.235 m. Knee structure +5.235 m. Ridge structure +7.862 m. Approximate roof cap +8.192 m above FFL.




REAR ELEVATION

Roof pitch 30°. Loft FFL +3.235 m. Knee structure +5.235 m. Ridge structure +7.862 m. Approximate roof cap +8.192 m above FFL.

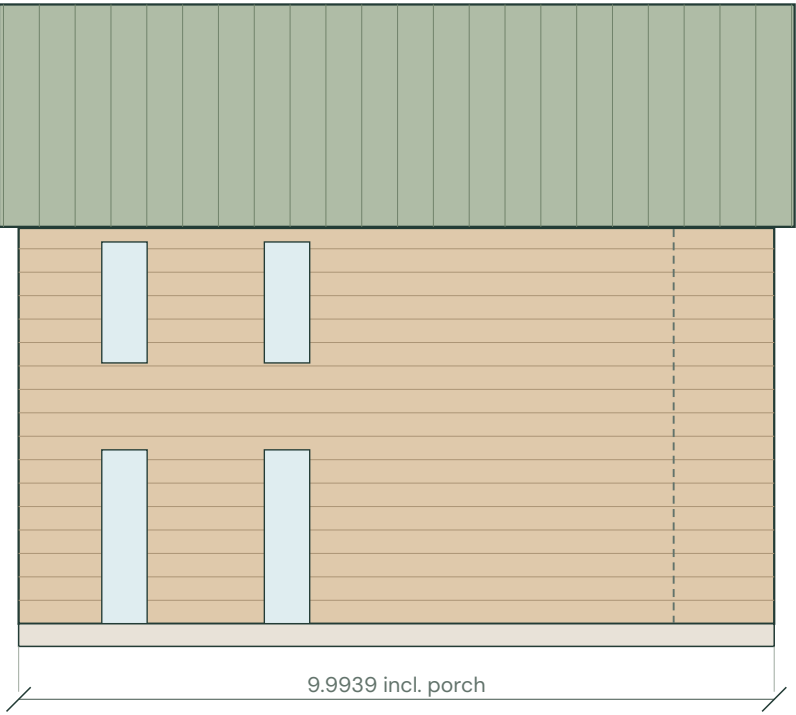

LEFT ELEVATION

The wider design raises the ridge to retain the 30° pitch. Porch wings extend 1.330 m. All levels are relative to each house finished floor.

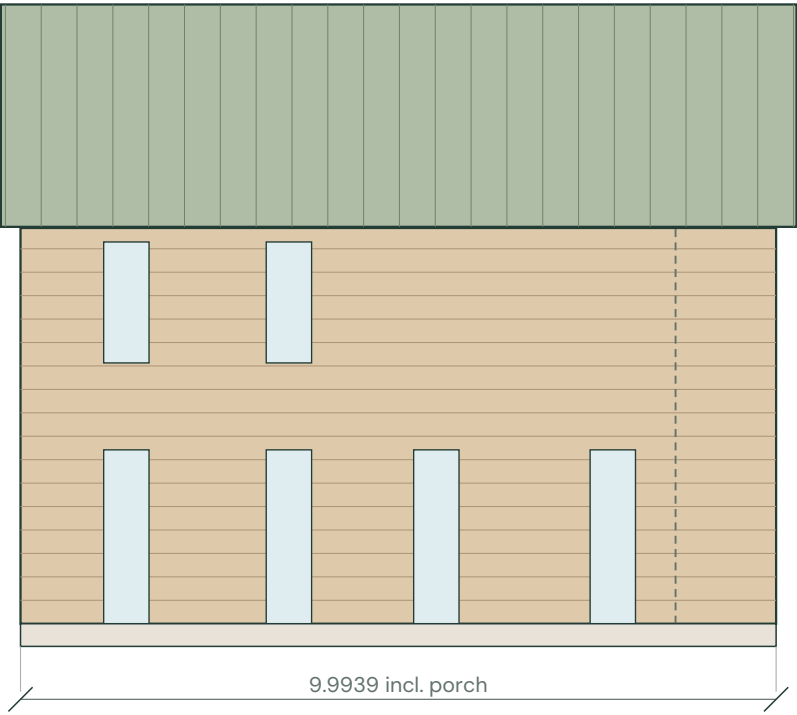


RIGHT ELEVATION

The wider design raises the ridge to retain the 30° pitch. Porch wings extend 1.330 m. All levels are relative to each house finished floor.


Roof plan / sage green metal

1:100. The roof and covered porch are additional to the enclosed floor area.

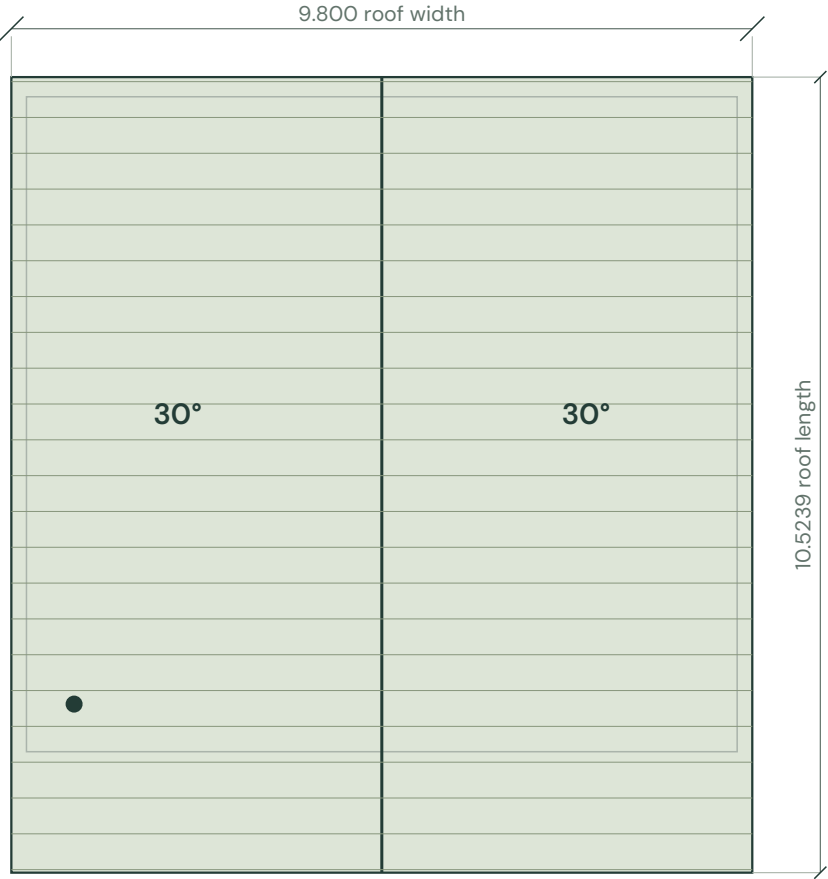


Longitudinal section / at the loft arrival

1:100. Glass retained toward the double-height living room.

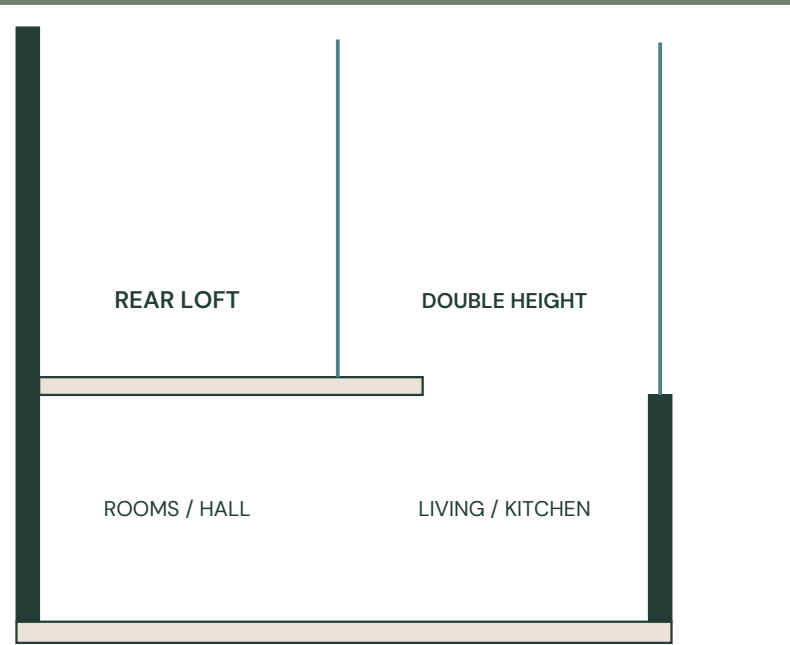

Transverse section / rear loft

1:50. Measured enclosure, full wall thicknesses and headroom bands.

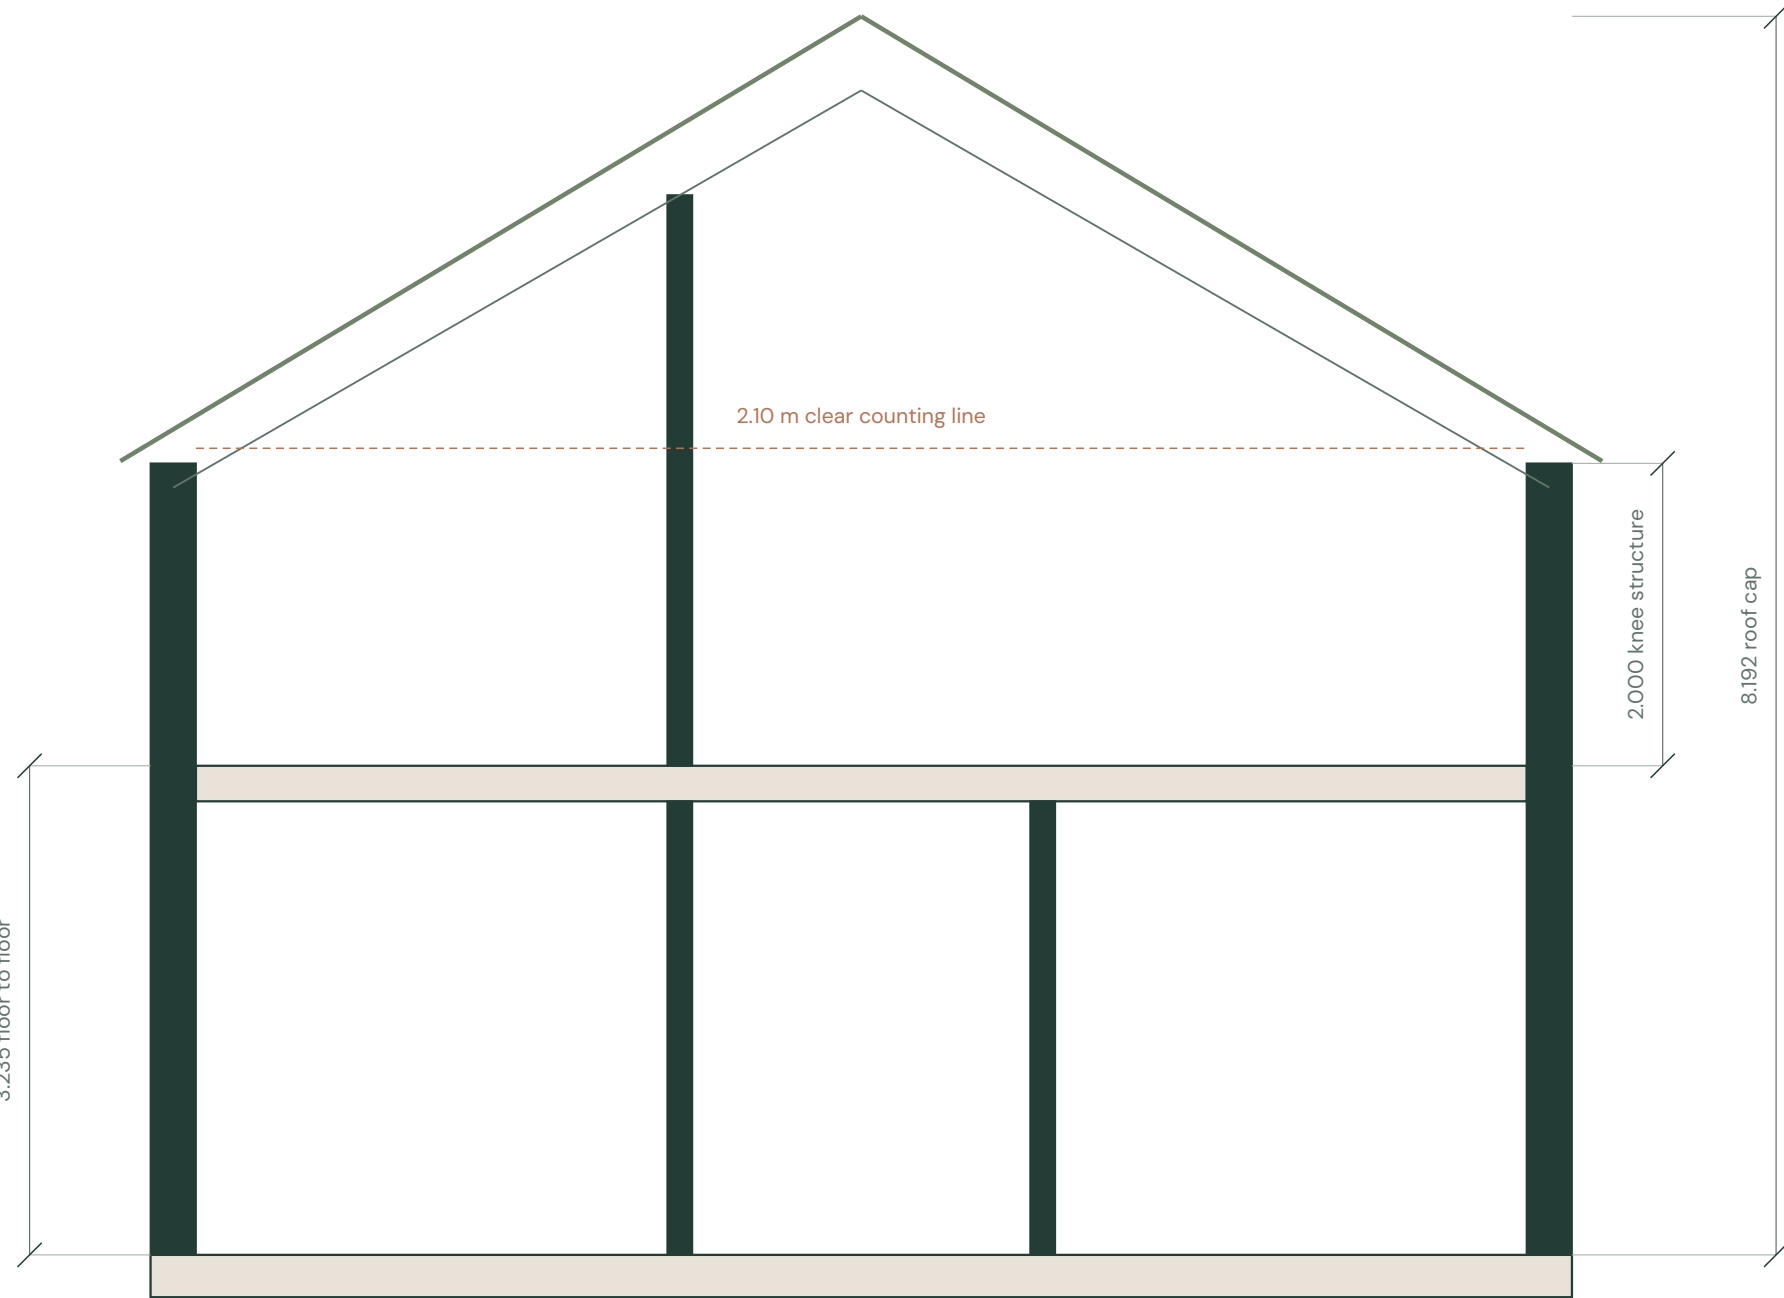

The roof underside controls the excluded low-headroom strips. External walls remain 300 mm; partitions remain 165 mm. Floor, roof and timber joints shown here are indicative assemblies for engineering coordination.

Roof cap is approximately 8.192 m above house FFL, or 8.492 m above its garden. Confirm the applicable height datum and limits with the appointed architect.

Usable area and placement register

All local coordinates are metres. Do not treat this model trace as a cadastral survey.

| HOME  | NAME        | PLOT | CENTRE X | CENTRE Z | ROTATION | FFL   | USABLE m² |
|-------|-------------|------|----------|----------|----------|-------|-----------|
| P6-01 | Olive       | 6    | -34.0000 | -39.1180 | 0.00°    | +6.30 | 95        |
| P6-02 | Cypress     | 6    | -18.0000 | -39.1180 | 0.00°    | +6.30 | 95        |
| P6-03 | Juniper     | 6    | -2.0000  | -39.1180 | 0.00°    | +6.30 | 95        |
| P5-01 | Cedar       | 5    | 15.0000  | -39.1180 | 0.00°    | +6.30 | 95        |
| P5-02 | Laurel      | 5    | 30.0000  | -39.1180 | 0.00°    | +6.30 | 95        |
| P5-03 | Myrtle      | 5    | 45.0000  | -39.1180 | 0.00°    | +6.30 | 95        |
| P3-01 | Sage        | 3    | -41.0000 | -9.6180  | 0.00°    | +3.30 | 95        |
| P3-02 | Rosemary    | 3    | -23.8000 | -9.6180  | 0.00°    | +3.30 | 95        |
| P4-01 | Almond      | 4    | -2.0000  | -9.6180  | 0.00°    | +3.30 | 95        |
| P4-02 | Fig         | 4    | 12.0000  | -9.6180  | 0.00°    | +3.30 | 95        |
| P4-03 | Pomegranate | 4    | 26.0000  | -9.6180  | 0.00°    | +3.30 | 95        |
| P1-01 | Jasmine     | 1    | -44.0303 | 30.8794  | -9.60°   | +0.30 | 95        |
| P1-02 | Lavender    | 1    | -30.0303 | 33.1794  | -9.60°   | +0.30 | 95        |
| P1-03 | Iris        | 1    | -16.5303 | 35.4794  | -9.60°   | +0.30 | 95        |
| P2-01 | Thyme       | 2    | 36.5000  | 19.1820  | 0.00°    | +0.30 | 95        |
| P2-02 | Arbutus     | 2    | 22.0000  | 37.1820  | 0.00°    | +0.30 | 95        |

| PER HOME              | OPEN    | DRESSING |
|-----------------------|---------|----------|
| Ground usable         | 62.7208 | 62.7208  |
| Loft usable           | 32.2792 | 32.2792  |
| TOTAL USABLE          | 95      | 95       |
| Gross enclosed floor* | 123.373 | 124.576  |


Development usable total: 1,520.00 m². Smallest enclosed-house separation: 4.29 m. Smallest original plot-boundary clearance: 0.40 m. These gaps are geometric measurements, not evidence of permitted setbacks.

\* Gross is an illustrative outside-face envelope including the landing. Usable area is not planning floor area. The historical binder records plot-6 density/coverage constraints; current rights and loft treatment need the appointed architect’s review.



The shared garden / space to come together

Pool, padel, café, gym and planted paths. Exterior landscaping is a concept proposal.

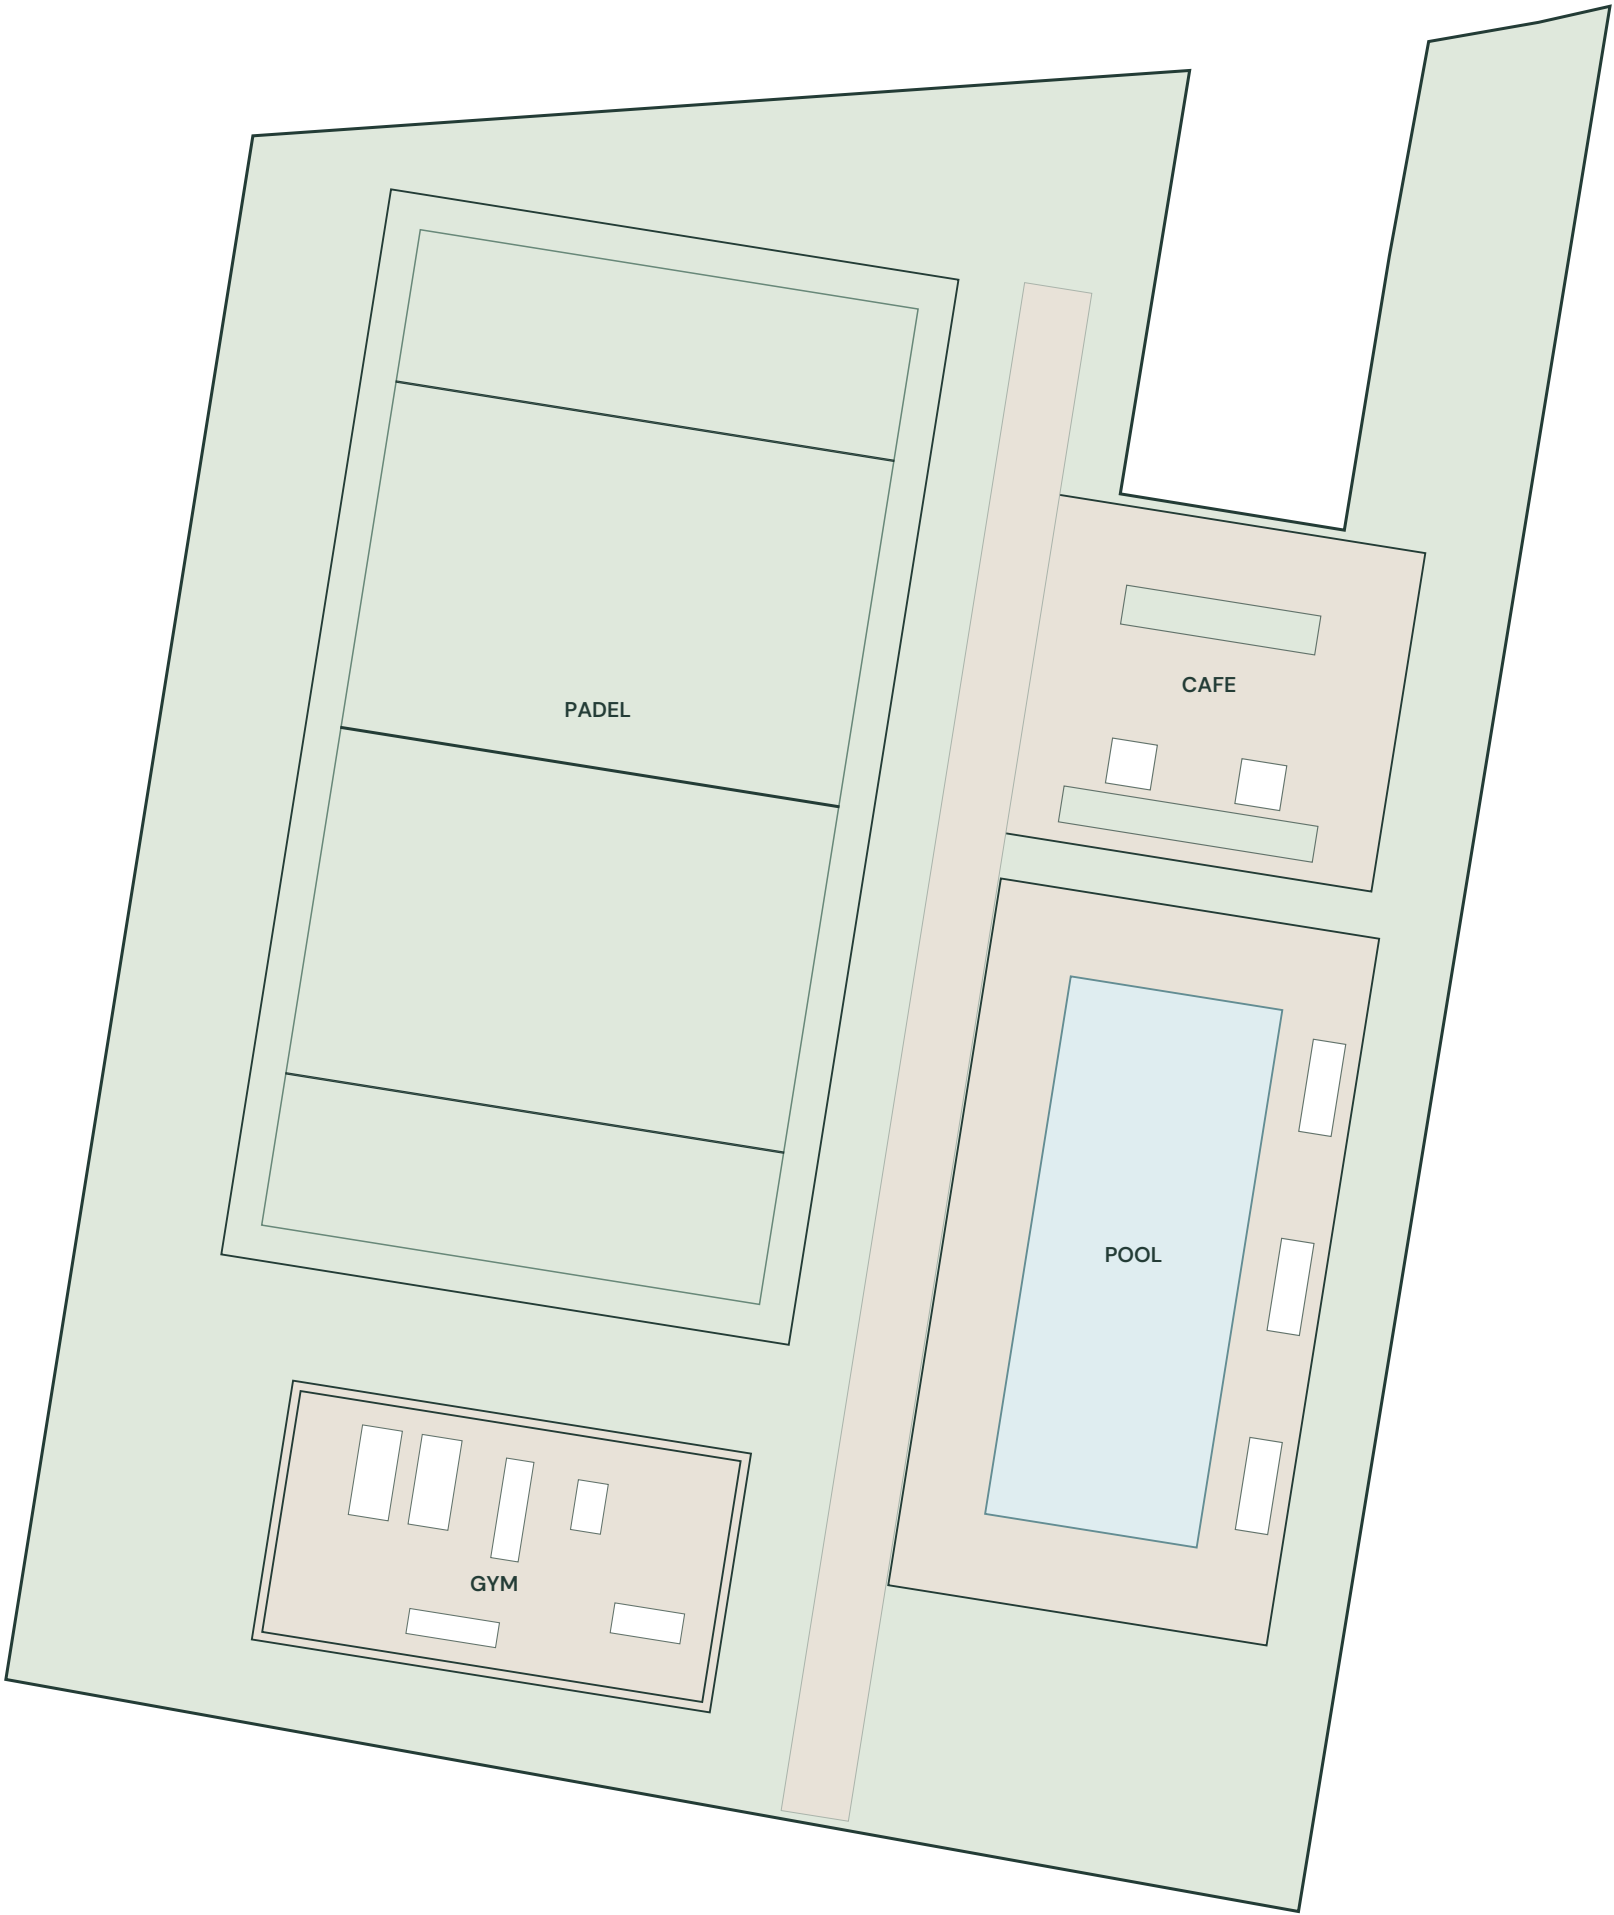

Development and coordination

- 01** Padel playing area: 10 x 20 m. Enclosure, access and compact surrounds are concept layouts. Pool water surface: 4.25 x 10.80 m. Gym pavilion: 9.20 x 5.20 m.
- 02** Thirty-centimetre external timber walls are kept full size in both models. Structural spruce grade, connections, fire performance, insulation, moisture control and foundations require engineering.
- 03** The nominal 2.10 m loft counting threshold follows the shared roof underside. Floor finishes, roof build-up, stair headroom and opening details need a coordinated construction design.
- 04** Private gardens have perimeter walls, a parking bay and a garden kitchen. Boundary walls and retaining sections require drainage and structural design. The larger option has compact rear patios in the tightest parcels.
- 05** Street, garden and common-area fixtures illuminate at dusk/night in the model. Positions are indicative; electrical, glare and access requirements remain to be designed.
- 06** Source basis: manufacturer hand drawing, architect binder, subdivision overview and the owner’s revised placement and landscape instructions. Refer to the Info folder for source material.
- 07** North, plot edges, levels and roads follow the digitized model trace. A fresh measured survey and appointed architect review are required before setting out.

