

143.7 m². Room to live.

Sixteen spruce glulam homes, developed from the manufacturer’s roof and glazing concept. A coordinated architectural study for your appointed architect, matching the selected interactive model.

16

HOMES

143.7

USABLE m² / HOME

2,299.2

DEVELOPMENT m²

A measured design, with choices

- 01
- Outside enclosure 9.400 x 12.0968 m. Ground usable 92.1384 m² plus loft 51.5616 m². Both master arrangements total 143.7 m².
- 02
- Width remains 9.400 m to preserve neighbour gaps. The minimum measured separation between enclosed house faces is 4.29 m. House centres and rotations stay fixed.
- 03
- Two downstairs rooms each measure 3.1175 x 5.0675 m. Bedroom, dining and library options share the same shell.
- 04
- The dressing loft front and stair/landing move forward 178.28 mm to compensate for the extra partitions. Both layouts retain glass toward the living room.
- 05
- Usable area excludes wall/door–reveal bands, ground stair reservation, upper void and loft floor below 2.10 m clear headroom. Fixed cabinetry is included.

Drawing register

SHEET	DRAWING	SCALE
A000	Design brief and drawing register	NTS
A001	Overall site arrangement	1:500
A101	Upper terrace plots 5 and 6	1:250
A102	Middle terrace plots 3 and 4	1:250
A103	Lower terrace plots 1 and 2	1:250
A201	Dimensioned ground floor	1:50
A202	Both master–suite arrangements	1:50
A203	Three lower–left room options	1:25
A204	Bathroom and laundry options	1:25
A301	Four external elevations	1:100
A302	Roof plan and building sections	1:100 / 1:50
A401	Area and placement schedules	NTS
A402	Shared amenities and design coordination	1:150

CONCEPT C03 / ARCHITECT REVIEW

Shared dimensions match the C03 website model. This set does not establish permit rights, legal setbacks or construction details. Plot trace and terrace levels are provisional. Structural, services, drainage, fire and energy designs require appointed consultants.

Do not set out from rounded dimensions. The metre–based CAD and area audit retain full precision.

CONCEPT DESIGN – NOT FOR CONSTRUCTION OR PERMIT SUBMISSION

Dimensions in metres unless stated. Print at 100% on A2 (594 x 420 mm).

PROJECT KH-16-143.7

Brief: 143.7 m² usable per home

SCALE

NTS

DRAWING

A000

SHEET

01 / 13

Overall arrangement / 16 homes of 143.7 m²

Existing centres and orientations retained. Perimeter divisions, private gardens and shared green area.



PLOT	HOMES	USABLE m²
6	3	431.1
5	3	431.1
4	3	431.1
3	2	287.4
1	3	431.1
2	2	287.4

- 01** Upper plots 5/6: +6.00 m. Middle plots 3/4: +3.00 m. Lower plots 1/2: +0.00 m. House finished floors +0.30 m above terrace; relative levels only.
- 02** Only the two source road corridors are shown. Parking access meets the road edge; no extra internal street is introduced.
- 03** Rear gardens on plots 1, 3 and 4; left garden at Thyme and right garden at Arbutus. Larger homes require more compact terraces.
- 04** Private divisions are landscape proposals, not cadastral boundaries. Gate locations and retaining walls need measured survey coordination.

Upper terrace / homes, gardens and arrivals

143.7 m² usable per home. Enclosed footprint 9.400 x 12.0968 m; porch additional.



HOME	NAME	FFL	GARDEN	PLOT GAP*	PARCEL GAP*
P6-01	Olive	+6.30	front	3.40	3.40
P6-02	Cypress	+6.30	front	4.71	2.40
P6-03	Juniper	+6.30	front	4.23	2.40
P5-01	Cedar	+6.30	front	3.36	3.36
P5-02	Laurel	+6.30	front	4.85	1.90
P5-03	Myrtle	+6.30	front	4.96	1.90

* Shortest enclosed-face distance to the plot or private division. These are measured model clearances, not approved setbacks. Roof overhangs and wall construction require separate review.

Every home retains a 2.70 x 5.20 m parking bay and direct road connection. Gate fabrication is not defined.

Middle terrace / homes, gardens and arrivals

143.7 m² usable per home. Enclosed footprint 9.400 x 12.0968 m; porch additional.



* Shortest enclosed-face distance to the plot or private division. These are measured model clearances, not approved setbacks. Roof overhangs and wall construction require separate review.

Every home retains a 2.70 x 5.20 m parking bay and direct road connection. Gate fabrication is not defined.

Lower terrace / homes, gardens and arrivals


143.7 m² usable per home. Enclosed footprint 9.400 x 12.0968 m; porch additional.



HOME	NAME	FFL	GARDEN	PLOT GAP*	PARCEL GAP*
P1-01	Jasmine	+0.30	rear	1.55	1.55
P1-02	Lavender	+0.30	rear	5.38	2.15
P1-03	Iris	+0.30	rear	0.39	0.39
P2-01	Thyme	+0.30	left	1.54	1.54
P2-02	Arbutus	+0.30	right	1.45	0.83

* Shortest enclosed-face distance to the plot or private division. These are measured model clearances, not approved setbacks. Roof overhangs and wall construction require separate review.

Every home retains a 2.70 x 5.20 m parking bay and direct road connection. Gate fabrication is not defined.

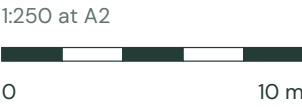

Ground floor / furnished arrangement

92.1384 m² counted usable. All three left-room options use this enclosure.



Space for everyday life

GROUND FLOOR	AREA m²
Inside external walls	101.1723
Less full partition bands	3.5067
Less stair / guard reservation	5.5272
USABLE GROUND FLOOR	92.1384

- 01
- Each rear room: 15.7979 m² clear before furnishings. Central bath: 2.235 x 3.0403 m clear beyond the plumbing ledge. External walls 300 mm; internal wall bands 165 mm.
- 02
- Side-wall TV faces the sofa. A fitted reading bench uses the space beneath the loft; the 2.40 m island has clear working aisles and drawers below the kitchen windows.
- 03
- Stair concept: 18 equal rises over 3.235 m (179.72 mm each), 280 mm goings, 940 mm clear flight, upper landing 1.160 x 1.040 m. Verify structure, handrails, headroom and finished tolerances.
- 04
- This ground plan shows the open-suite stair position. With the dressing loft, the stair reservation moves 178.28 mm toward the front; usable area is unchanged.
- 05
- 1.330 m clear sheltered porch between the extended side walls. The open porch is excluded from usable and enclosed floor area.

CO3: rear rooms shortened 1.20 m. Ground bath includes stacked washer/dryer and a closed plumbing ledge; this replaces the removed wall area while maintaining the usable total.



A / Open master suite

Bathroom partition with open clothes storage; retained glazed frontage.



B / Walk-in wardrobe suite

Glazed frontage and landing advance 178.28 mm.



COUNTING METHOD	OPEN	DRESSING
Clear room floor	54.1199	54.2269
Below 2.10 m (excluded)	3.7647	3.8718
Landing included	1.2064	1.2064
USABLE LOFT	51.5616	51.5616


Ochre bands identify the low-headroom floor excluded from usable area. The threshold is a project counting assumption, not a statement of statutory habitable-room compliance. Cabinetry in these strips stays under the roof.

Both loft choices plus the ground floor total 143.7 m². The 0.90 m sliding entrance aligns with the landing.


The lower-left room / three ways to live

Identical finished dimensions: 3.1175 x 5.0675 m. Each option: 15.7979 m².


01 / BEDROOM

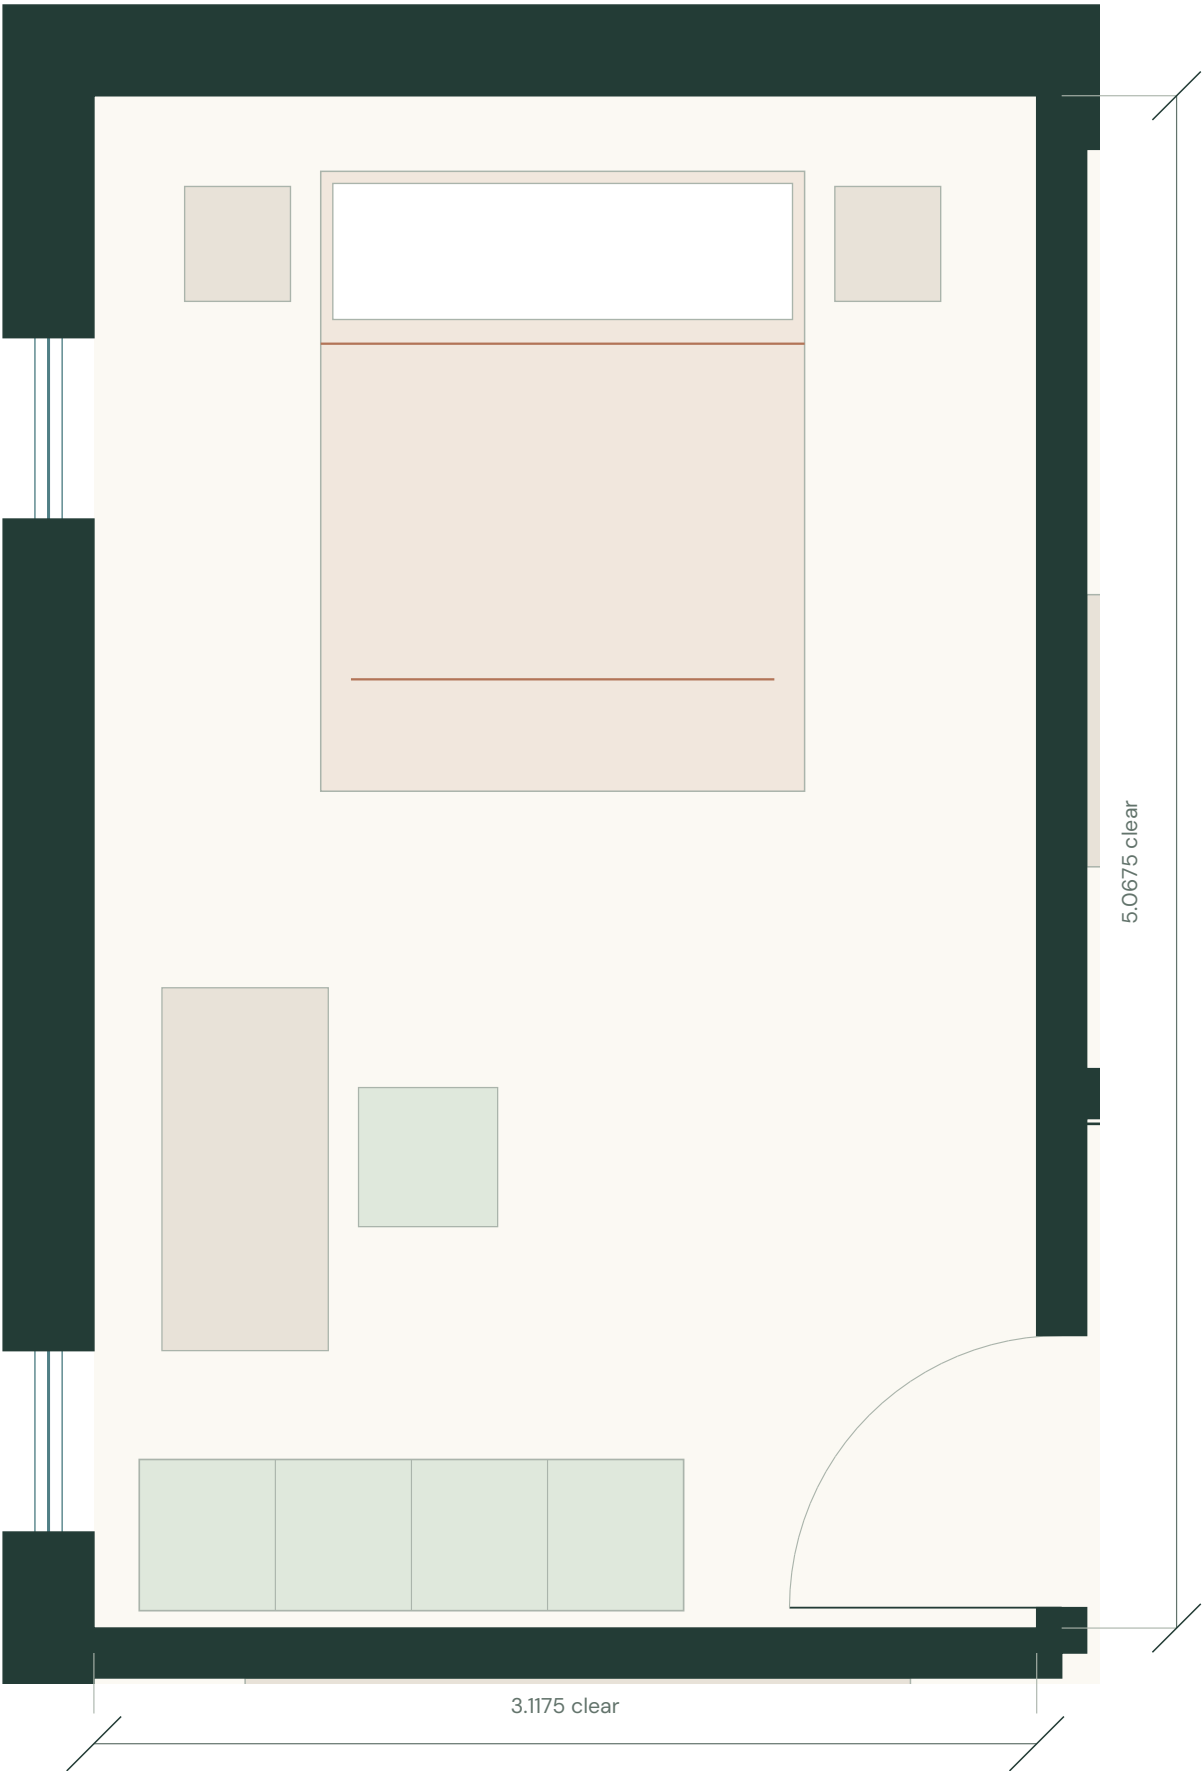

02 / ROUND DINING

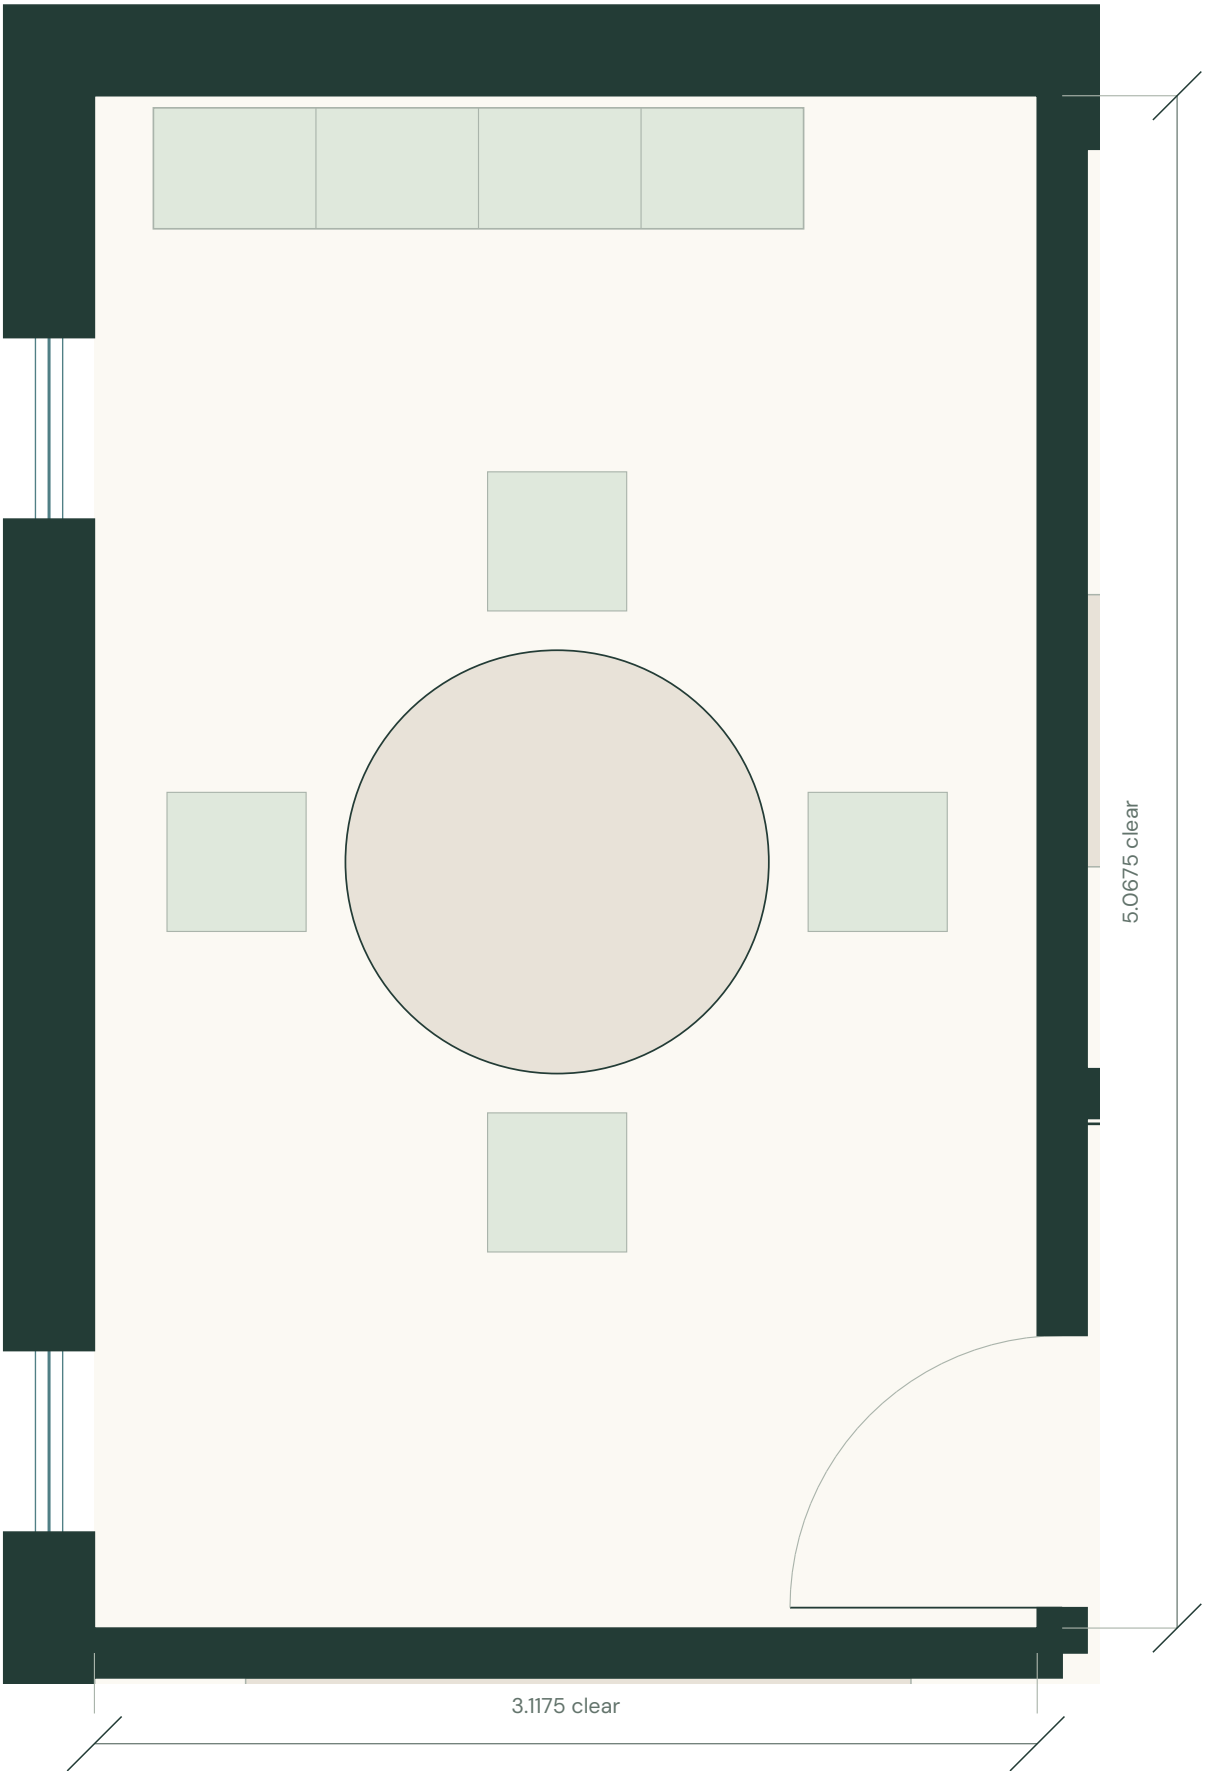


03 / LIBRARY + DESK

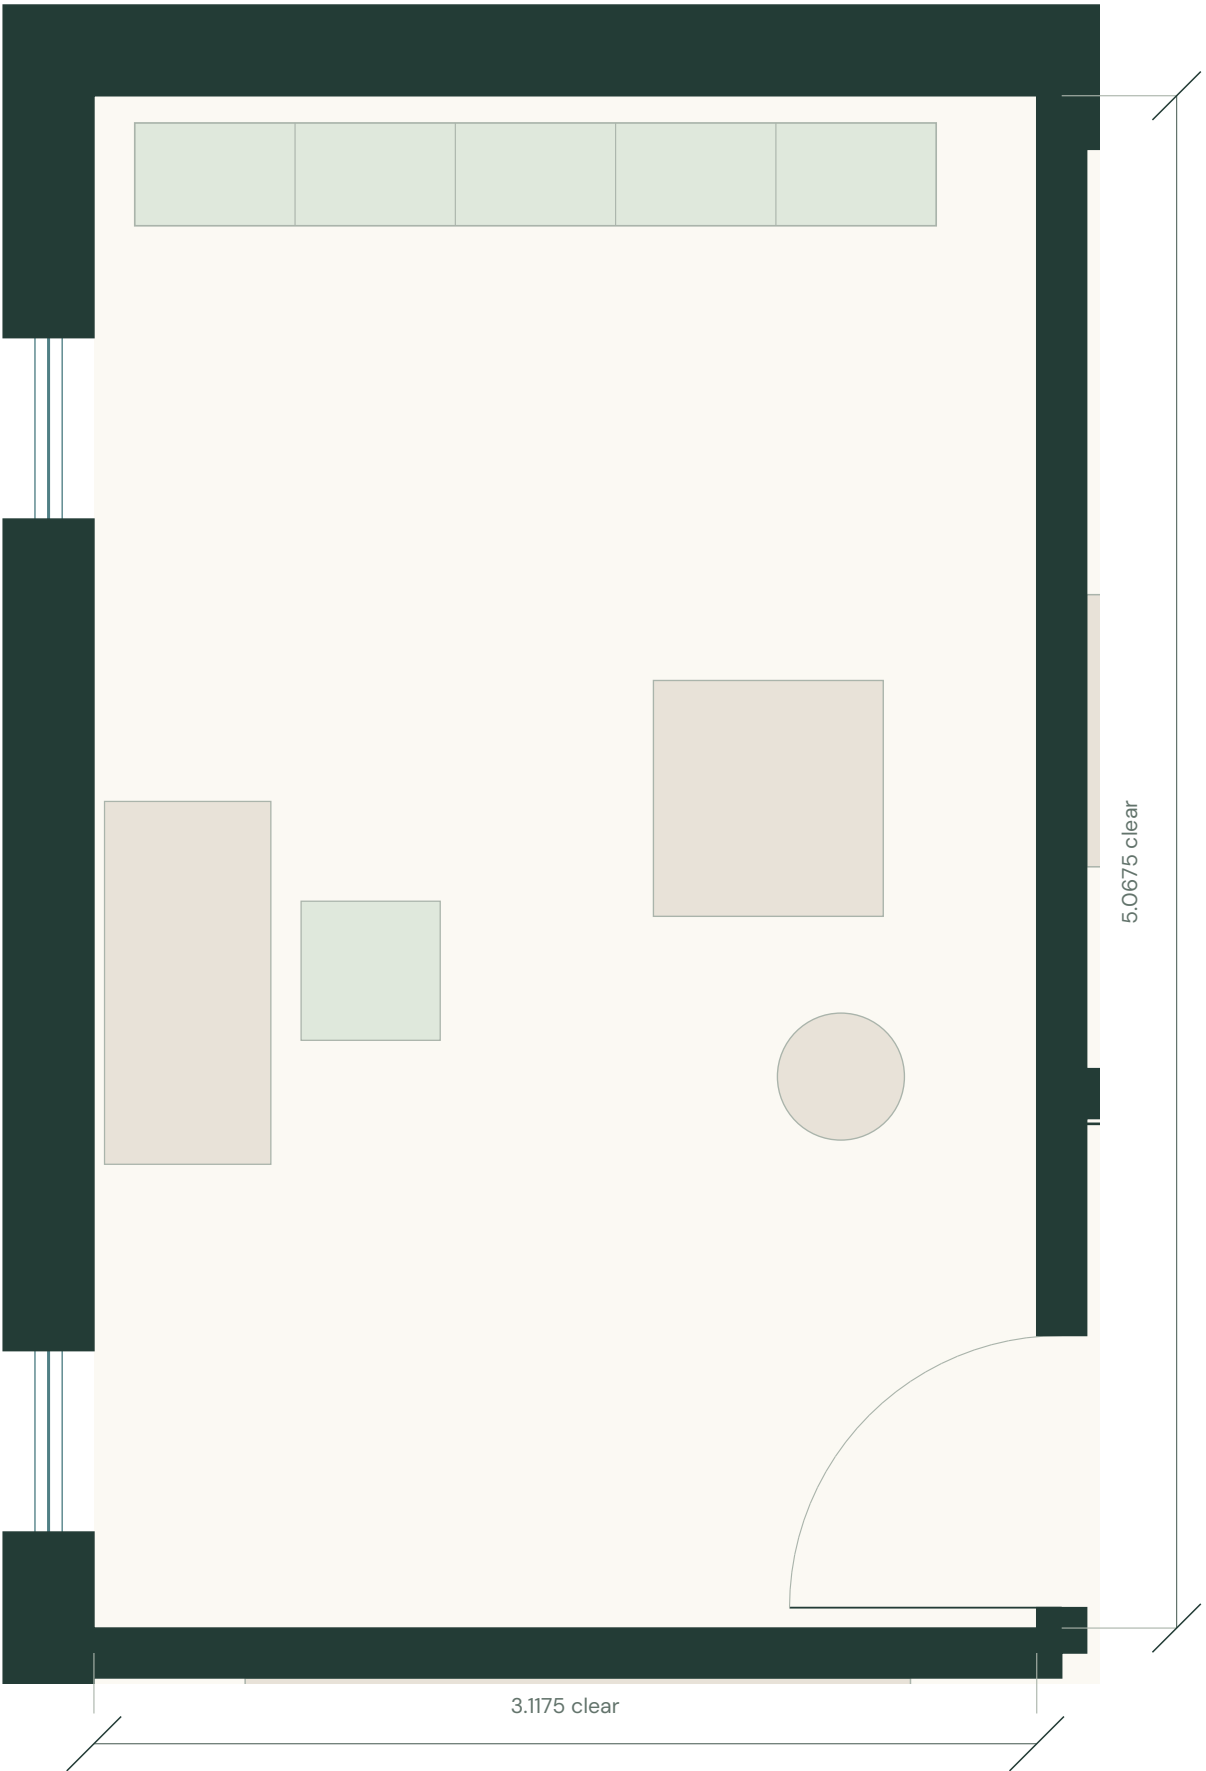

Bathrooms / comfort, laundry and choices

1:25. Fixture positions match the C03 model. Blue bath outlines are optional; shower-only replaces the bath with a towel bench.


GROUND / SHOWER + LAUNDRY

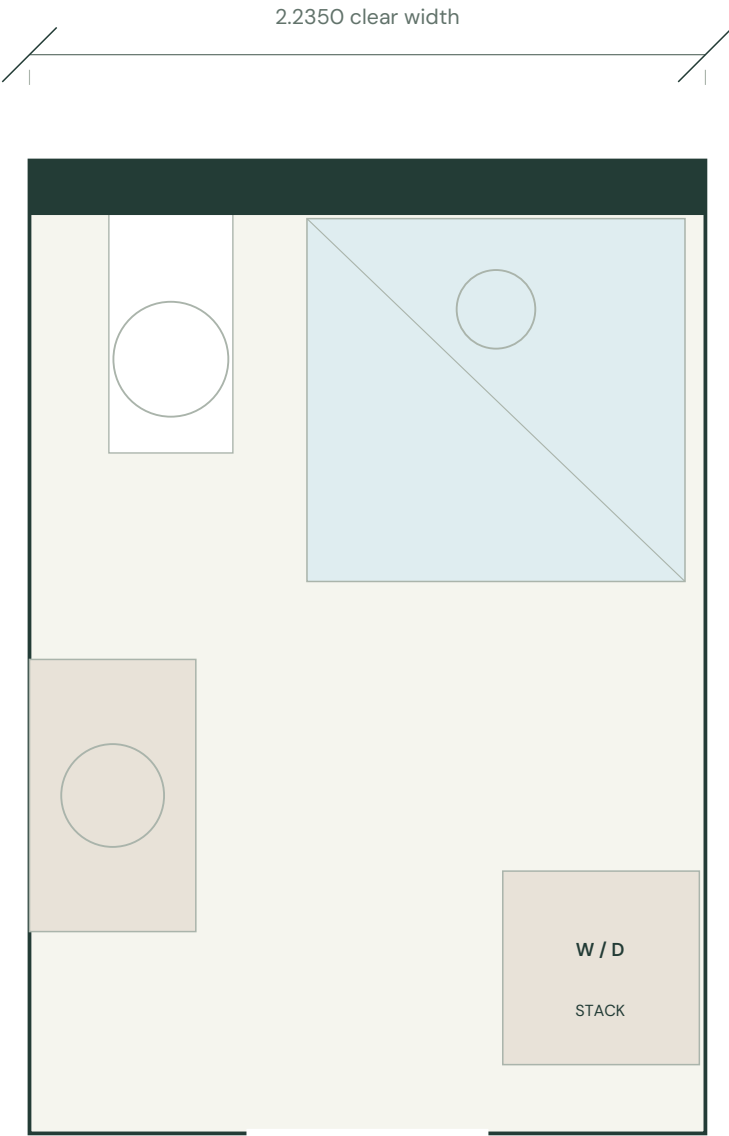

A 1.25 x 1.20 m shower, wall-backed WC, 0.90 m vanity and a 0.64 x 0.65 m stacked washer/dryer. Sliding entry avoids a door swing into appliances.


Bathroom variants do not alter the floor-area total. Clothes storage flanks both sides of the open-suite bathroom doorway. Plumbing, waterproofing, ventilation and electrical zones require detailed coordination.

OPEN SUITE / SHOWER + BATH

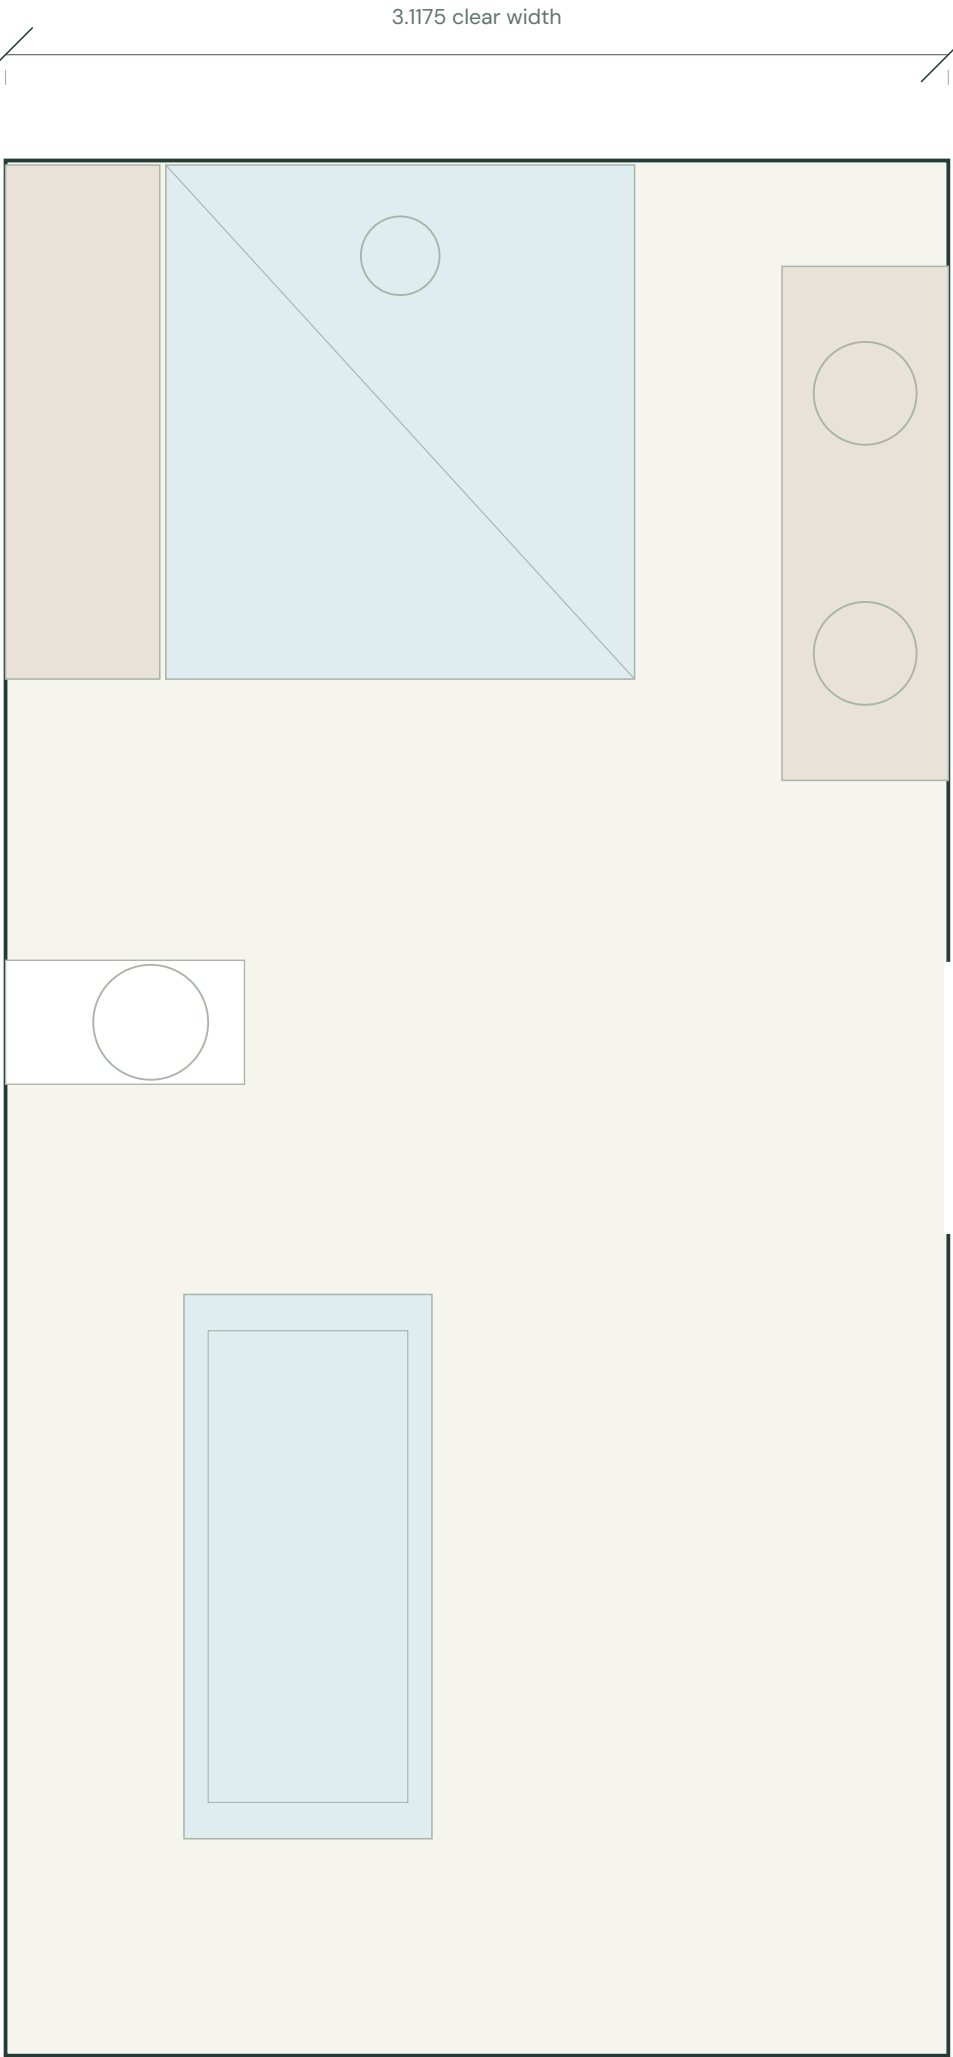

A 1.55 x 1.70 m walk-in shower and 1.70 m wall-backed double vanity. Optional 0.82 x 1.80 m bath; remove it for a towel bench and open floor.


WALK-IN SUITE / SHOWER + BATH

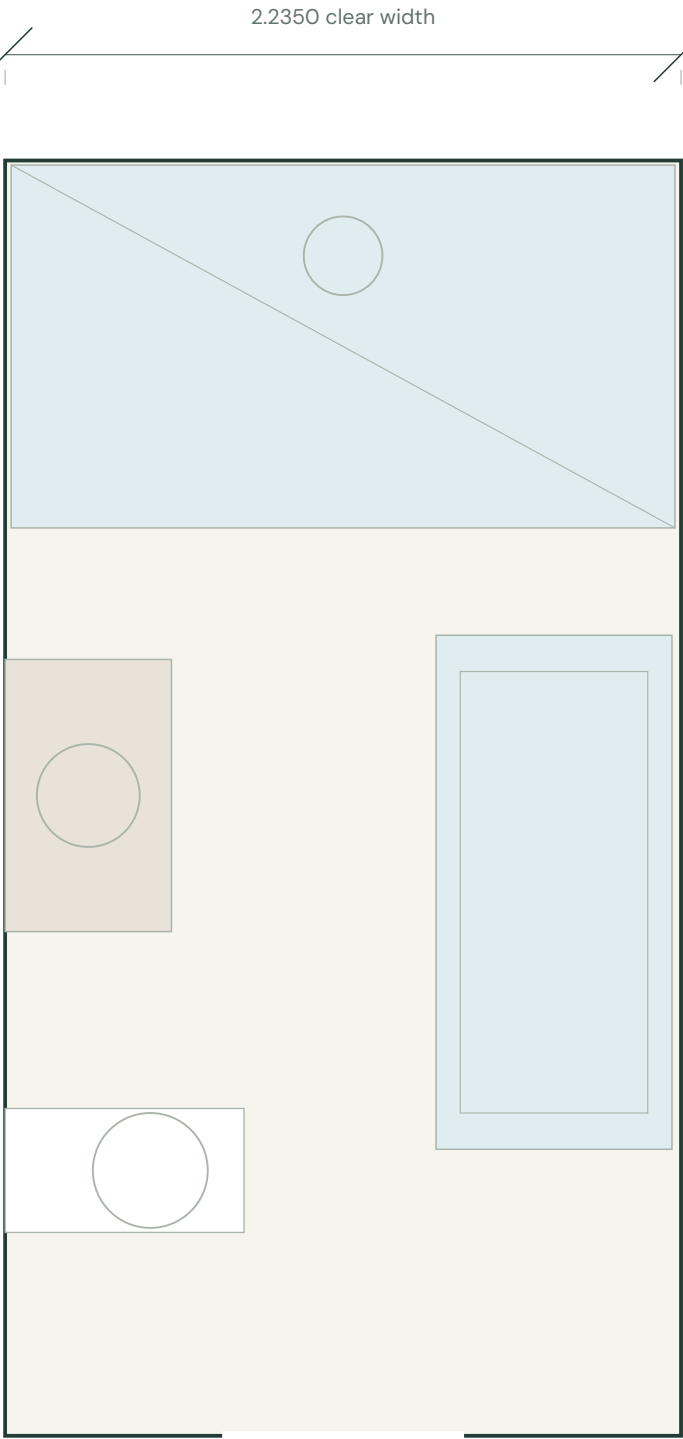


A 2.195 x 1.20 m shower, wall-backed vanity and side-wall WC. Optional 0.78 x 1.70 m bath keeps an approximately 0.87 m aisle beside the vanity.

Elevations / timber, glazing and shelter

Horizontal spruce courses, grey roof and a raised glazed living volume. Openings are concept dimensions.

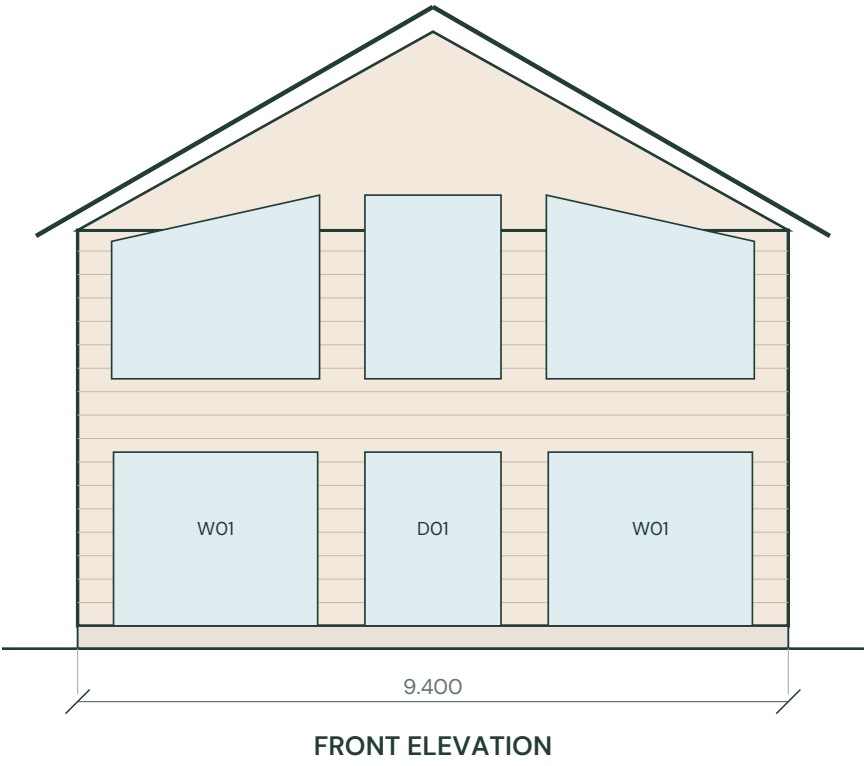

Roof pitch 30°. Loft FFL +3.235 m. Knee structure 2.000 m above loft. Ridge structure +7.862 m. Roof build-up and flue height require engineering.

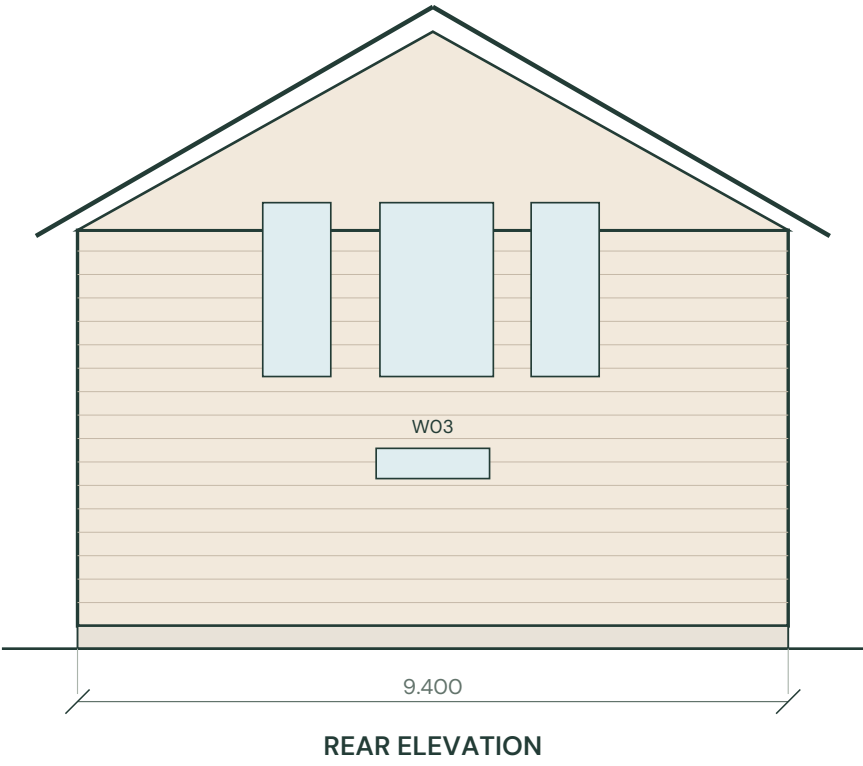

Roof pitch 30°. Loft FFL +3.235 m. Knee structure 2.000 m above loft. Ridge structure +7.862 m. Roof build-up and flue height require engineering.




Roof and side-wall heights remain common to both house sizes. Front porch wings project 1.330 m beyond enclosure. All vertical levels are relative to house FFL.



Roof and side-wall heights remain common to both house sizes. Front porch wings project 1.330 m beyond enclosure. All vertical levels are relative to house FFL.


Roof plan / sheltered front

1:100. Roof overhangs are separate from the enclosed and usable areas.

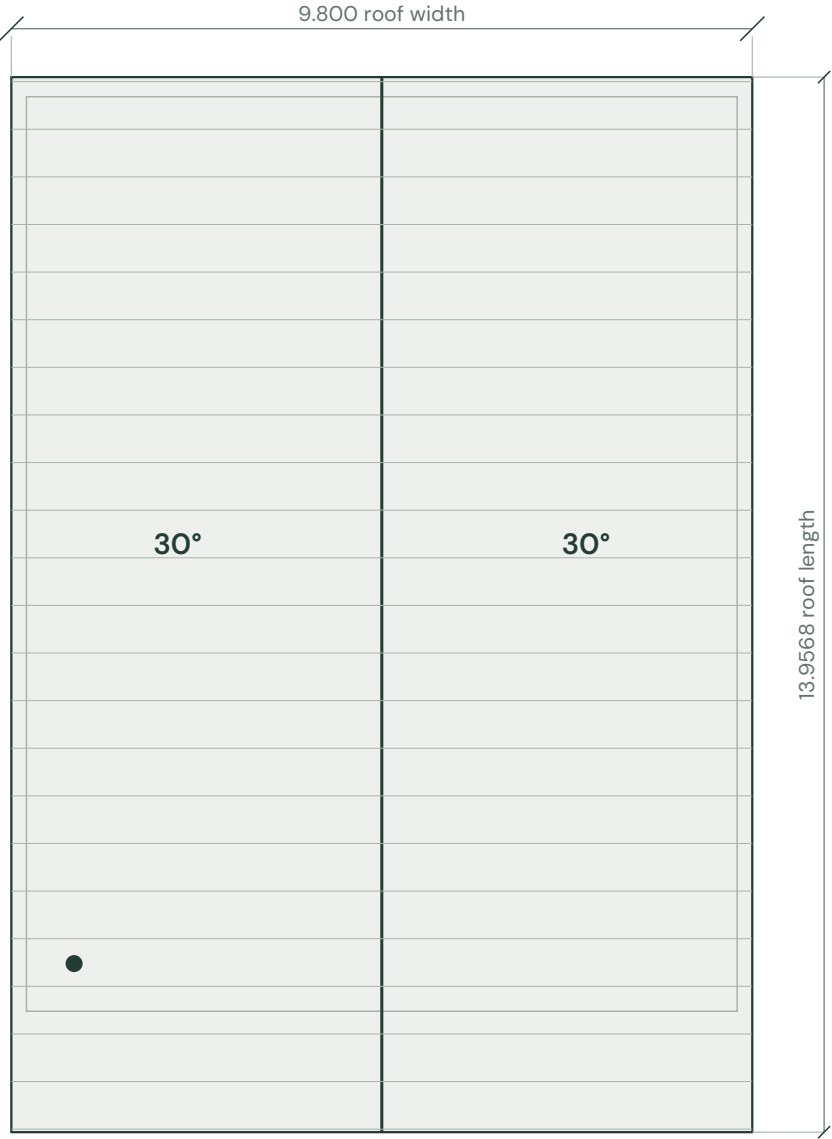

Longitudinal section / at the loft arrival

1:100. The glazed master overlooks the double-height living room.

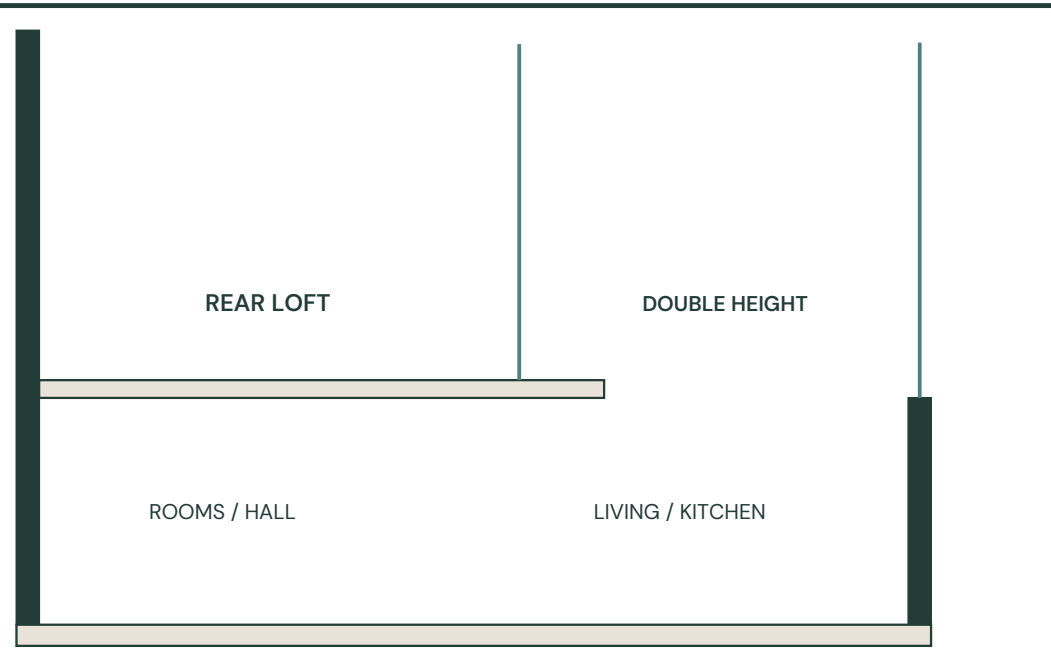

Transverse section / rear loft

1:50. Ground-floor finished level is the local 0.000 datum.



The roof underside at the loft eaves controls the excluded low-headroom strips. External walls remain 300 mm. The roof, floor and timber connections shown here are indicative assemblies; an engineer must design spans, members, foundations and restraint.

The roof top is approximately 8.19 m above house FFL, or 8.49 m above its garden. Confirm applicable height datum and planning limits with the appointed architect.

Usable area and placement register

All local coordinates are metres. Do not treat this model trace as a cadastral survey.

HOME	NAME	PLOT	CENTRE X	CENTRE Z	ROTATION	FFL	USABLE m²
P6-01	Olive	6	-34.0000	-39.1180	0.00°	+6.30	143.7
P6-02	Cypress	6	-18.0000	-39.1180	0.00°	+6.30	143.7
P6-03	Juniper	6	-2.0000	-39.1180	0.00°	+6.30	143.7
P5-01	Cedar	5	15.0000	-39.1180	0.00°	+6.30	143.7
P5-02	Laurel	5	30.0000	-39.1180	0.00°	+6.30	143.7
P5-03	Myrtle	5	45.0000	-39.1180	0.00°	+6.30	143.7
P3-01	Sage	3	-41.0000	-9.6180	0.00°	+3.30	143.7
P3-02	Rosemary	3	-23.8000	-9.6180	0.00°	+3.30	143.7
P4-01	Almond	4	-2.0000	-9.6180	0.00°	+3.30	143.7
P4-02	Fig	4	12.0000	-9.6180	0.00°	+3.30	143.7
P4-03	Pomegranate	4	26.0000	-9.6180	0.00°	+3.30	143.7
P1-01	Jasmine	1	-44.0303	30.8794	-9.60°	+0.30	143.7
P1-02	Lavender	1	-30.0303	33.1794	-9.60°	+0.30	143.7
P1-03	Iris	1	-16.5303	35.4794	-9.60°	+0.30	143.7
P2-01	Thyme	2	36.5000	19.1820	0.00°	+0.30	143.7
P2-02	Arbutus	2	22.0000	37.1820	0.00°	+0.30	143.7


PER HOME	OPEN	DRESSING
Ground usable	92.1384	92.1384
Loft usable	51.5616	51.5616
TOTAL USABLE	143.7	143.7
Gross enclosed floor*	178.202	179.878

Development usable total: 2,299.20 m². Smallest enclosed-house separation: 4.29 m. Smallest original plot-boundary clearance: 0.39 m. These gaps are geometric measurements, not evidence of permitted setbacks.

* Gross is an illustrative outside-face envelope including the landing. Usable area is not planning floor area. The historical binder records plot-6 density/coverage constraints; current rights and loft treatment need the appointed architect’s review.

The shared garden / space to come together

Pool, padel, café, gym and planted paths. Exterior landscaping is a concept proposal.

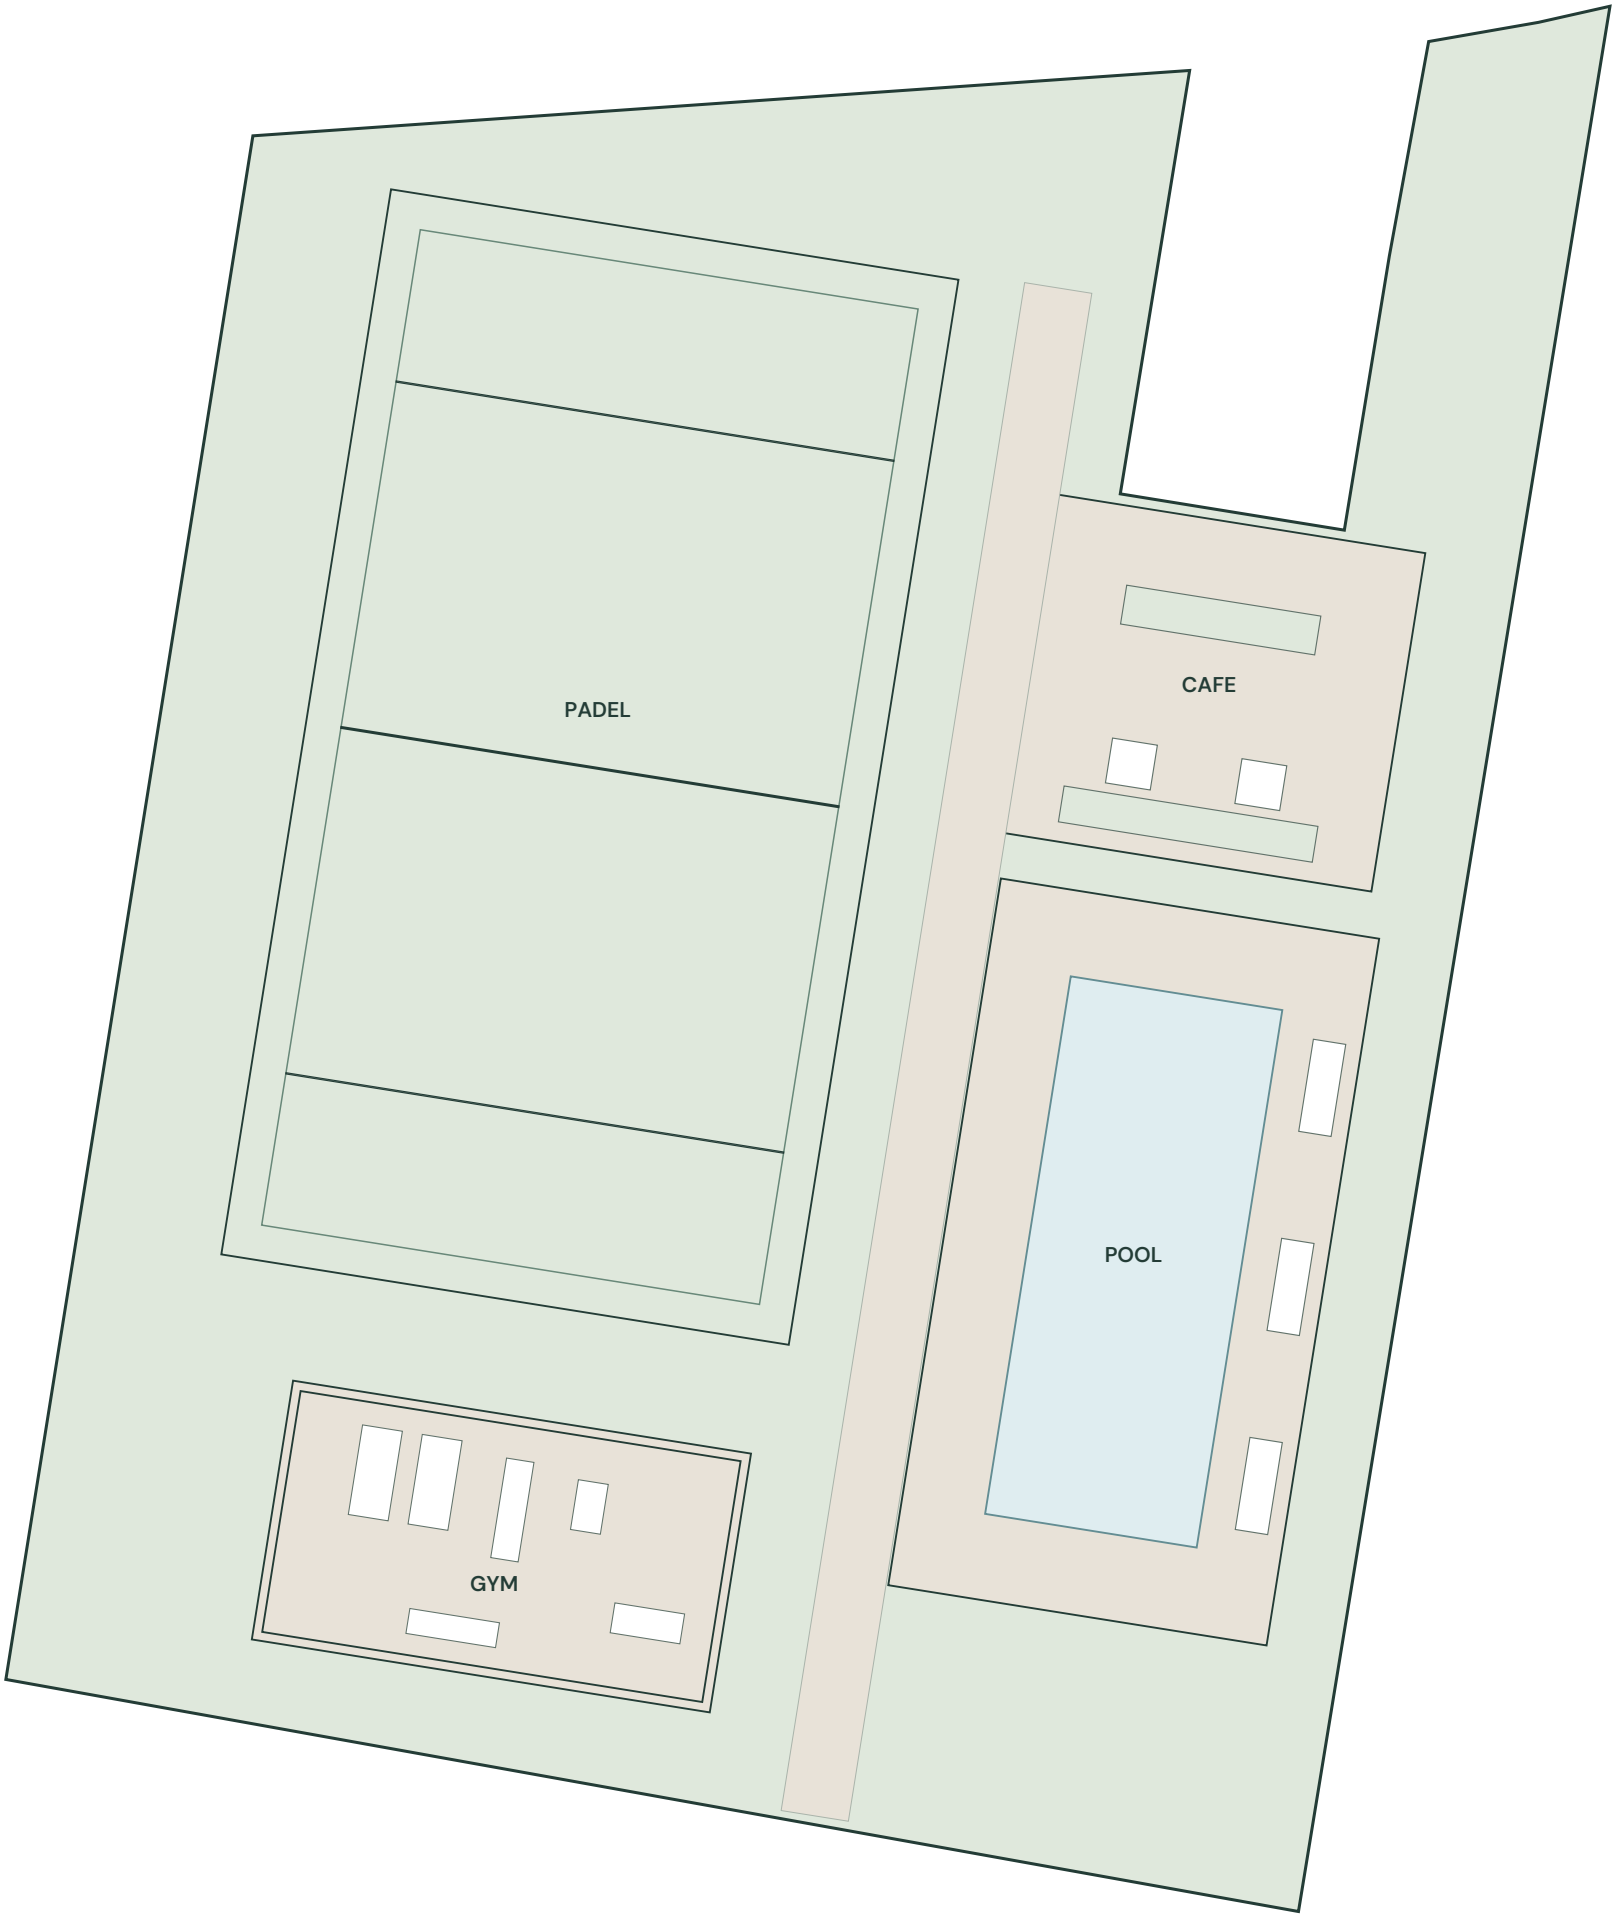

Development and coordination

- 01** Padel playing area: 10 x 20 m. Enclosure, access and compact surrounds are concept layouts. Pool water surface: 4.25 x 10.80 m. Gym pavilion: 9.20 x 5.20 m.
- 02** Thirty-centimetre external timber walls are kept full size in both models. Structural spruce grade, connections, fire performance, insulation, moisture control and foundations require engineering.
- 03** The nominal 2.10 m loft counting threshold follows the shared roof underside. Floor finishes, roof build-up, stair headroom and opening details need a coordinated construction design.
- 04** Private gardens have perimeter walls, a parking bay and a garden kitchen. Boundary walls and retaining sections require drainage and structural design. The larger option has compact rear patios in the tightest parcels.
- 05** Street, garden and common-area fixtures illuminate at dusk/night in the model. Positions are indicative; electrical, glare and access requirements remain to be designed.
- 06** Source basis: manufacturer hand drawing, architect binder, subdivision overview and the owner’s revised placement and landscape instructions. Refer to the Info folder for source material.
- 07** North, plot edges, levels and roads follow the digitized model trace. A fresh measured survey and appointed architect review are required before setting out.

